

Эскизный проект

Архитектурные решения
квартиры по адресу:
г. Москва,
ЖК "Headliner" 39/1

Дизайнер: Заика Нина _____
Компания: «Кодолов Групп» _____



г. Владивосток, ул. Енисейская, 23 Б
+7 999 058 31 91 | 2676421@mail.ru
kodolov.group



Содержание проекта:

1. Обмерный план существующей планировки.....	3
2. Визуализации интерьера.....	4–14
3. План монтажа и демонтажа перегородок.....	15
4. План заполнения дверных проемов	16
5. План привязки сантехнического оборудования и кондиционеров.....	17
6. План расстановки мебели и оборудования.....	18
7. План потолка с указанием площадей.....	19
8. План размещения осветительных приборов	20
9. План выключателей с привязкой к группам света.....	21
10. План размещения розеток.....	22
11. План раскладки материалов пола.....	23
12. План раскладки теплого пола.....	24
13. Развертки по гардеробу (отделка стен, расстановка мебели).....	25
14. Развертки по спальне (отделка стен, расстановка мебели).....	26
15. Развертки по спальне (отделка стен, расстановка мебели).....	27
16. Развертки по прихожей (отделка стен, расстановка мебели).....	28
17. Развертки по кухне (отделка стен, расстановка мебели).....	29
18. Развертки по кухне (отделка стен, расстановка мебели).....	30
19. Развертки по гостиной (отделка стен, расстановка мебели).....	31
20. Развертки по гостиной (отделка стен, расстановка мебели).....	32
20. Развертки по душевой (отделка стен, расстановка мебели).....	33
21. Ведомость учета материалов.....	34–35

Общие указания:

1. Комплект рабочих чертежей разработан на основании обмеров. Все размеры округлены до ± 5 мм;
2. Любые отступления от проекта необходимо согласовать с автором проекта и заказчиком;
3. Все размеры носят ориентировочный характер и уточняются по месту после демонтажных и монтажных работ;
4. При обнаружении неточности на чертежах, просьба сообщить дизайнеру и уточнить информацию;
5. Подрядчикам, выполняющим проектирование вентиляции, сплит-систем и прочего инженерного оборудования, необходимо ознакомиться с полным дизайн проектом, в том числе с визуализациями. Необходимо учитывать размеры, указанные на плане монтажа, плане потолка, плане размещения светильников, а также плане мебели. Также необходимо предусмотреть и указать на схеме все необходимые люки ревизии, их размер и расположение. Отметить все оборудование, к которому необходим доступ. Важно организовать доступ к оборудованию таким образом, чтобы люк не нарушал размещение светильников, декоративных лепных элементов, перепада высот потолков и полов, а также не попадал на места примыкания встраиваемой мебели. Проект по вентиляции необходимо утвердить и подписать до начала монтажных работ. В случае отсутствия возможности разместить оборудование, не нарушив дизайн-проект – просьба связаться с дизайнером для внесения корректировок. В случае, если данные требования подрядчиком не были выполнены, и монтаж инженерных систем привел к существенным изменениям в проекте и/или повлек непоправимые последствия, влияющие на внешний вид и функциональные особенности помещения, вина и обязанность по исправлению недочетов ложится на подрядчика, выполнявшего работу.
6. Чертежи на изготовление мебели, а так же изделий индивидуального изготовления разрабатывают производители, после контрольного замера на объекте. Данные чертежи могут быть использованы для расчета изделий.

Все размеры уточнить на стадии
производственных работ


ОБМЕРНЫЙ ПЛАН

УСЛОВНЫЕ ОБОЗНАЧЕНИЯ

- Стены существующие бетон
- Стены существующие пеноблок

Высота проектируемого помещения
H=3110мм

Общая площадь проектирования
78,4 кв.м.

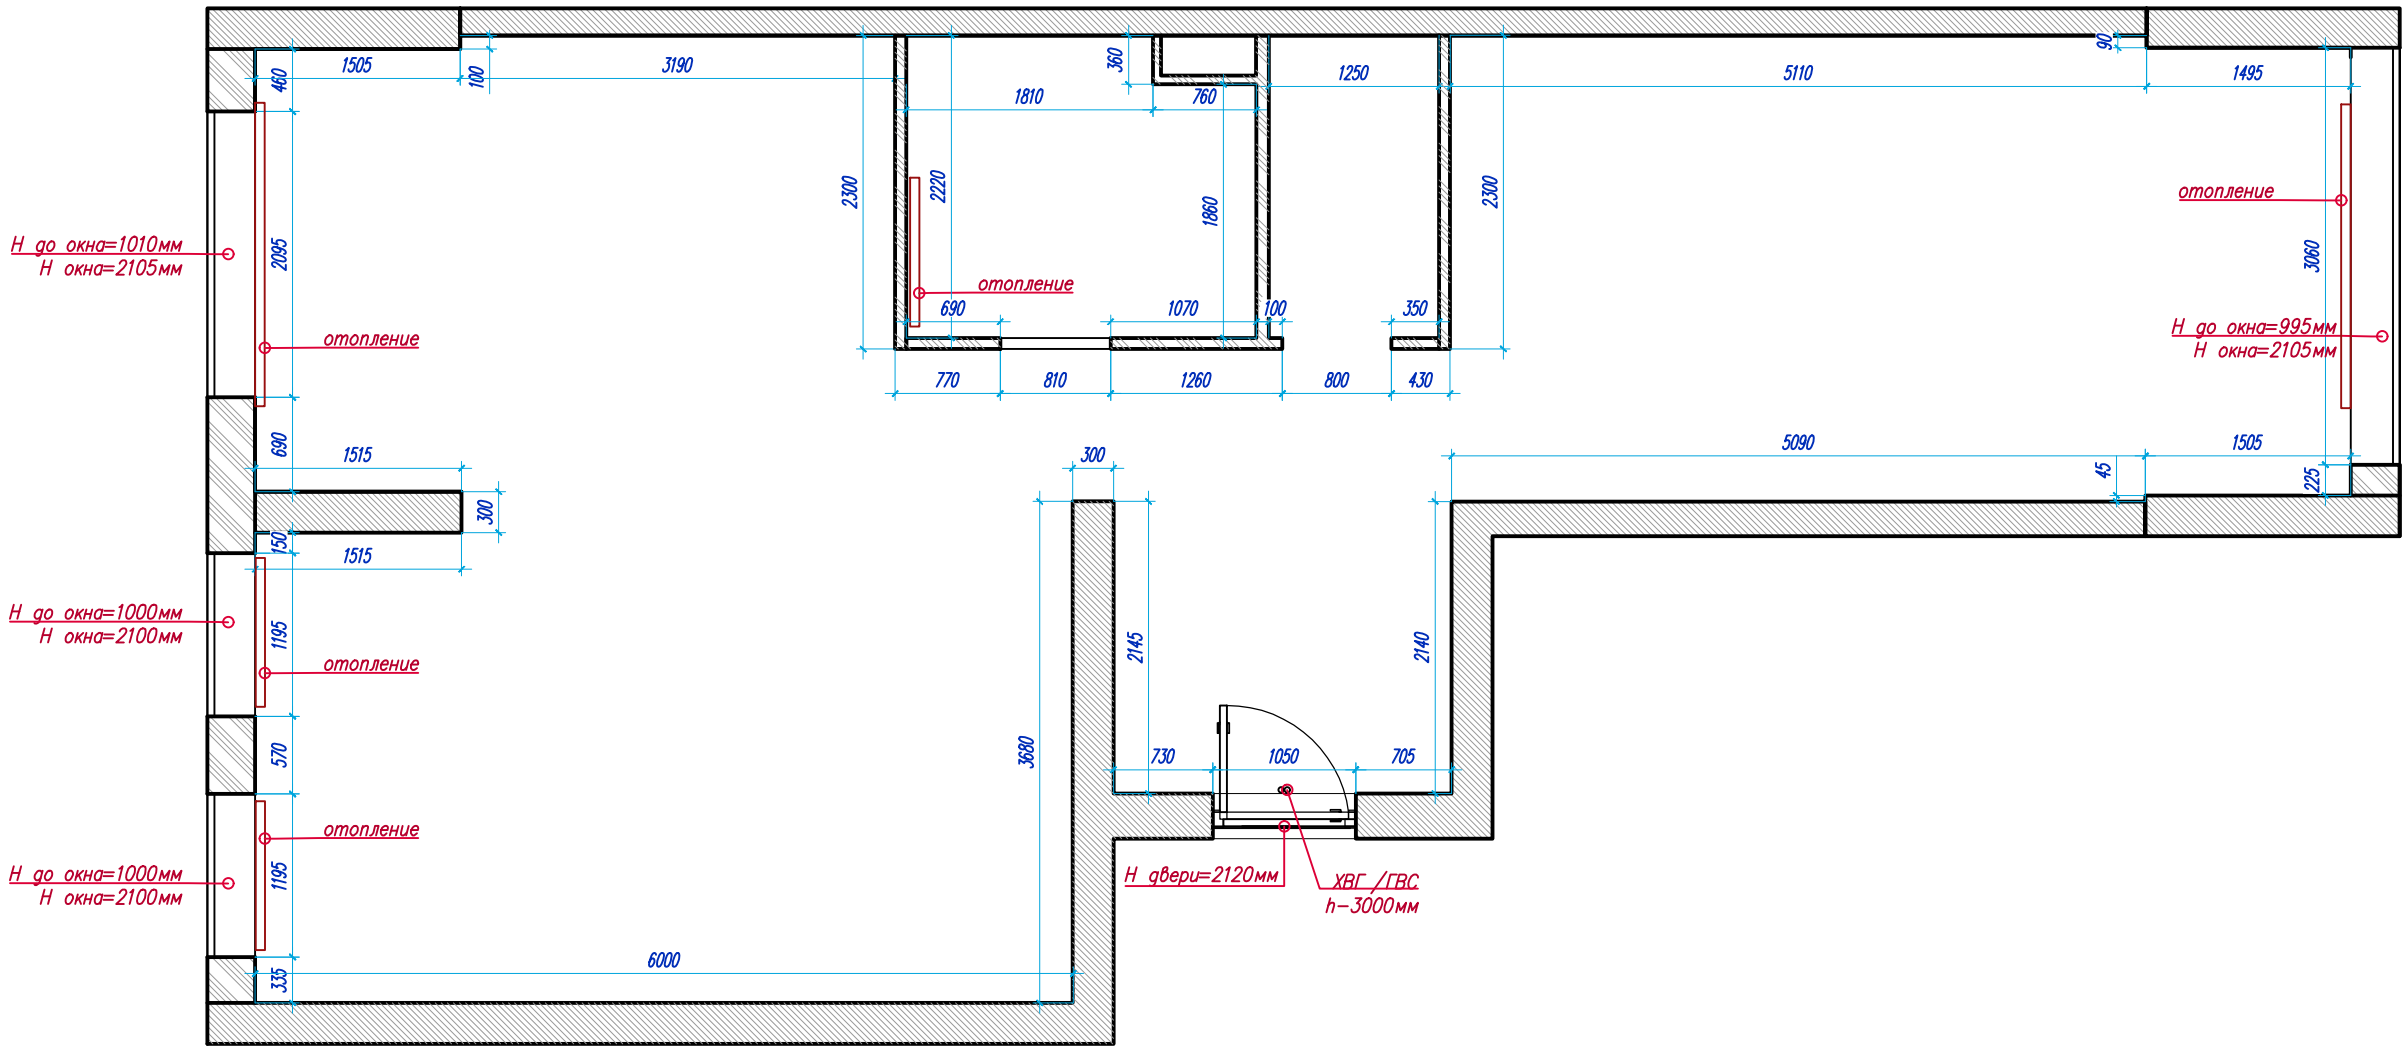

Примечание:
Все размеры и отметки, расход всех материалов, все площади уточняются по месту. На каждом объекте возможны увеличения или уменьшения размеров в зависимости от технических допусков, кривизны, расхождения уровней стен и потолков.


Дизайн проект интерьера
квартиры по адресу:
г. Москва ЖК "Headliner" 39/1

Стадия	Лист	Листов
РП	3	
Компания	Кодолов Групп	
Дизайнер	Заика Нина	
Дата	11.2022	

ВИЗУАЛИЗАЦИЯ ИНТЕРЬЕРА (прихожая, коридор)

УСЛОВНЫЕ ОБОЗНАЧЕНИЯ

3D-визуализации интерьера
могут частично отличаться от
чертежей и даны для понимания
общей концепции.
Дизайн-проект реализуется по
рабочей документации

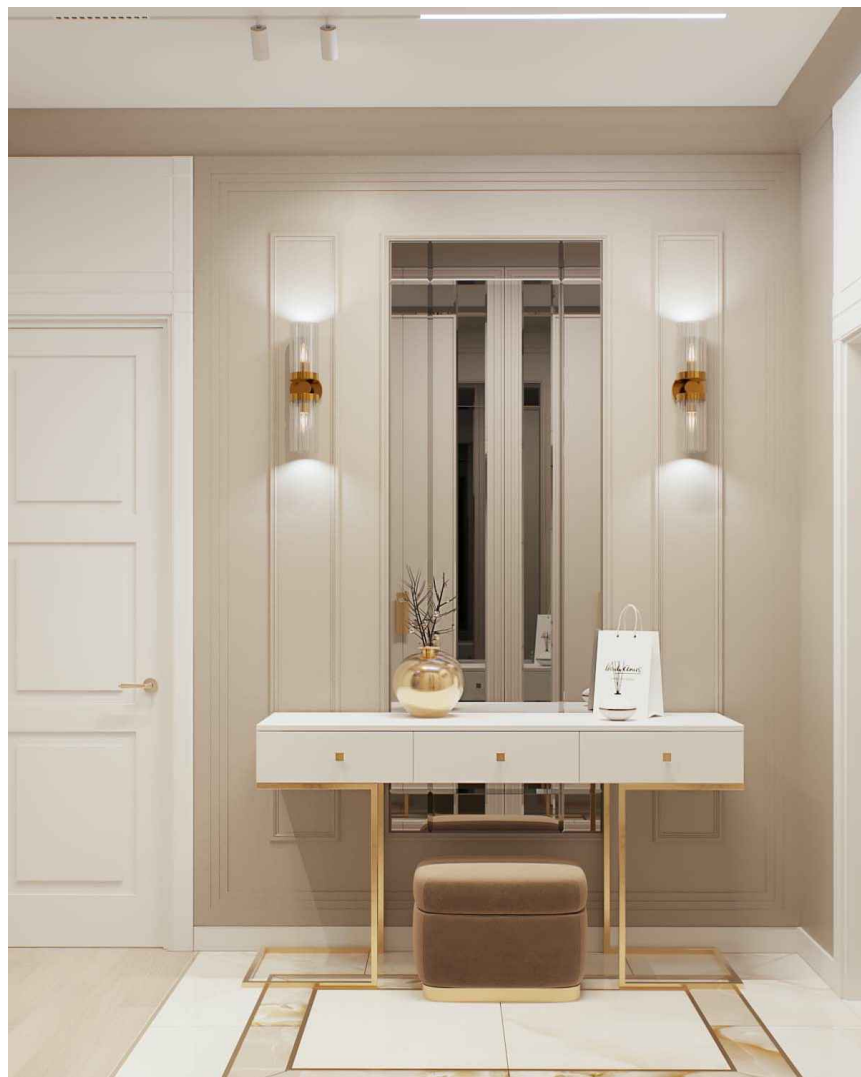


Дизайн проект интерьера
квартиры по адресу:
г. Москва ЖК "Headliner" 39/1

Стадия	Лист	Листов
РП	4	
Компания	Кодолов Групп	
Дизайнер	Заика Нина	
Дата	11.2022	

ВИЗУАЛИЗАЦИЯ ИНТЕРЬЕРА (кухня)

УСЛОВНЫЕ ОБОЗНАЧЕНИЯ

3D-визуализации интерьера
могут частично отличаться от
чертежей и даны для понимания
общей концепции.
Дизайн-проект реализуется по
рабочей документации

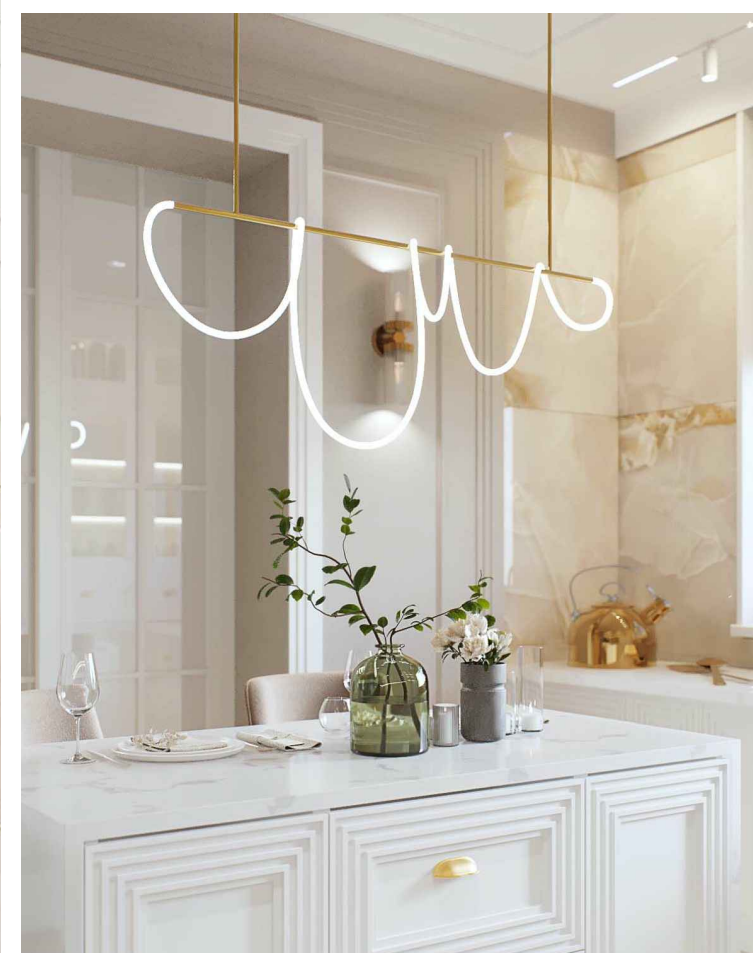

Дизайн проект интерьера
квартиры по адресу:
г. Москва ЖК "Headliner" 39/1

Стадия	Лист	Листов
РП	5	
Компания	Кодолов Групп	
Дизайнер	Заика Нина	
Дата	11.2022	



ВИЗУАЛИЗАЦИЯ ИНТЕРЬЕРА (кухня)

УСЛОВНЫЕ ОБОЗНАЧЕНИЯ

3D-визуализации интерьера
могут частично отличаться от
чертежей и даны для понимания
общей концепции.
Дизайн-проект реализуется по
рабочей документации



Дизайн проект интерьера
квартиры по адресу:
г. Москва ЖК "Headliner" 39/1

Стадия	Лист	Листов
РП	6	
Компания	Коголов Групп	
Дизайнер	Заика Нина	
Дата	11.2022	

ВИЗУАЛИЗАЦИЯ ИНТЕРЬЕРА (гостиная)

УСЛОВНЫЕ ОБОЗНАЧЕНИЯ

3D-визуализации интерьера
могут частично отличаться от
чертежей и даны для понимания
общей концепции.
Дизайн-проект реализуется по
рабочей документации

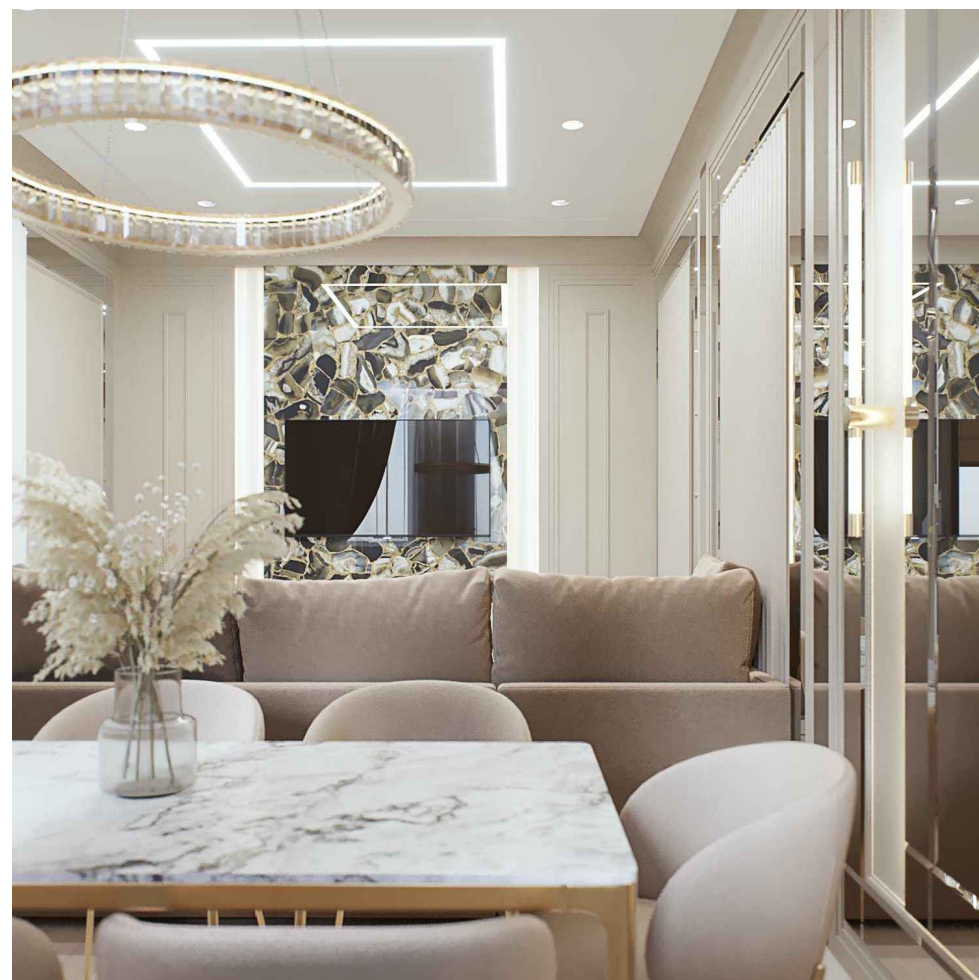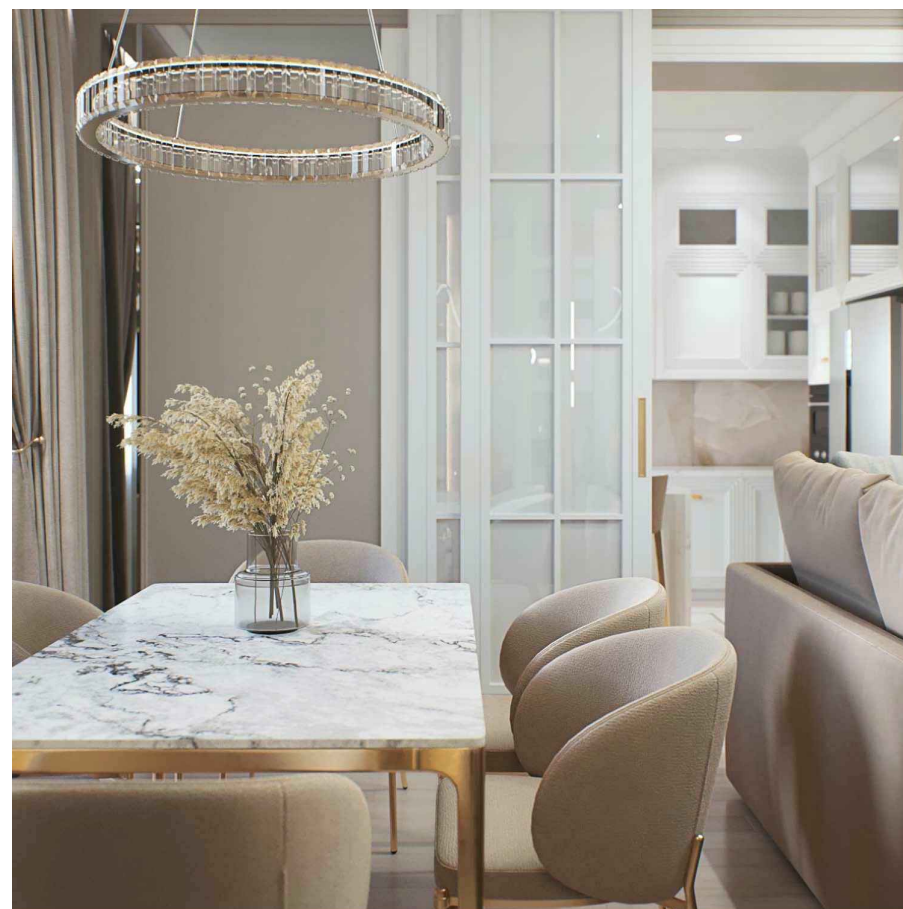

Дизайн проект интерьера
квартиры по адресу:
г. Москва ЖК "Headliner" 39/1

Стадия	Лист	Листов
РП	7	
Компания	Кодолов Групп	
Дизайнер	Заика Нина	
Дата	11.2022	

ВИЗУАЛИЗАЦИЯ ИНТЕРЬЕРА (гостиная)

УСЛОВНЫЕ ОБОЗНАЧЕНИЯ

3D-визуализации интерьера
могут частично отличаться от
чертежей и даны для понимания
общей концепции.
Дизайн-проект реализуется по
рабочей документации



Дизайн проект интерьера
квартиры по адресу:
г. Москва ЖК "Headliner" 39/1

Стадия	Лист	Листов
РП	8	
Компания	Кодолов Групп	
Дизайнер	Заика Нина	
Дата	11.2022	

ВИЗУАЛИЗАЦИЯ ИНТЕРЬЕРА (спальня)

УСЛОВНЫЕ ОБОЗНАЧЕНИЯ

3D-визуализации интерьера
могут частично отличаться от
чертежей и даны для понимания
общей концепции.
Дизайн-проект реализуется по
рабочей документации



Дизайн проект интерьера
квартиры по адресу:
г. Москва ЖК "Headliner" 39/1

Стадия	Лист	Листов
РП	9	
Компания	Коголов Групп	
Дизайнер	Заика Нина	
Дата	11.2022	



ВИЗУАЛИЗАЦИЯ ИНТЕРЬЕРА (спальня)

УСЛОВНЫЕ ОБОЗНАЧЕНИЯ

3D-визуализации интерьера могут частично отличаться от чертежей и даны для понимания общей концепции.
Дизайн-проект реализуется по рабочей документации






Дизайн проект интерьера
квартиры по адресу:
г. Москва ЖК "Headliner" 39/1

Стадия	Лист	Листов
РП	10	
Компания	Коголов Групп	
Дизайнер	Заика Нина	
Дата	11.2022	

ВИЗУАЛИЗАЦИЯ ИНТЕРЬЕРА (спальня)

УСЛОВНЫЕ ОБОЗНАЧЕНИЯ

3D-визуализации интерьера
могут частично отличаться от
чертежей и даны для понимания
общей концепции.
Дизайн-проект реализуется по
рабочей документации

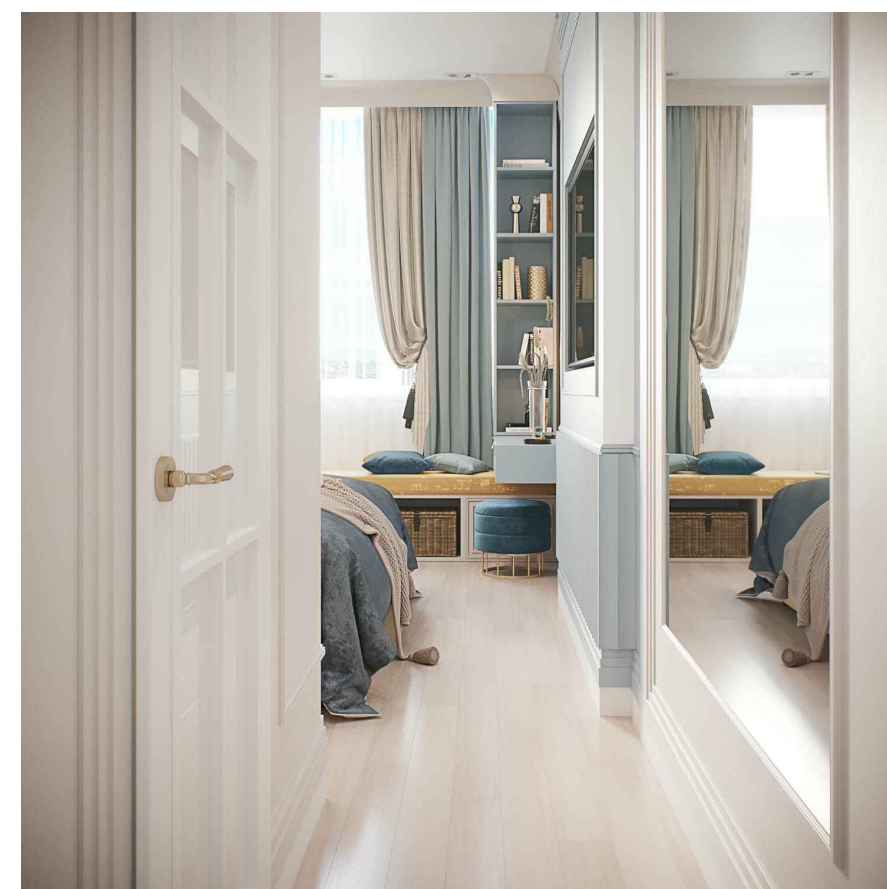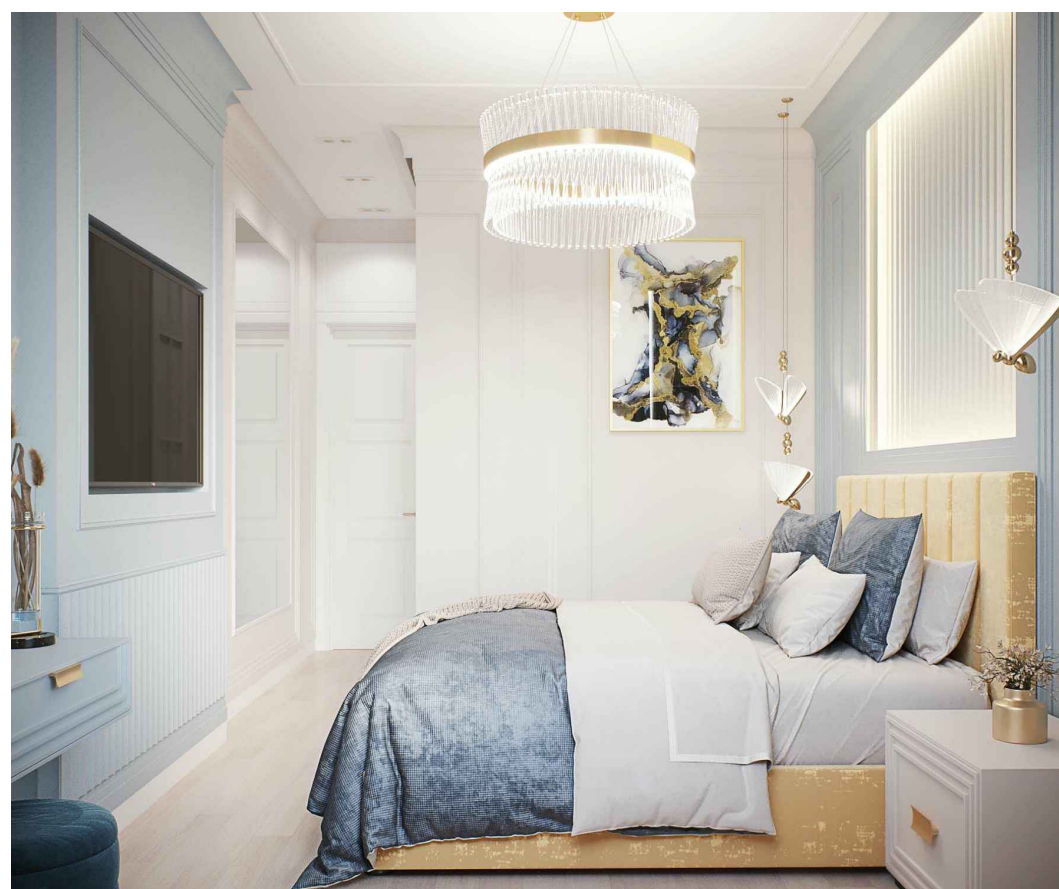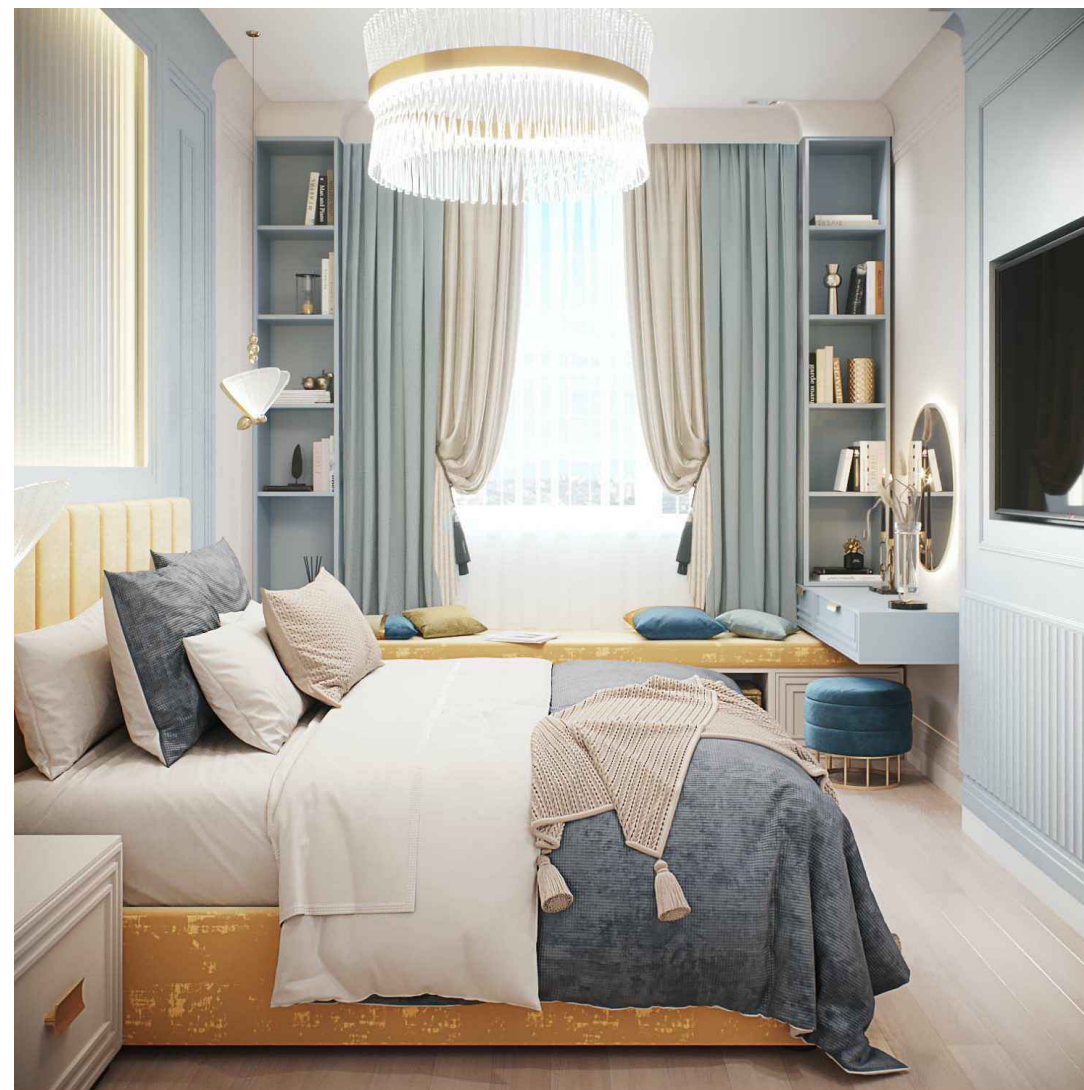


Дизайн проект интерьера
квартиры по адресу:
г. Москва ЖК "Headliner" 39/1

Стадия	Лист	Листов
РП	11	
Компания	Коголов Групп	
Дизайнер	Заика Нина	
Дата	11.2022	

ВИЗУАЛИЗАЦИЯ ИНТЕРЬЕРА
(гардероб)


УСЛОВНЫЕ ОБОЗНАЧЕНИЯ

3D-визуализации интерьера
могут частично отличаться от
чертежей и даны для понимания
общей концепции.
Дизайн-проект реализуется по
рабочей документации

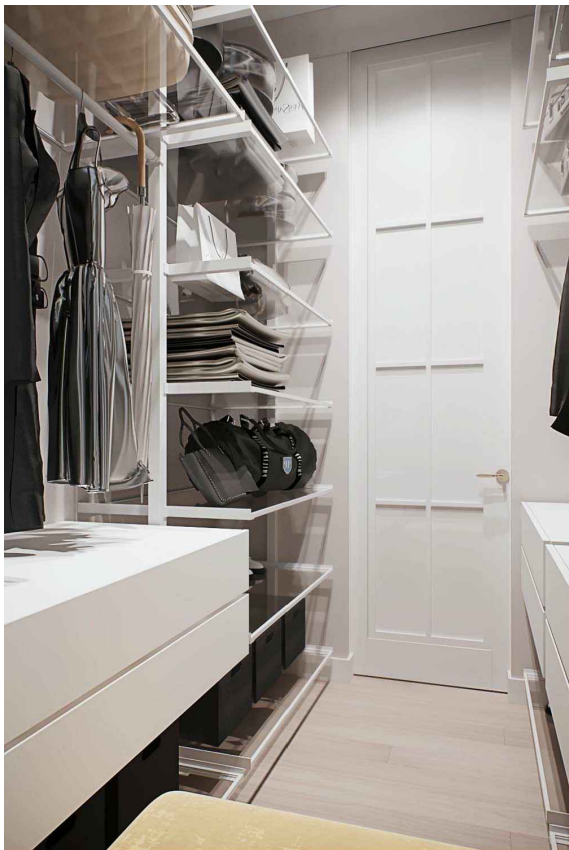

Дизайн проект интерьера
квартиры по адресу:
г. Москва ЖК "Headliner" 39/1

Стадия	Лист	Листов
РП	12	
Компания	Кодолов Групп	
Дизайнер	Заика Нина	
Дата	11.2022	

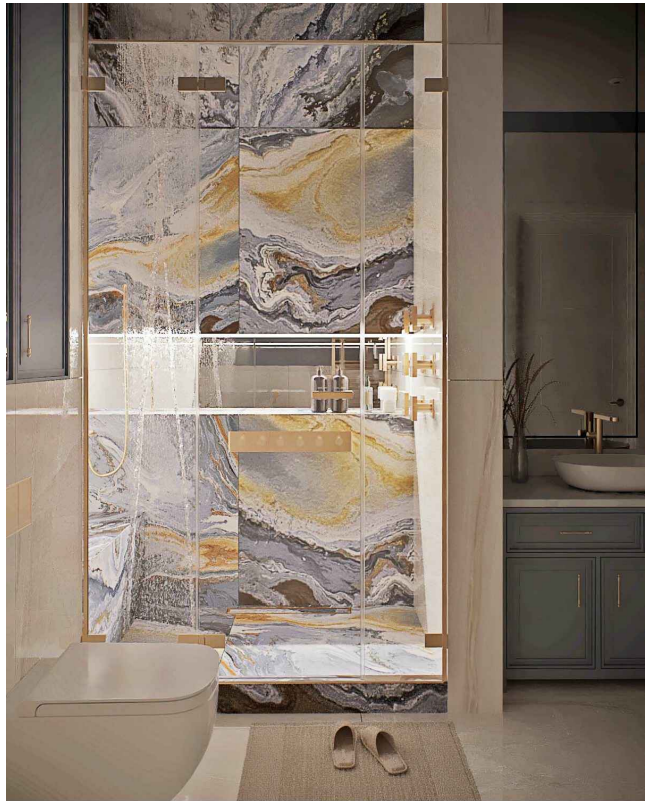

ВИЗУАЛИЗАЦИЯ ИНТЕРЬЕРА
(душевая)

УСЛОВНЫЕ ОБОЗНАЧЕНИЯ

3D-визуализации интерьера
могут частично отличаться от
чертежей и даны для понимания
общей концепции.
Дизайн-проект реализуется по
рабочей документации

Дизайн проект интерьера
квартиры по адресу:
г. Москва ЖК "Headliner" 39/1

Стадия	Лист	Листов
РП	13	
Компания	Коголов Групп	
Дизайнер	Заика Нина	
Дата	11.2022	



ВИЗУАЛИЗАЦИЯ ИНТЕРЬЕРА (душевая)



УСЛОВНЫЕ ОБОЗНАЧЕНИЯ

3D-визуализации интерьера
могут частично отличаться от
чертежей и даны для понимания
общей концепции.
Дизайн-проект реализуется по
рабочей документации

Дизайн проект интерьера
квартиры по адресу:
г. Москва ЖК "Headliner" 39/1

Стадия	Лист	Листов
РП	14	
Компания	Кодолов Групп	
Дизайнер	Заика Нина	
Дата	11.2022	

Все размеры уточнить на стадии
производственных работ

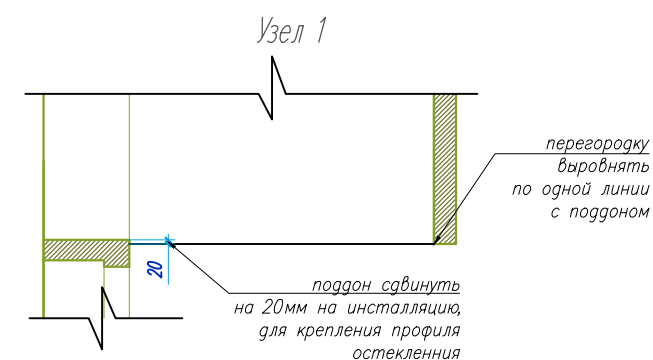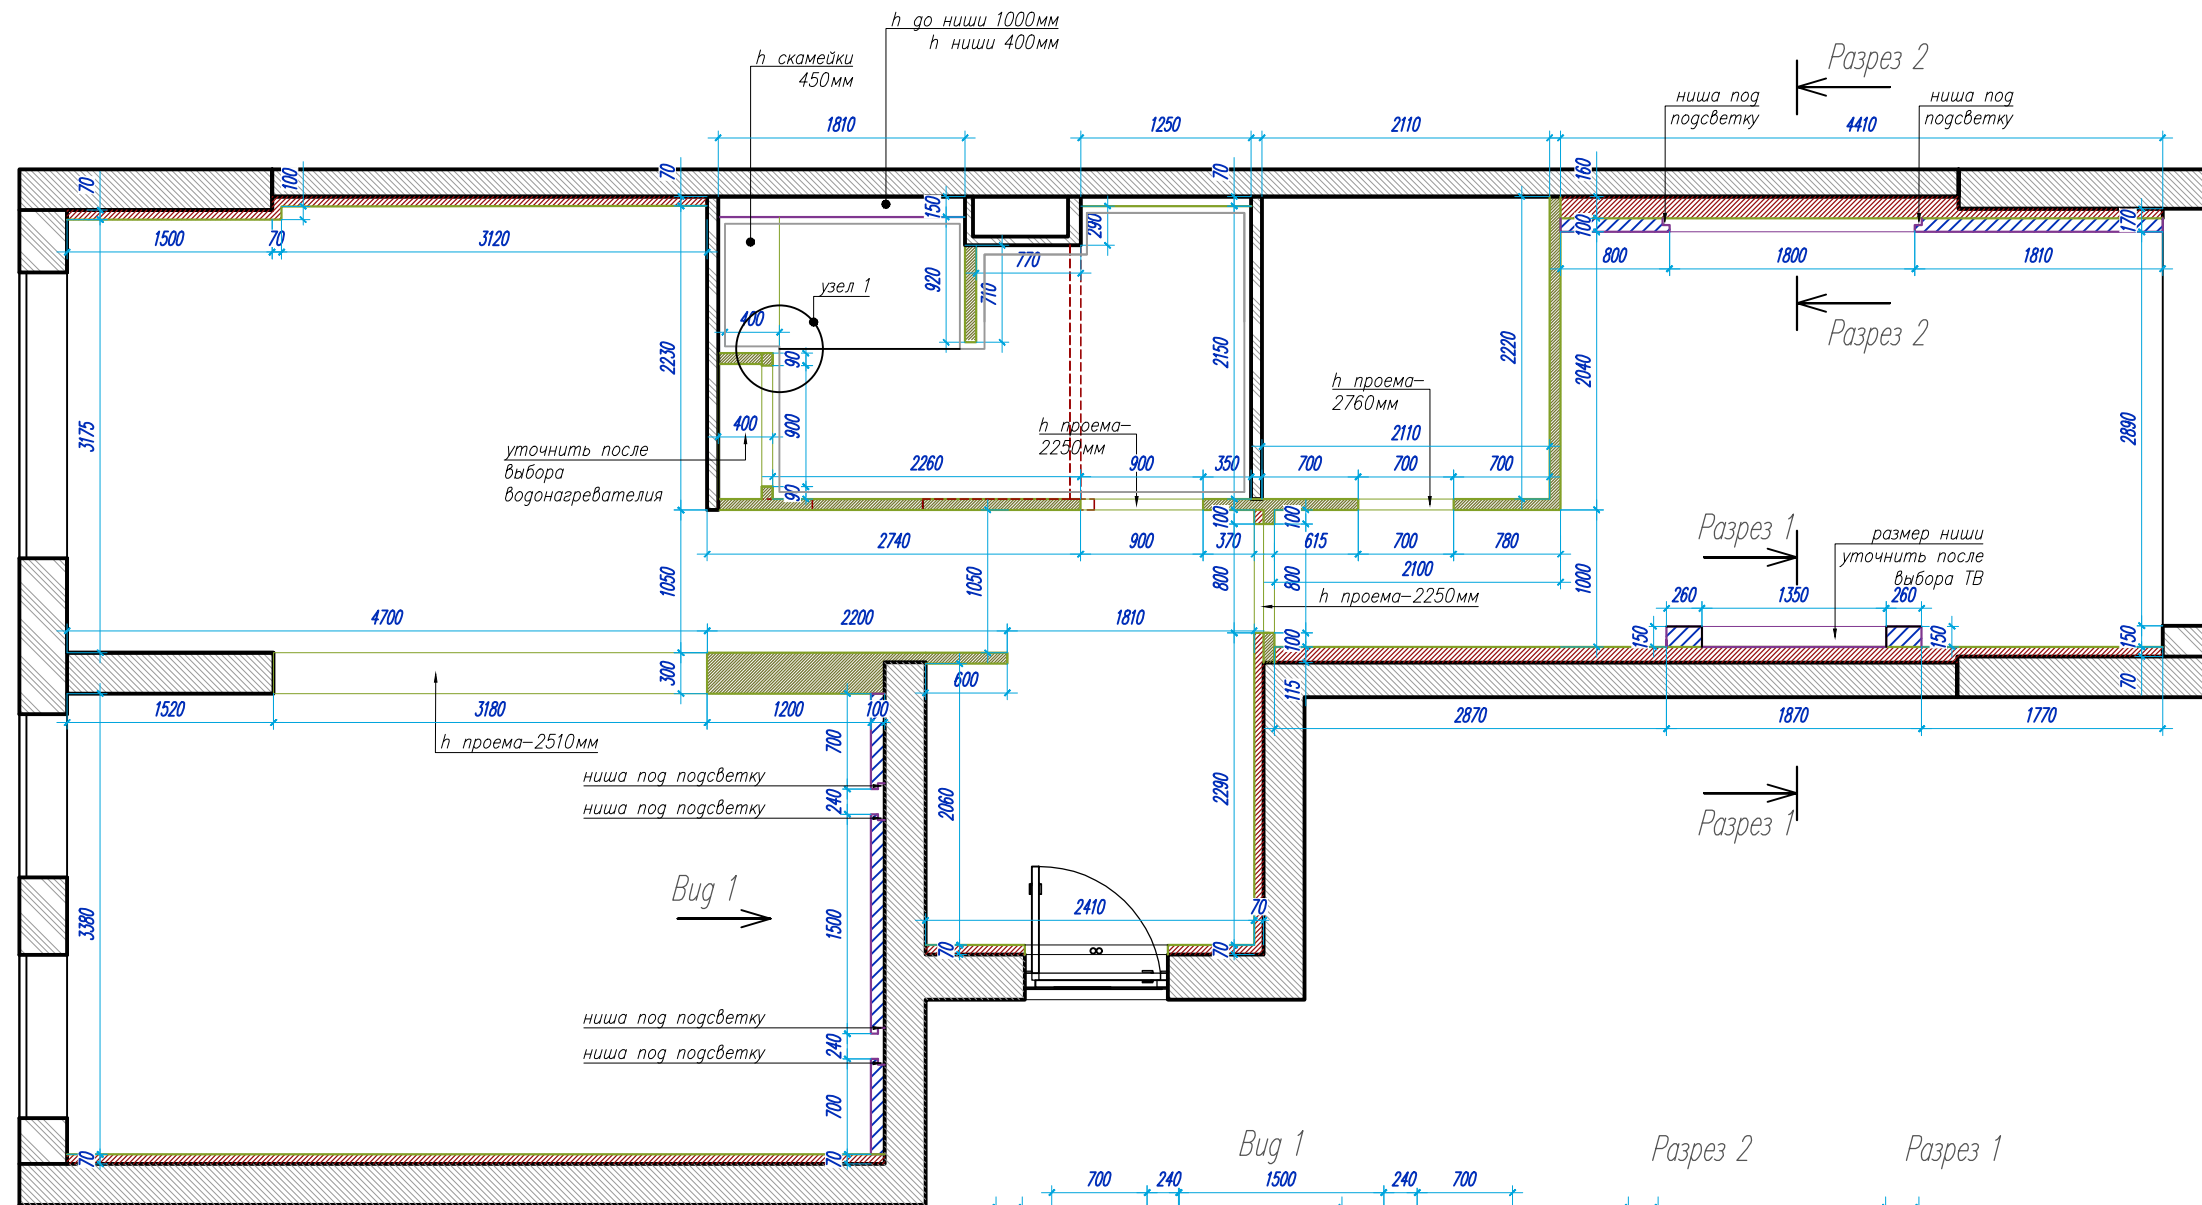

ПЛАН МОНТАЖА И ДЕМОНТАЖА


УСЛОВНЫЕ ОБОЗНАЧЕНИЯ

- Стены существующие бетон
- Стены существующие пеноблок
- Возводимые перегородки пазогребневых плит, 80 мм
- Звукоизоляция 70мм
- Возводимые перегородки гипсокартона
- Демонтаж стен
- Штукатурка 50мм

- Перед началом каких либо работ подрядчики должны сверить размеры на объекте.
- Все размеры уточняются после возведения и оштукатуривания стен. Поэтому после проведения отделочных материалов рекомендуем сверить с проектом и внести изменения, либо согласовать в порядке авторского надзора с проектировщиком.
- Проектировщики не несут ответственности за достоверность информации, предоставленной производителями и поставщиками, за сроки поставки, качество выполненных работ, сроки монтажа субподрядными организациями.

Дизайн проект интерьера квартиры по адресу: г. Москва ЖК "Headliner" 39/1		
Стадия	Лист	Листов
РП	15	
Компания	Коголов Групп	
Дизайнер	Заика Нина	
Дата	11.2022	

Примечание:
Все размеры и отметки, расход всех материалов, все площади уточняются по месту. На каждом объекте возможны увеличения или уменьшения размеров в зависимости от технических допусков, кривизны, расхождения уровней стен и потолков.


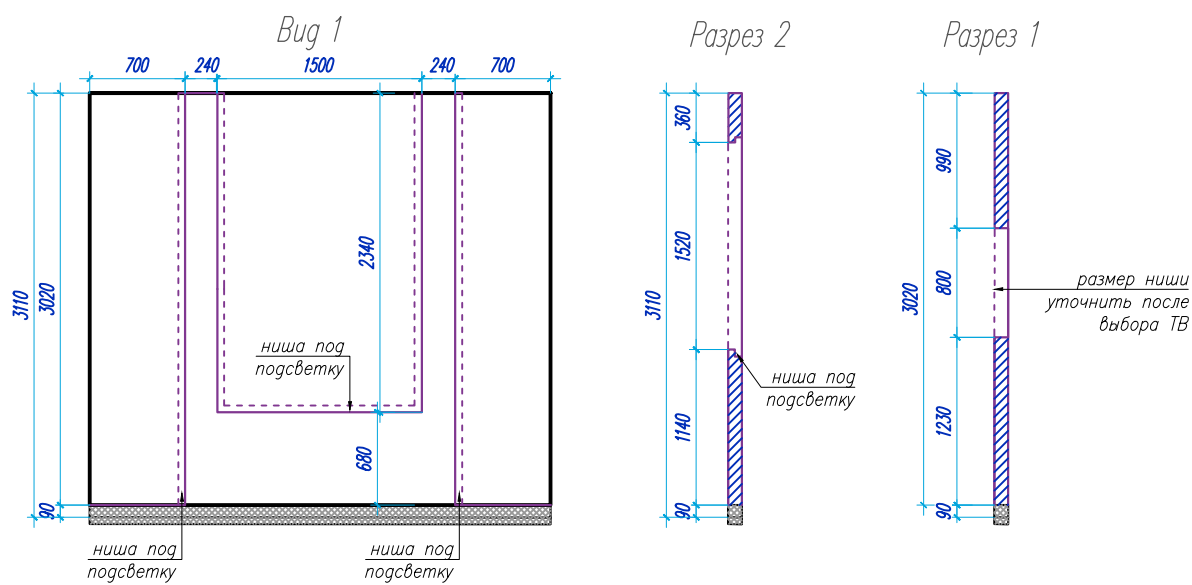


Все размеры уточнить на стадии
производственных работ

ПЛАН ЗАПОЛНЕНИЯ
ДВЕРНЫХ ПРОЕМОВ

УСЛОВНЫЕ ОБОЗНАЧЕНИЯ

- Стены существующие бетон
- Стены существующие пеноблок
- Возводимые перегородки пазогребневых плит, 80 мм
- Звукоизоляция 70мм
- Возводимые перегородки гипсокартона

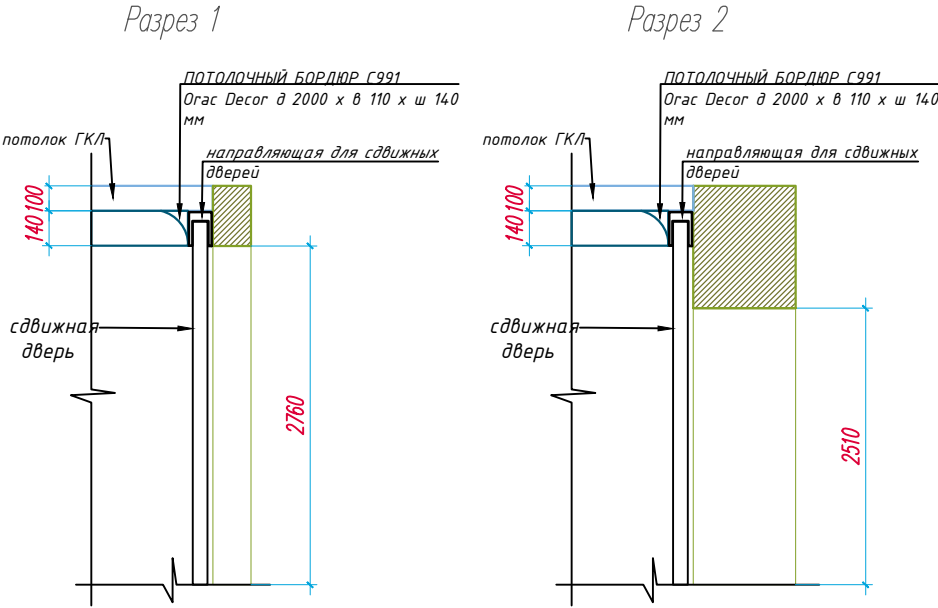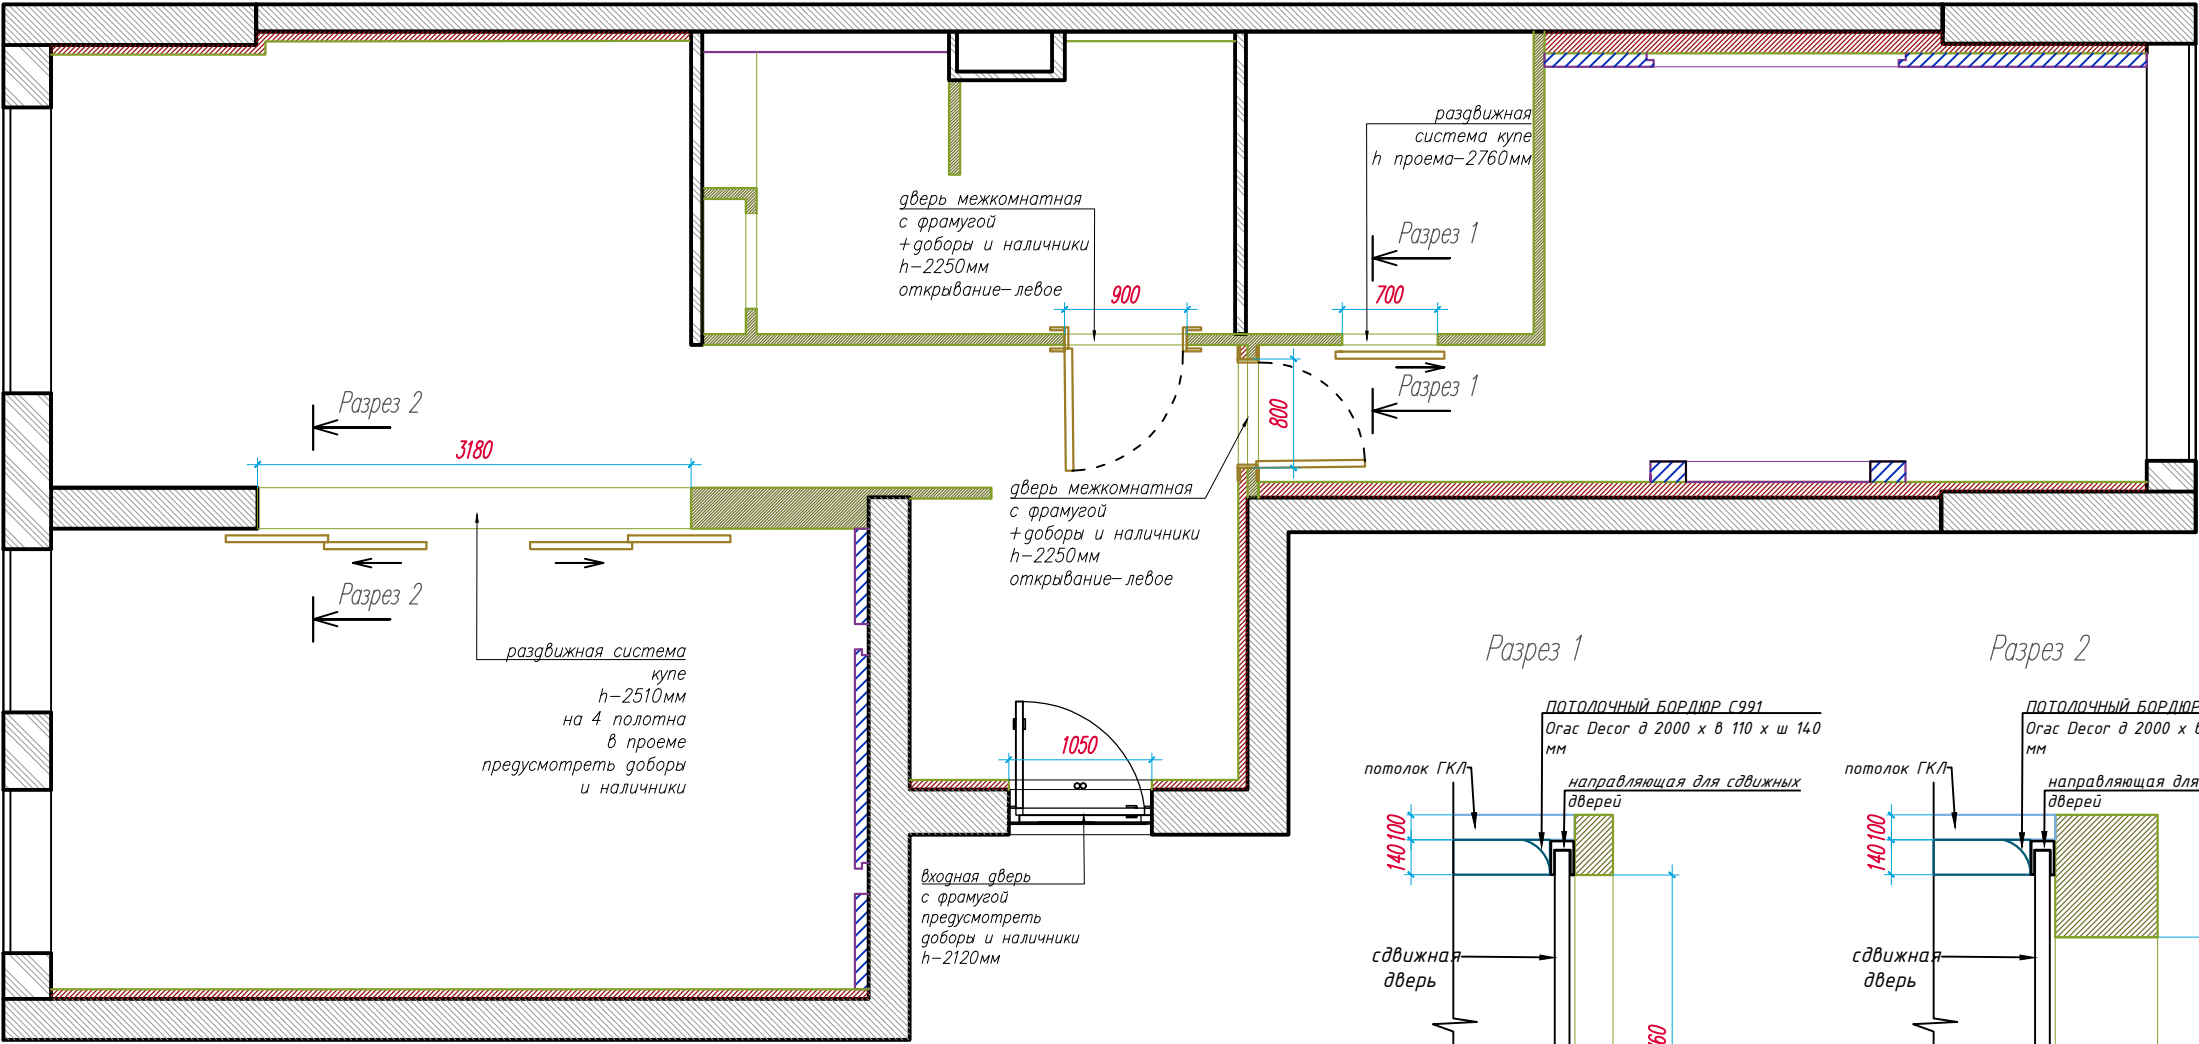

Примечание:
Высоты даны от чистого пола


Все размеры и отметки, расход всех материалов, все площади уточняются по месту. На каждом объекте возможны увеличения или уменьшения размеров в зависимости от технических допусков, кривизны, расхождения уровней стен и потолков.

1. Перед началом каких либо работ подрядчики должны сверить размеры на объекте.
2. Все размеры уточняются после возведения и оштукатуривания стен. Поэтому после проведения отделочных материалов рекомендуем сверить с проектом и внести изменения, либо согласовать в порядке авторского надзора с проектировщиком.
3. Проектировщики не несут ответственности за достоверность информации, предоставленной производителями и поставщиками, за сроки поставки, качество выполненных работ, сроки монтажа субподрядными организациями.

Дизайн проект интерьера
квартиры по адресу:
г. Москва ЖК "Headliner" 39/1

Стадия	Лист	Листов
РП	16	
Компания	Коголов Групп	
Дизайнер	Заика Нина	
Дата	11.2022	

Все размеры уточнить на стадии
производственных работ

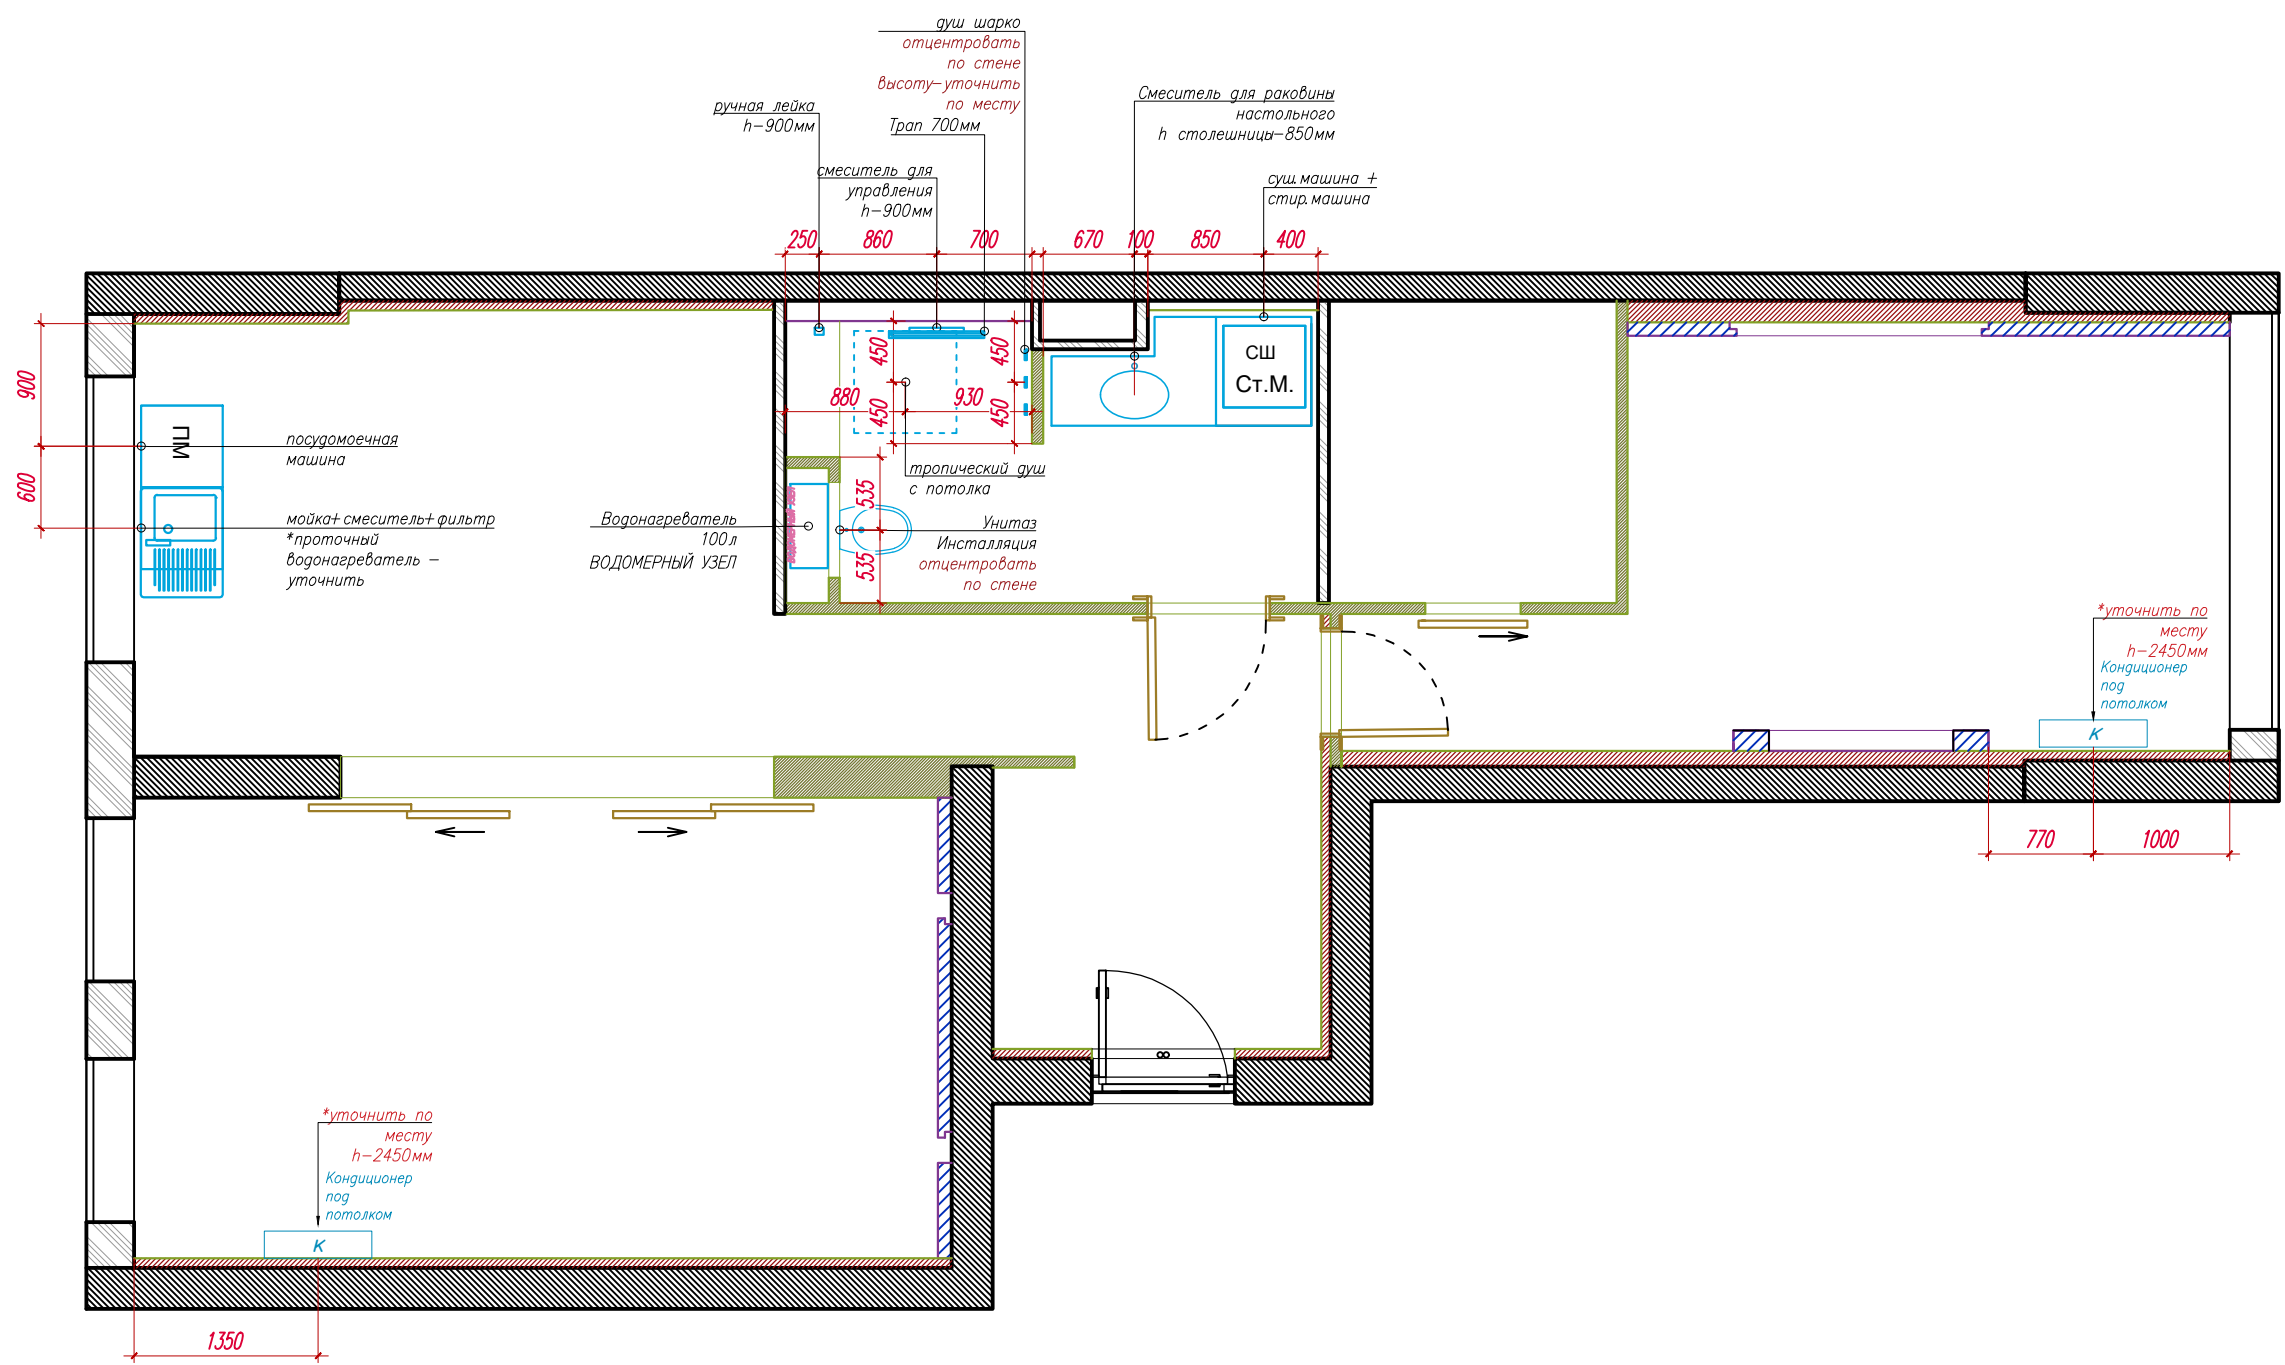

Примечание:
Все размеры и отметки, расход всех материалов, все
площади уточняются по месту. На каждом объекте возможны
увеличения или уменьшения размеров в зависимости от
технических допусков, кривизны, расхождения уровней стен и
потолков.

ПЛАН ПРИВЯЗКИ
САНТЕХНИЧЕСКОГО
ОБОРУДОВАНИЯ И
КОНДИЦИОНЕРОВ

УСЛОВНЫЕ ОБОЗНАЧЕНИЯ

- Стены существующие бетон
- Стены существующие пеноблок
- Возводимые перегородки пазогребневых плит, 80 мм
- Звукоизоляция 70мм
- Возводимые перегородки гипсокартона

- Все высоты указаны от чистого пола.
- Необходимые выводы под стиральную машину+сушку и посудомойку уточнить после выбора модели и получения технических характеристик
- Расположение сантехнического оборудования, а так же привязки по высотам, уточнить после заказа оборудования. В случае отсутствия оборудования на объекте, запросить все схемы подключения.
- Перед началом каких-либо работ подрядчик должен сверить размеры на объекте.
- Проектировщик не несет ответственности за достоверность информации, предоставленной производителями и поставщиками, за сроки поставки, качество выполненных работ, сроки монтажа субподрядными организациями.
- Размеры стен даны без учета штукатурного слоя и отделочных материалов. Поэтому после проведения отделочных работ рекомендуется сверить фактические размеры с проектом и внести изменения, либо согласовать в порядке авторского надзора с проектировщиком.

Дизайн проект интерьера
квартиры по адресу:
г. Москва ЖК "Headliner" 39/1

Стадия	Лист	Листов
РП	17	
Компания	Коголов Групп	
Дизайнер	Заика Нина	
Дата	11.2022	

Все размеры уточнить на стадии
производственных работ

ПЛАН С РАССТАНОВКОЙ
МЕБЕЛИ

УСЛОВНЫЕ ОБОЗНАЧЕНИЯ


- Стены существующие бетон
- Стены существующие пеноблок
- Возводимые перегородки из пазогребневых плит 80мм
- Звукоизоляция 70мм
- Штукатурка 50мм

ЭКСПЛИКАЦИЯ ПОМЕЩЕНИЙ

№	ПОМЕЩЕНИЕ	ПЛОЩАДЬ
1	Прихожая	5,2 кв.м.
2	Холл	3,4 кв.м.
3	Душевая	8,3 кв.м.
4	Кухня	14,6 кв.м.
5	Гостиная	21 кв.м.
6	Гардероб	4,4 кв.м.
7	Спальня	15,6 кв.м.
8		
9		
10		
Итого		72,5 кв.м.

Дизайн проект интерьера
квартиры по адресу:
г. Москва ЖК "Headliner" 39/1

Стадия	Лист	Листов
РП	18	
Компания	Коголов Групп	
Дизайнер	Заика Нина	
Дата	11.2022	

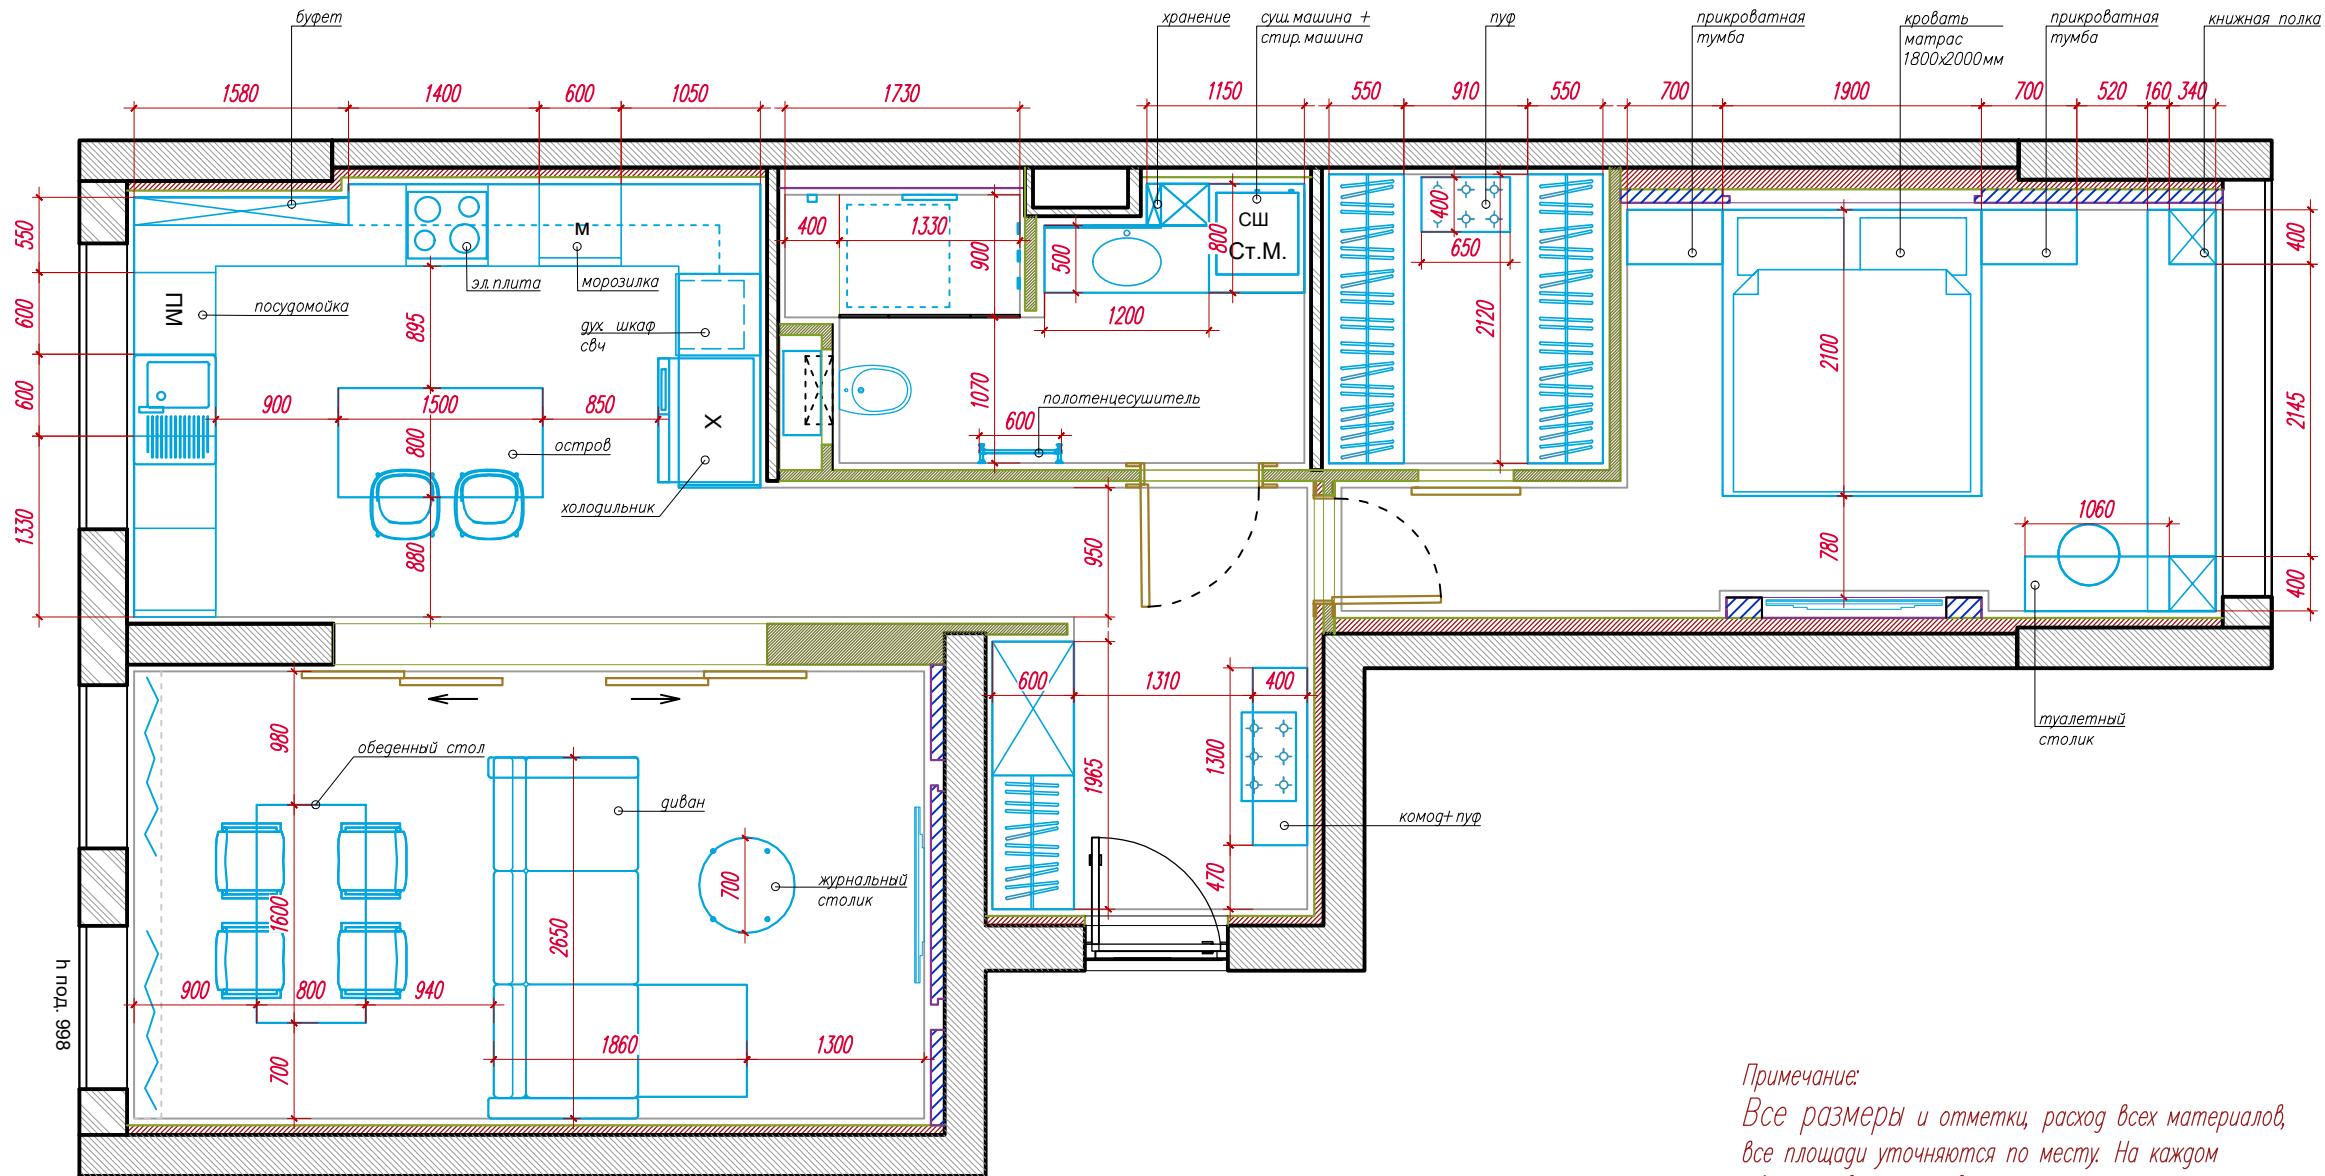

Примечание:
Все размеры и отметки, расход всех материалов,
все площади уточняются по месту. На каждом
объекте возможны увеличения или уменьшения
размеров в зависимости от технических допусков,
кривизны, расхождения уровней стен и потолков.

Все размеры уточнить на стадии
производственных работ

ПЛАН ПОТОЛКА С
УКАЗАНИЕМ ПЛОЩАДЕЙ

УСЛОВНЫЕ ОБОЗНАЧЕНИЯ



Потолок ГКЛ
цвет белый



ПОТОЛОЧНЫЙ БОРДЮР С991
Orac Decor
д 2000 х в 110 х ш 140 мм
в цвет стены



Молдинг PX116 Orac Decor
д 2000 х в 31 х ш 10 мм




Canyon Purple Natural
керамогранит LAND
Porcelanico 1000*1000мм

Примечания:


1. За 0 потолка принимается выровненный потолок.
2. Размеры стен даны без учета штукатурного слоя и отделочных материалов.
3. Перед началом каких либо работ подрядчики должны сверить размеры на объекте. Поэтому после проведения отделочных работ рекомендуется сверить с проектом и внести изменения в порядке авторского надзора с проектировщиком.
4. Проектировщик не несет ответственности за достоверность информации, предоставленной производителями и поставщиками, за сроки поставки, качество выполненных работ, сроки монтажа субподрядными организациями.
5. Все потолки будут уточняться по факту выполнения технической документации от поставщиков вентиляционного и кондиционерного оборудования и т.п.

Дизайн проект интерьера
квартиры по адресу:
г. Москва ЖК "Headliner" 39/1

Стадия	Лист	Листов
РП	19	
Компания	Коголов Групп	
Дизайнер	Заика Нина	
Дата	10.2022	

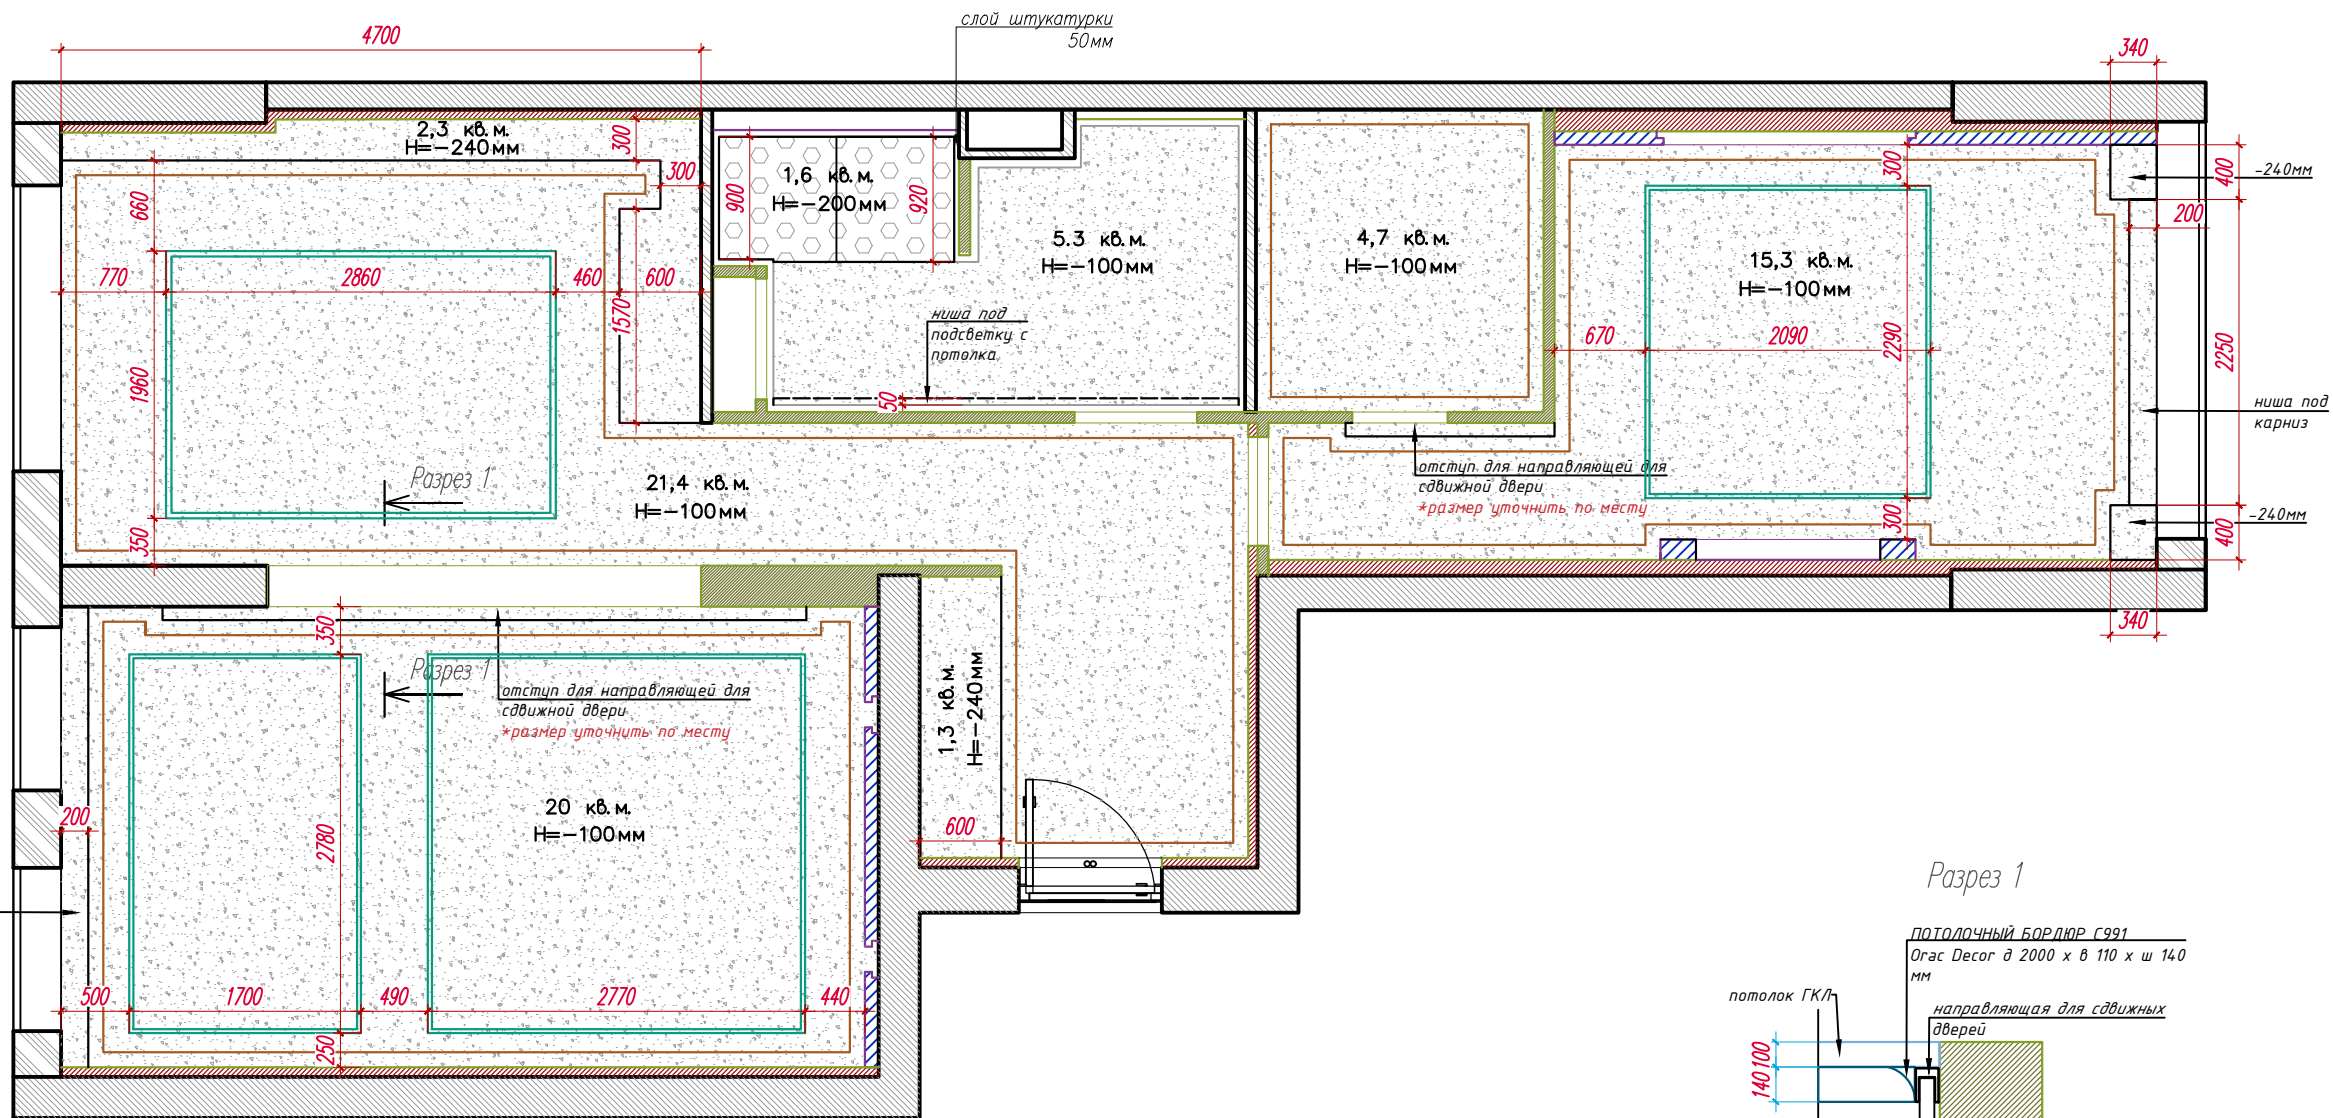

Разрез 1

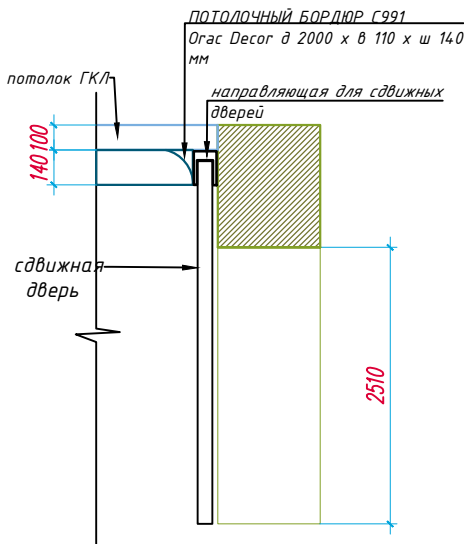


Примечание:
Все размеры и отметки, расход всех материалов, все
площади уточняются по месту. На каждом объекте возможны
увеличения или уменьшения размеров в зависимости от
технических допусков, кривизны, расхождения уровней стен и
потолков.

Все размеры уточнить на стадии
производственных работ

План размещения
осветительных
приборов

УСЛОВНЫЕ ОБОЗНАЧЕНИЯ

- Светильник
потолочный Встроенный
- Светильник настенный
Бра
- Вывод
- LED подсветка
- Светильник
потолочный накладной
- Потолочный световой
профиль
- Светильник
потолочный Подвесной
- Встроенная трековая
система

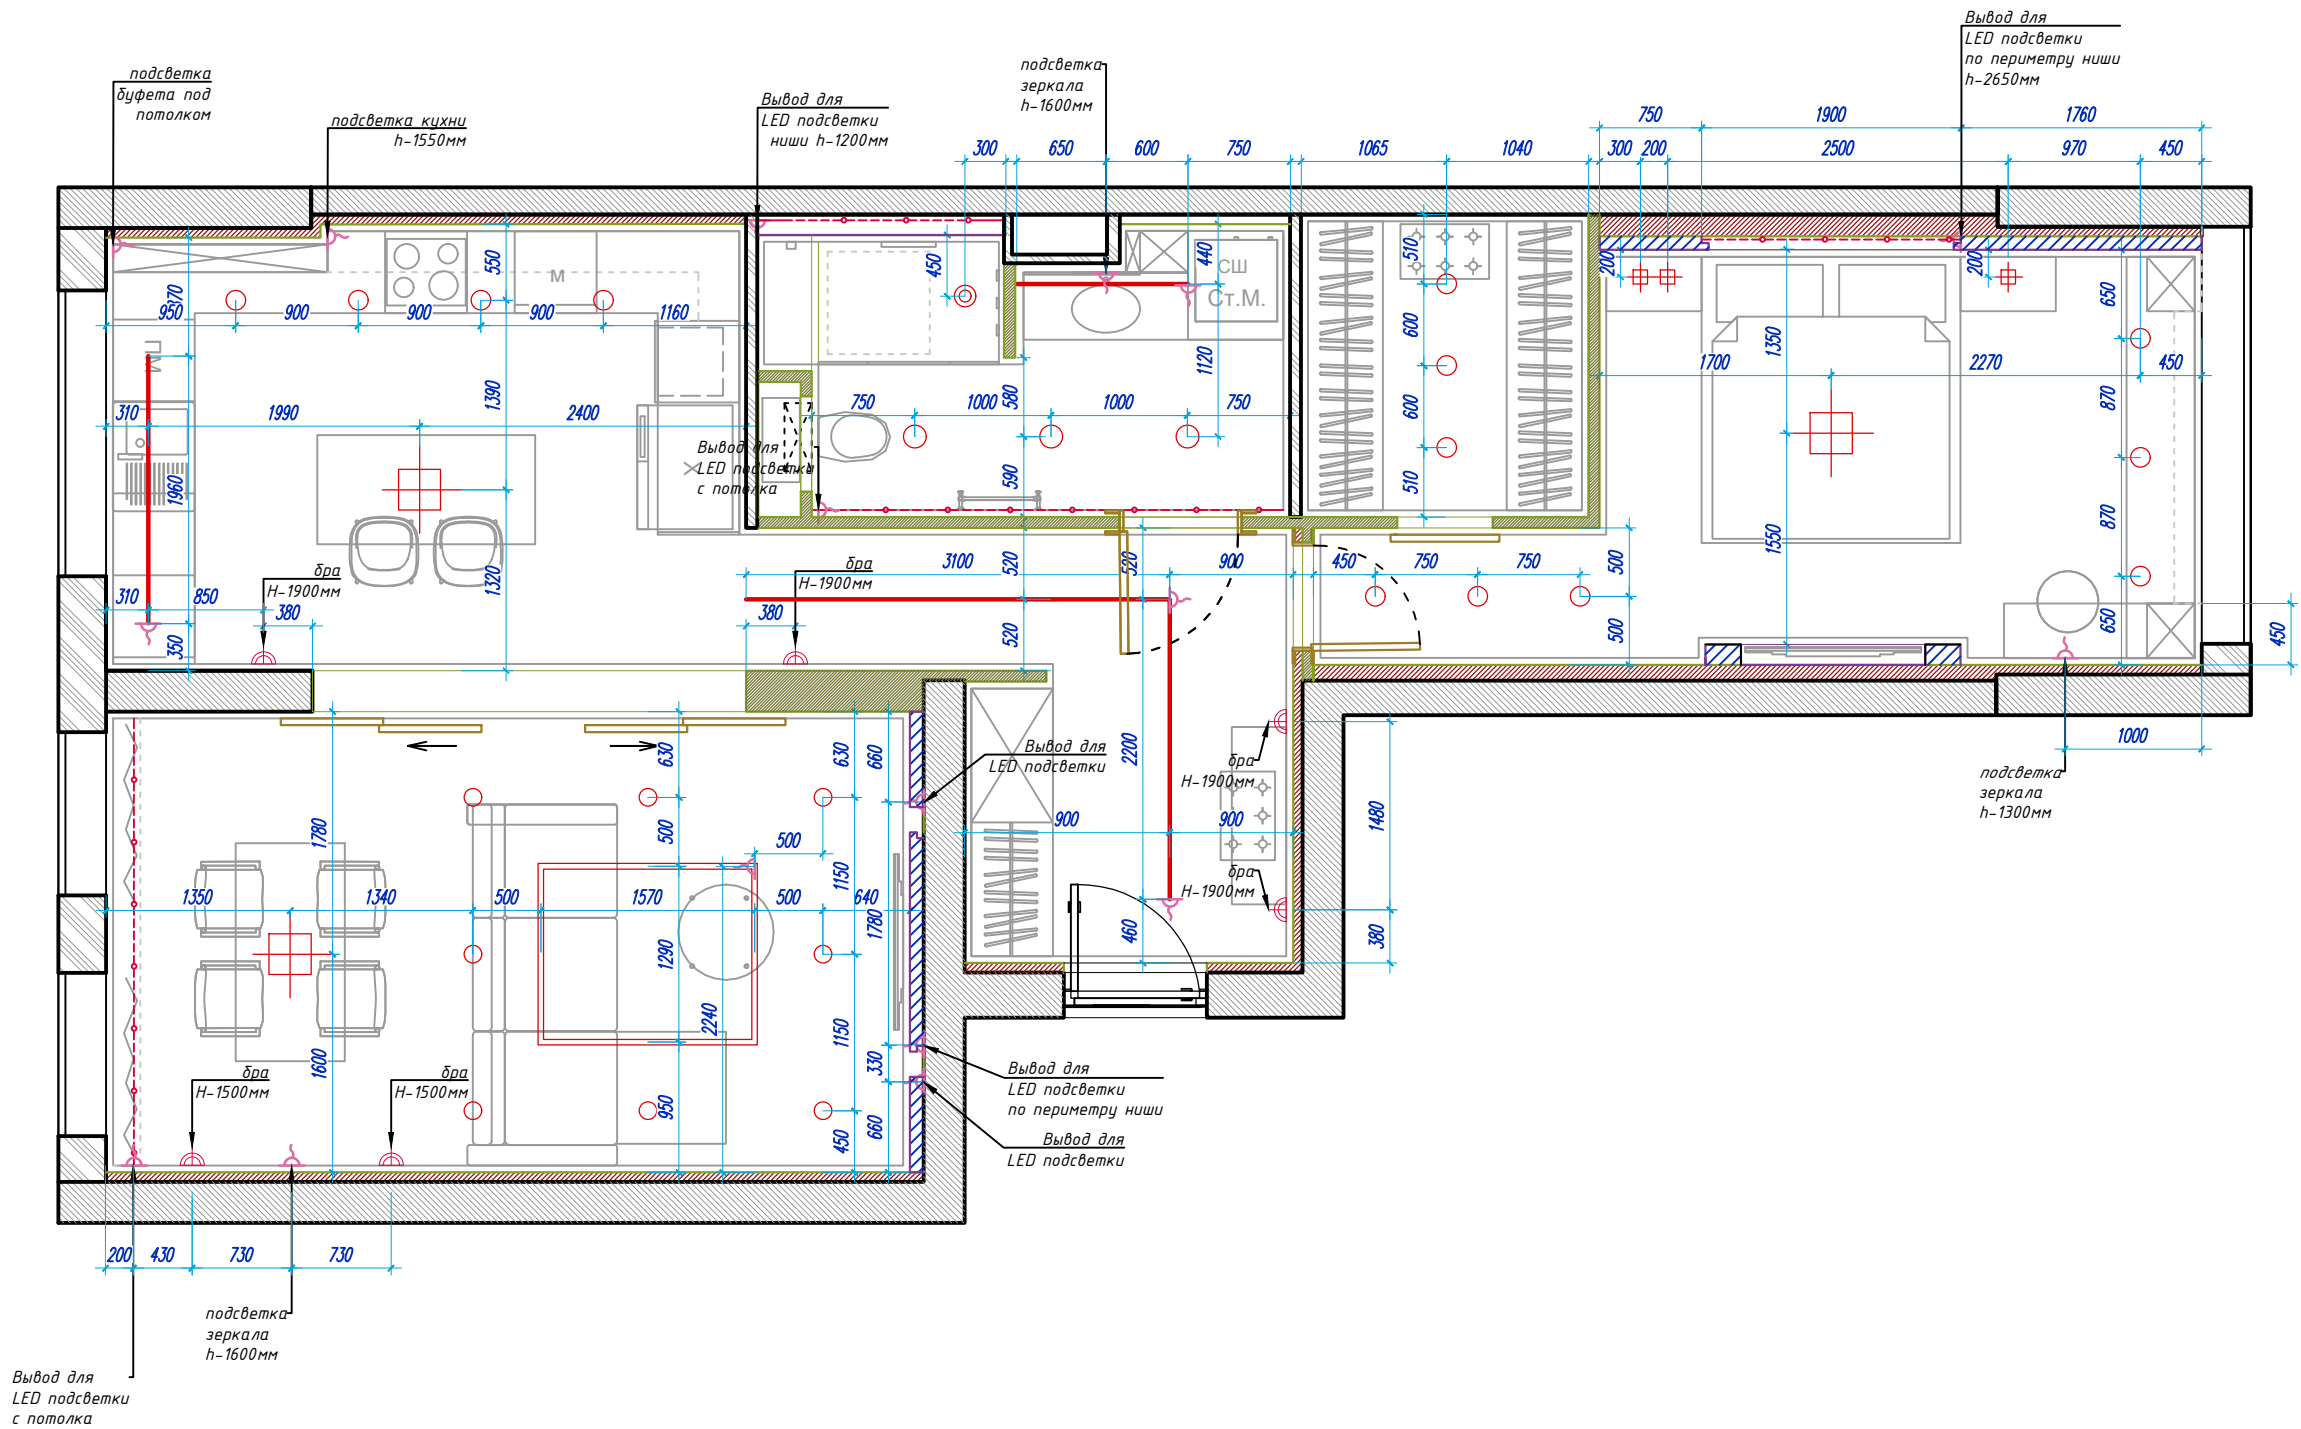

1. Монтаж осветительного оборудования производить в соответствии с паспортом изделия.
2. Размеры указаны до оси электроустановочного изделия
3. Размеры стен даны без учета штукатурного слоя и отделочных материалов.
4. Все привязки даны в мм.
6. В целях дальнейшего обслуживания или замены рекомендуется располагать трансформаторы светодиодной ленты в доступном месте.
7. Не рекомендуется располагать в одном помещении одновременно свет холодного и теплого оттенков.
8. Предусмотреть запас провода под осветительные приборы 600мм

Дизайн проект интерьера
квартиры по адресу:
г. Москва ЖК "Headliner" 39/1

Стадия	Лист	Листов
РП	20	
Компания	Коголов Групп	
Дизайнер	Заика Нина	
Дата	10.2022	

Примечание:
Все размеры и отметки, расход всех материалов, все площади уточняются по месту. На каждом объекте возможны увеличения или уменьшения размеров в зависимости от технических допусков, кривизны, расхождения уровней стен и потолков.

Все размеры уточнить на стадии
производственных работ

План выключателей с
привязкой к группам
света


УСЛОВНЫЕ ОБОЗНАЧЕНИЯ

- Светильник
потолочный Встроенный
- Светильник настенный
- Бра
- Вывод
- LED подсветка
- Светильник
потолочный накладной
- Потолочный световой
профиль
- Светильник
потолочный Подвесной
- Встроенная трековая
система
- Вытяжка
- Выключатель одноклавишный
H-1000мм
- Выключатель двухклавишный
H-1000мм
- Выключатель проходной
- Выключатель перекрестный

- Монтаж осветительного оборудования
производить в соответствии с паспортом
изделия.
- Размеры указаны до оси
электроустановочного изделия
- Размеры стен даны без учета штукатурного
слоя и отделочных материалов.
- Все привязки даны в мм.
- В целях дальнейшего обслуживания или
замены рекомендуется располагать
трансформаторы светодиодной ленты в
доступном месте.
- Не рекомендуется располагать в одном
помещении одновременно свет холодного и
теплого оттенков.
- Предусмотреть запас провода под
осветительные приборы 600мм


Дизайн проект интерьера
квартиры по адресу:
г. Москва ЖК "Headliner" 39/1

Стадия	Лист	Листов
РП	21	
Компания	Коголов Групп	
Дизайнер	Заика Нина	
Дата	10.2022	

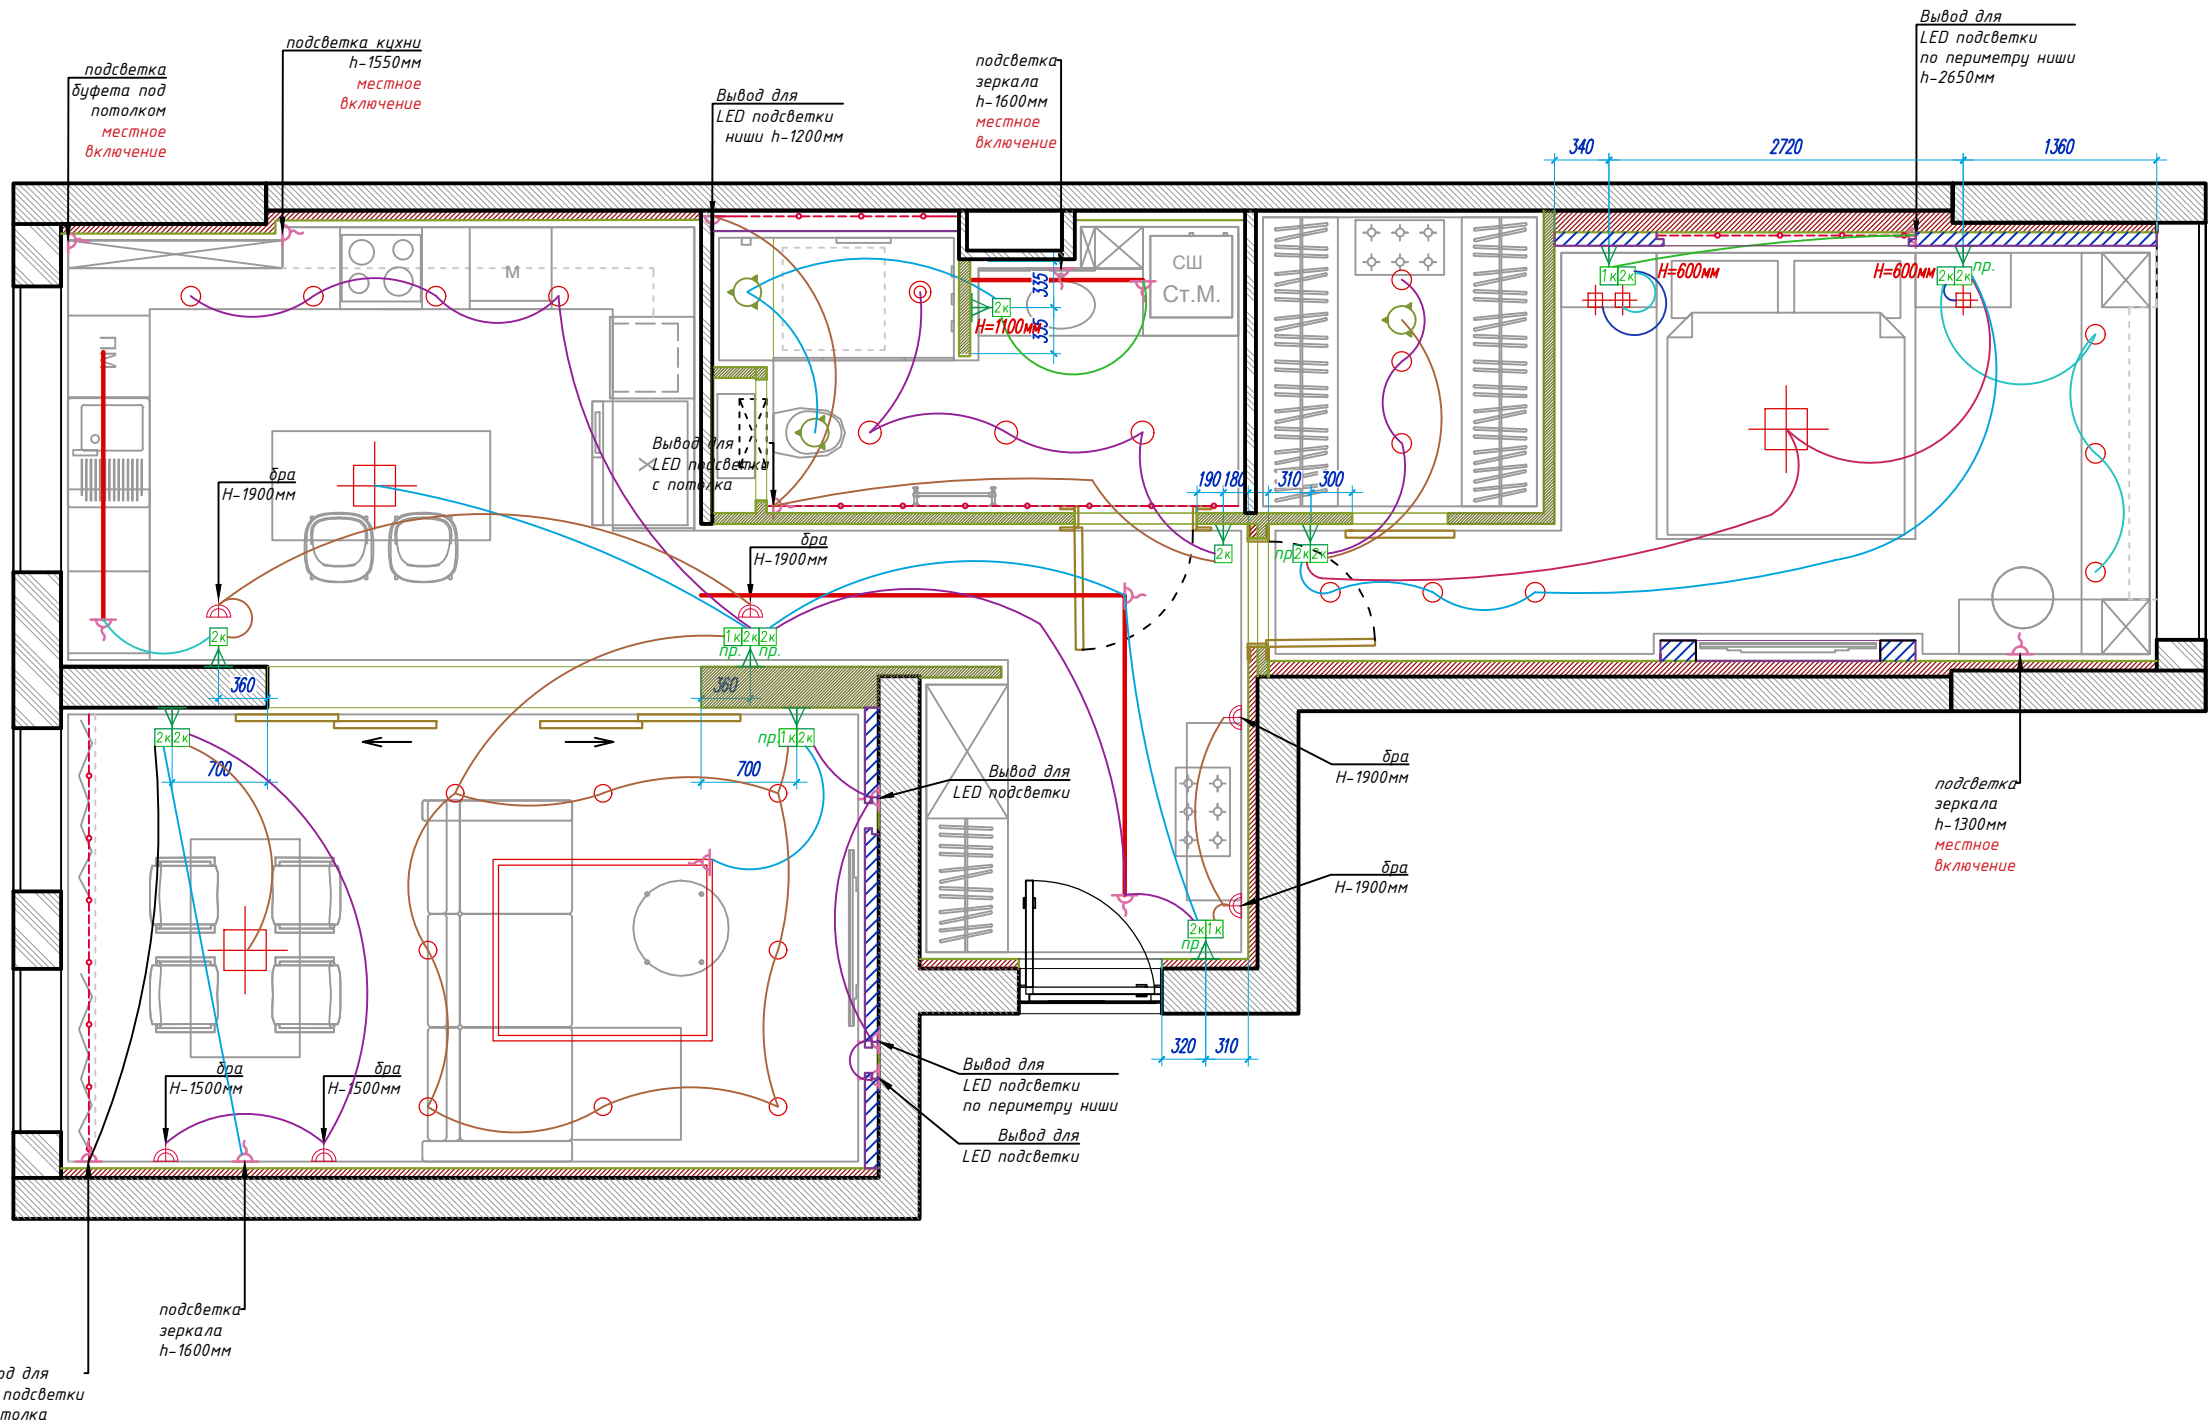

Примечание:
Все размеры и отметки, расход всех материалов, все
площади уточняются по месту. На каждом объекте возможны
увеличения или уменьшения размеров в зависимости от
технических допусков, кривизны, расхождения уровней стен и
потолков.

Все размеры уточнить на стадии
производственных работ

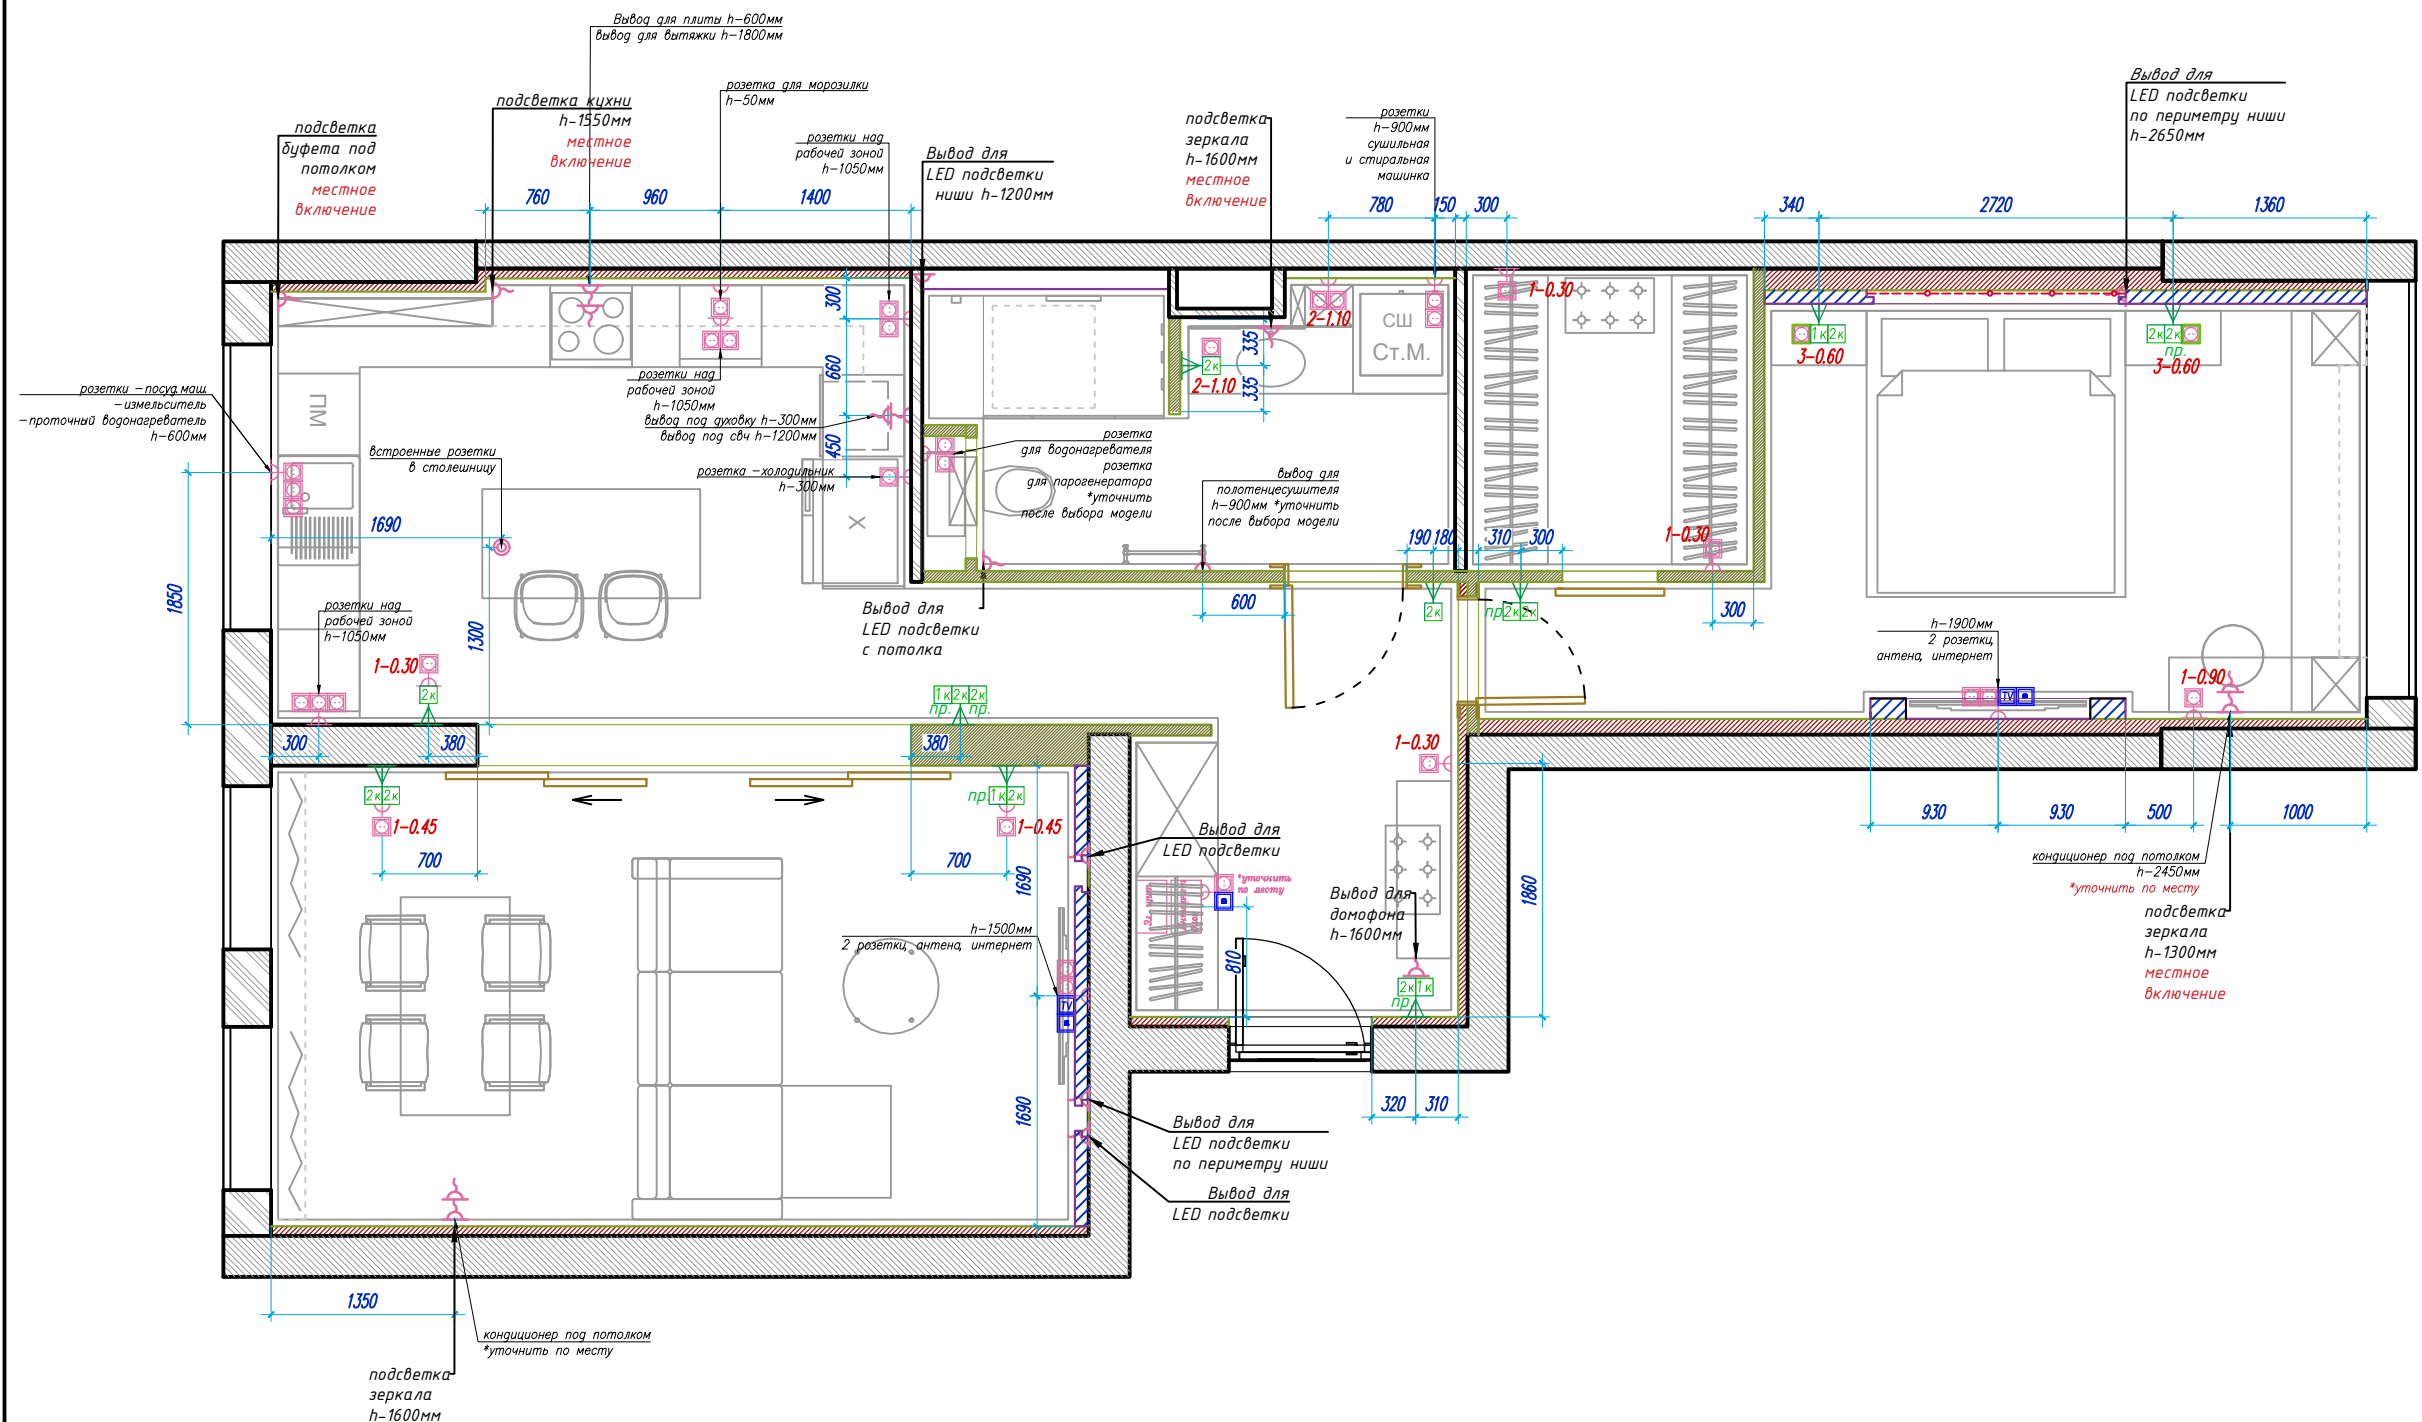

Примечание:
Все размеры и отметки, расход всех материалов, все
площади уточняются по месту. На каждом объекте возможны
увеличения или уменьшения размеров в зависимости от
технических допусков, кривизны, расхождения уровней стен и
потолков.

План размещения
розеток

УСЛОВНЫЕ ОБОЗНАЧЕНИЯ


- 1-1000mm Выключатель одноклавишный
- 2-1000mm Выключатель двухклавишный
- перекр. Выключатель проходной
- перекр. Выключатель перекрестный
- Электророзетка 220В
- Сетевой кабель LAN 220В
- Розетка телевизионная
- Вывод провода 220В
- Электророзетка + USB выход 220В

1. Монтаж осветительного оборудования производить в соответствии с паспортом изделия.
2. Размеры указаны до оси электроустановочного изделия.
3. Размеры стен даны без учета штукатурного слоя и отделочных материалов.
4. Перед началом каких либо работ подрядчики должны сверить размеры на объекте. Поэтому после проведения отделочных работ рекомендуется сверить с проектом и внести изменения в порядке авторского надзора с проектировщиком.
5. Уточнить включение настенных светильников.
6. Разводка в кухонном оборудовании уточняется после выбора бытовой техники и утверждения рабочего чертежа в кухонном салоне.
7. Все высоты даны от чистого пола.
8. Уточнить у подрядчика необходимые выводы для установки WiFi.

Дизайн проект интерьера
квартиры по адресу:
г. Москва ЖК "Headliner" 39/1

Стадия	Лист	Листов
РП	22	
Компания	Коголов Групп	
Дизайнер	Заика Нина	
Дата	10.2022	

Все размеры уточнить на стадии
производственных работ

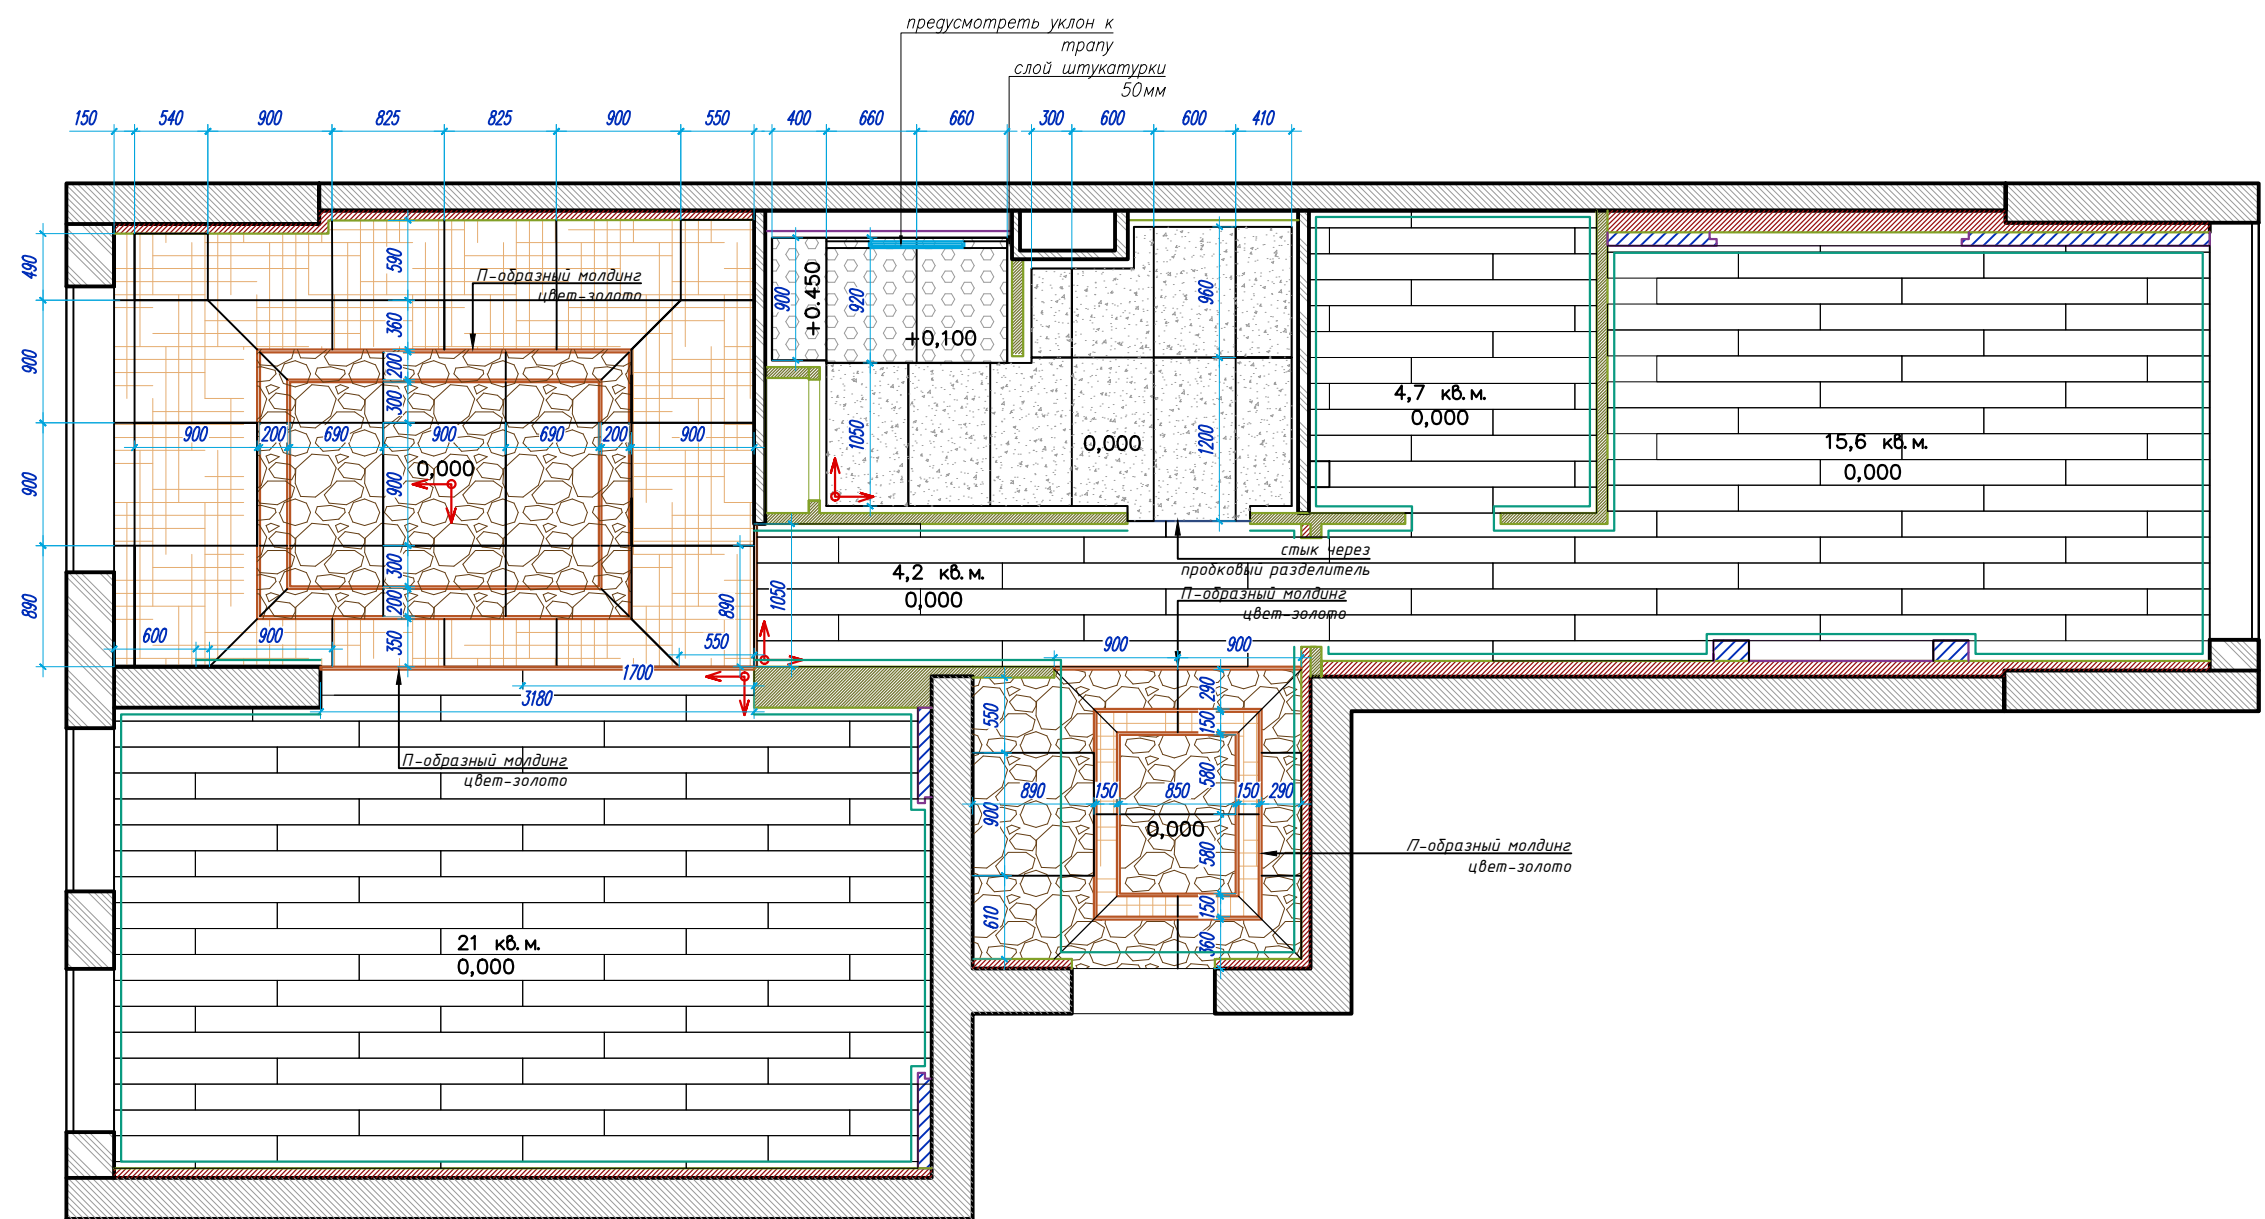

ПЛАН РАСКЛАДКИ МАТЕРИАЛОВ ПОЛА

УСЛОВНЫЕ ОБОЗНАЧЕНИЯ

- 201221P Selene Light Pol.
керамогранит Dune 600x1200мм
- Canyon Purple Natural
керамогранит LAND Porcelanico
1000x1000мм
- 188205 Selene Cappuccino Pul.
керамогранит Dune 900x900мм
- 187971 Selene Light Pul.
керамогранит Dune 900x900мм
- Инженерная Доска греб
Мерлетто (brushed) 110511
190x1800мм
- ПЛИНТУС SX163 SQUARE
Orac Decor g 2000 x в 101 x
ш 13 мм

Начало раскладки

Примечания:

- Все размеры указаны от чистого пола до середины блока (центра блока).
- Перед началом каких-либо работ подрядчики должны сверить размеры на объекте.
- Проектировщик не несет ответственности за достоверность информации, предоставленной производителями и поставщиками, за сроки поставки, качество выполненных работ, сроки монтажа субподрядными организациями.
- Размеры стен даны без учета штукатурного слоя отделочных материалов. Поэтому после проведения отделочных материалов рекомендуем сверить с проектом и внести изменения, либо согласовать в порядке авторского надзора с проектировщиком.
- Плинтус и напольное покрытие рассчитаны без учета подрезки. Взять с запасом 10%.
- Все артикулы и цвета проверить на объекте.

Дизайн проект интерьера
квартиры по адресу:
г. Москва ЖК "Headliner" 39/1


Стадия	Лист	Листов
РП	23	
Компания	Кодолов Групп	
Дизайнер	Заика Нина	
Дата	10.2022	

Все размеры уточнить на стадии
производственных работ

План раскладки
теплого пола

УСЛОВНЫЕ ОБОЗНАЧЕНИЯ

-  Терморегулятор теплого
пола. H-1400мм,
кроме отмеченных
на плане
-  Теплый пол




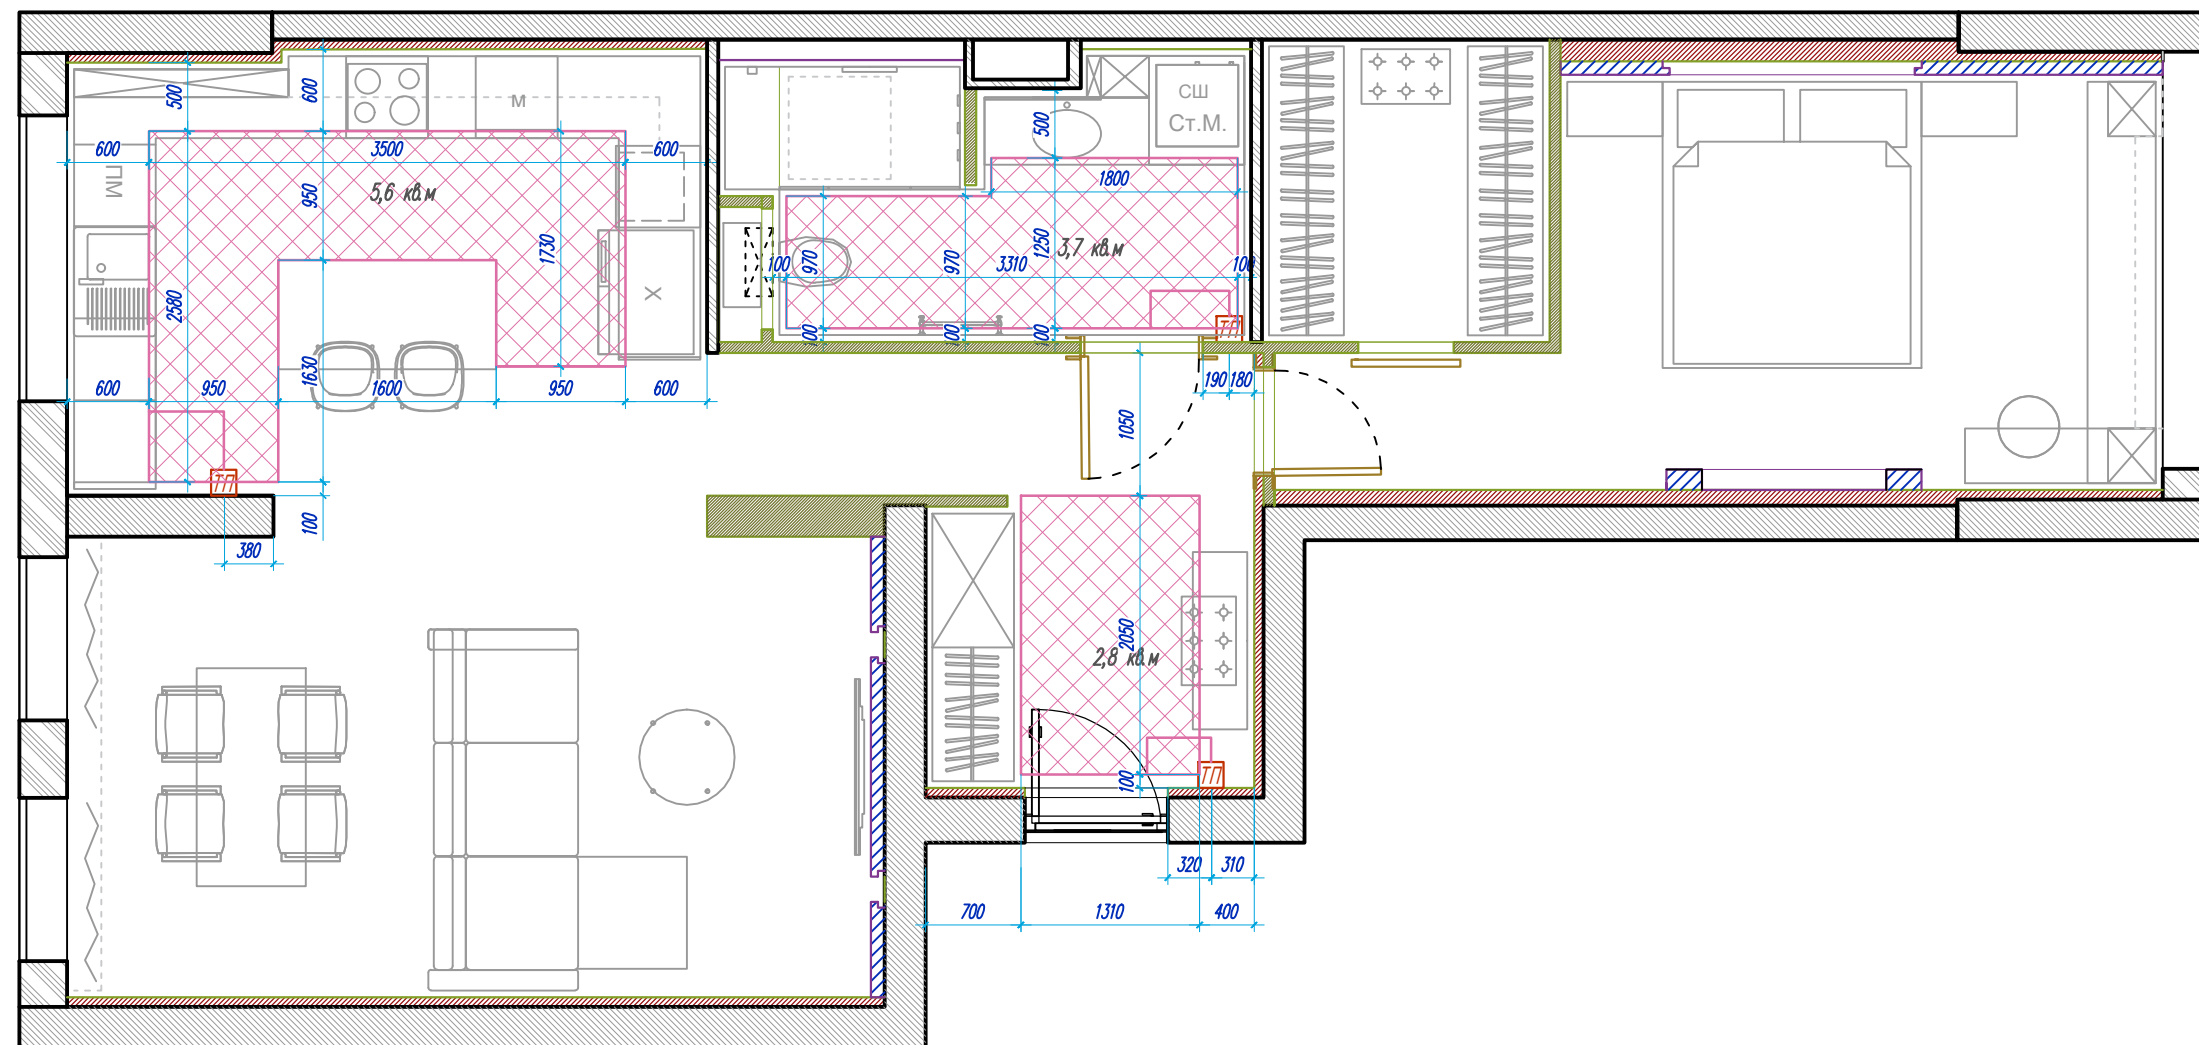


Примечание:
Все размеры и отметки, расход всех материалов, все
площади уточняются по месту. На каждом объекте возможны
увеличения или уменьшения размеров в зависимости от
технических допусков, кривизны, расхождения уровней стен и
потолков.


Дизайн проект интерьера
квартиры по адресу:
г. Москва ЖК "Headliner" 39/1

Стадия	Лист	Листов
РП	24	
Компания	Коголов Групп	
Дизайнер	Заика Нина	
Дата	10.2022	

Все размеры уточнить на стадии
производственных работ

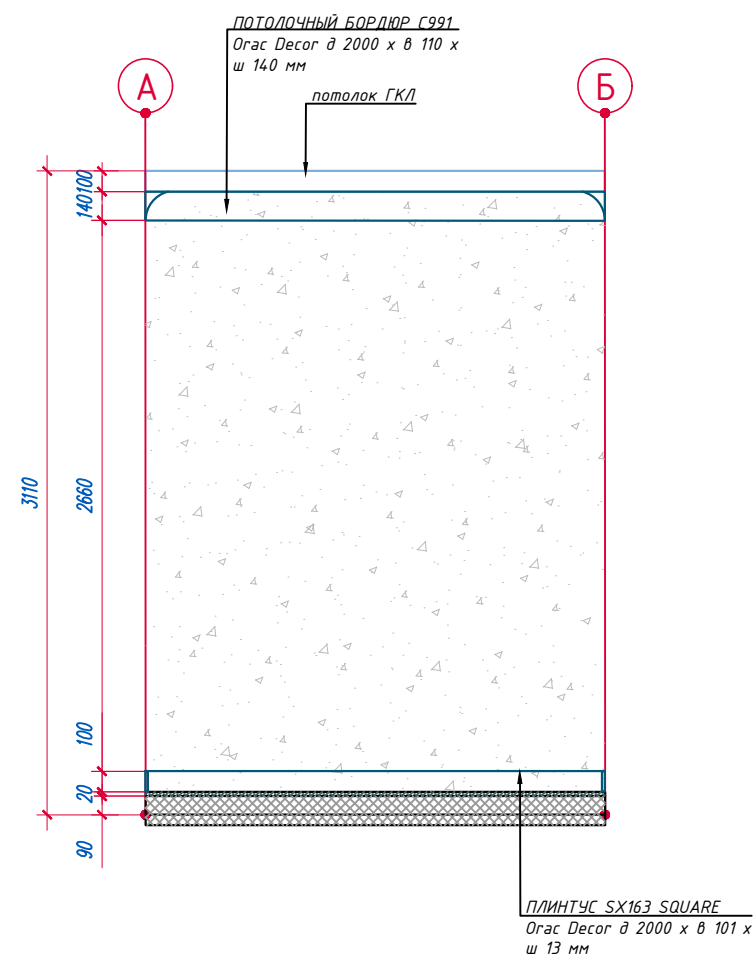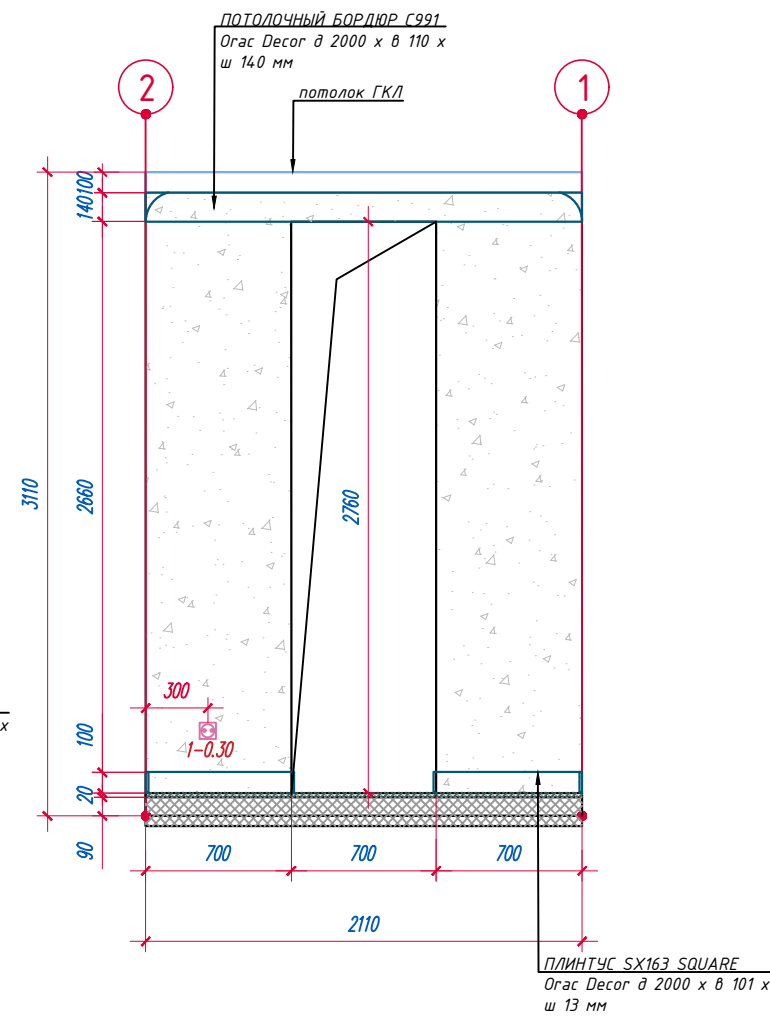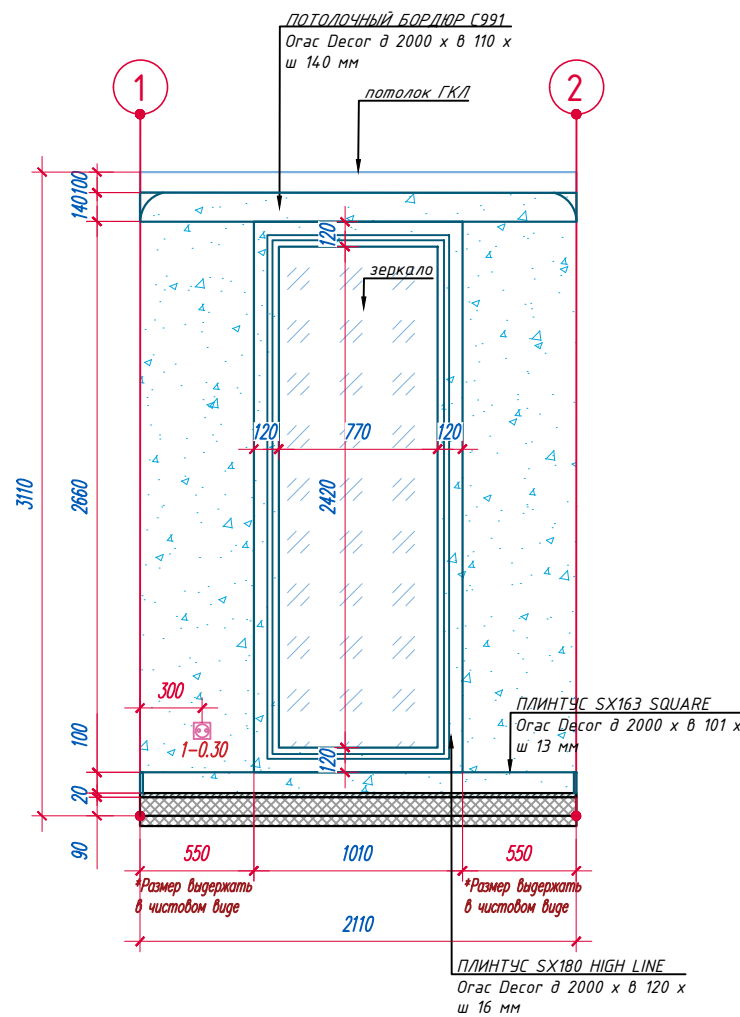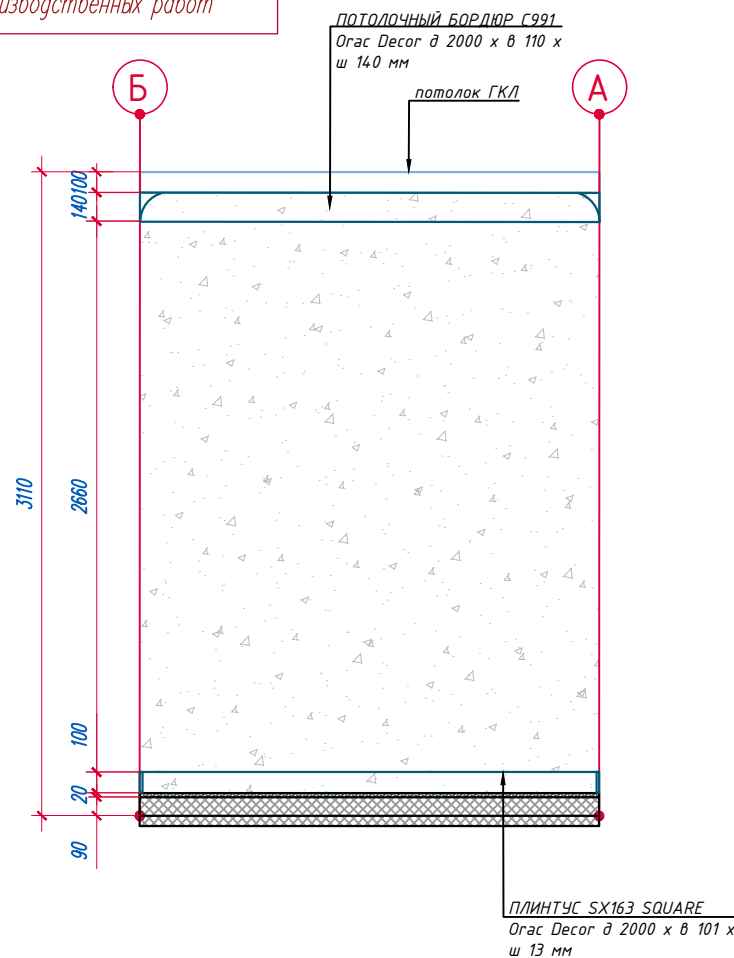

Примечание:
Все размеры и отметки, расход всех материалов, все
площади уточняются по месту. На каждом объекте возможны
увеличения или уменьшения размеров в зависимости от
технических допусков, кривизны, расхождения уровней стен и
потолков.

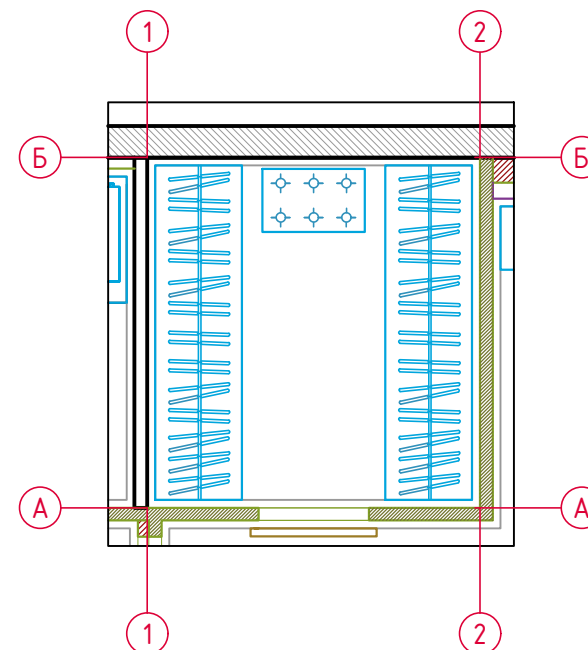

Развертки по гардеробу
(отделка стен,
расстановка мебели)

УСЛОВНЫЕ ОБОЗНАЧЕНИЯ



- А — ось привязки
- краска
цвет — голубой
- краска
цвет — серый

1. Все размеры указаны от чистого пола до середины блока (центра блока)
2. Размеры стен даны без учета штукатурного слоя отделочных материалов. Поэтому после проведения отделочных материалов рекомендуем сверить с проектом и внести изменения, либо согласовать в порядке авторского надзора с проектировщиком.
3. Проектировщик не несет ответственности за достоверность информации, предоставленной производителями, за сроки поставки, качество выполненных работ, сроки монтажа субподрядными организациями.
4. Смотреть совместно с планом розеток, выключателей, планировочным решением мебели и оборудования.
5. Перед началом каких-либо работ подрядчики должны сверить размеры на объекте.
6. Чистовую высоту стен уточнить после укладки стяжки и потолка.
7. Все высоты даны от чистого пола.
8. Размеры мебели уточняются производителем по месту.
9. Артикул и цвет краски и плитки уточнить по месту (при помощи выкрасов).



Дизайн проект интерьера
квартиры по адресу:
г. Москва ЖК "Headliner" 39/1

Стадия	Лист	Листов
РП	25	
Компания	Коголов Групп	
Дизайнер	Заика Нина	
Дата	11.2022	

Все размеры уточнить на стадии
производственных работ

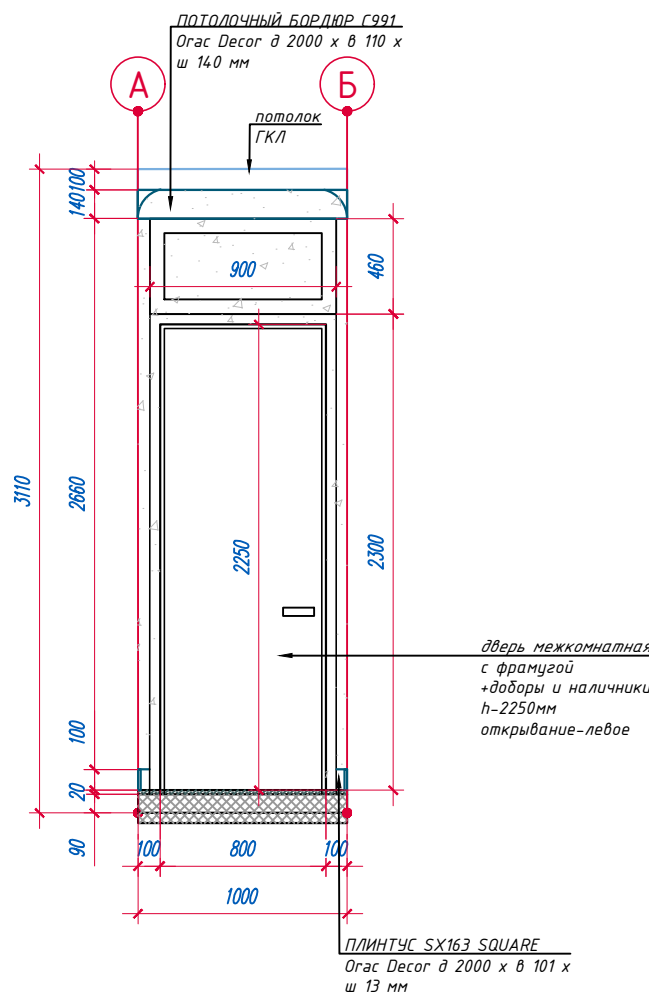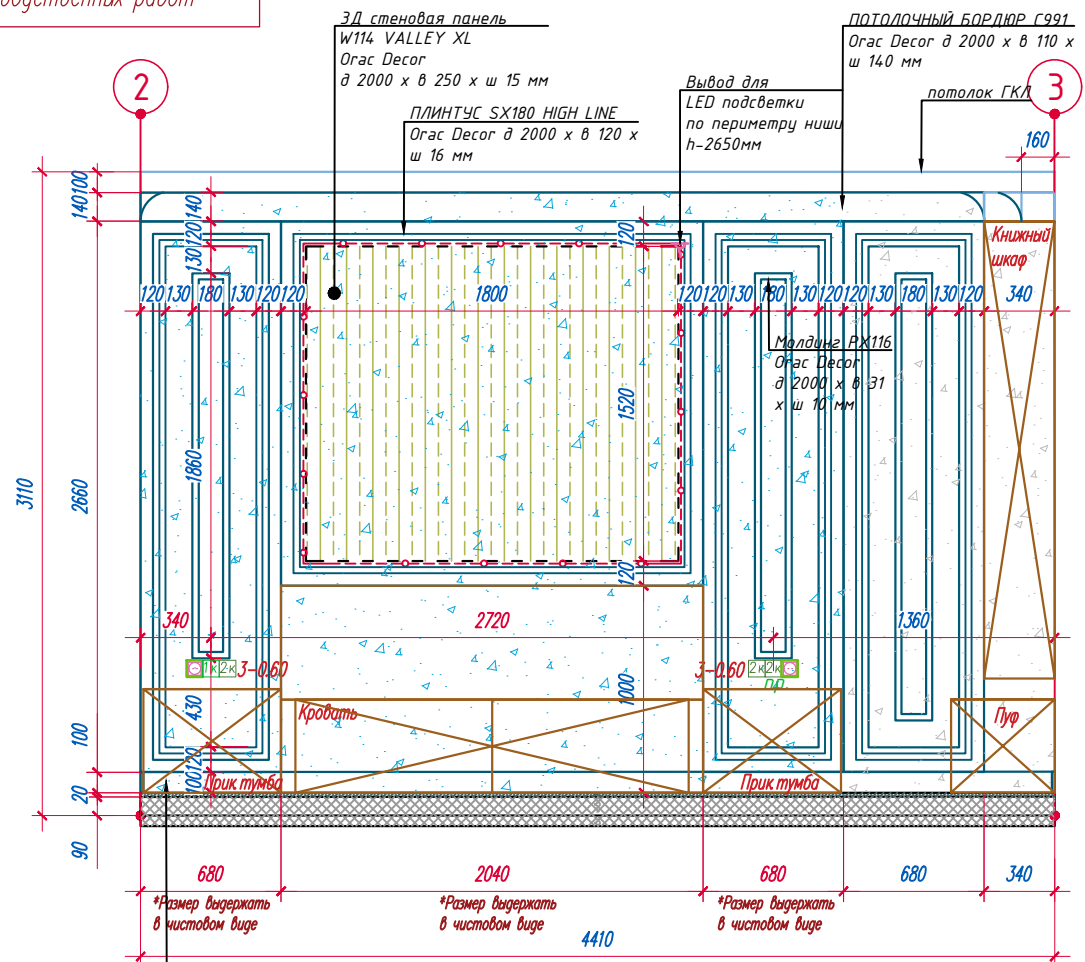

Примечание:
Все размеры и отметки, расход всех материалов, все
площади уточняются по месту. На каждом объекте возможны
увеличения или уменьшения размеров в зависимости от
технических допусков, кривизны, расхождения уровней стен и
потолков.

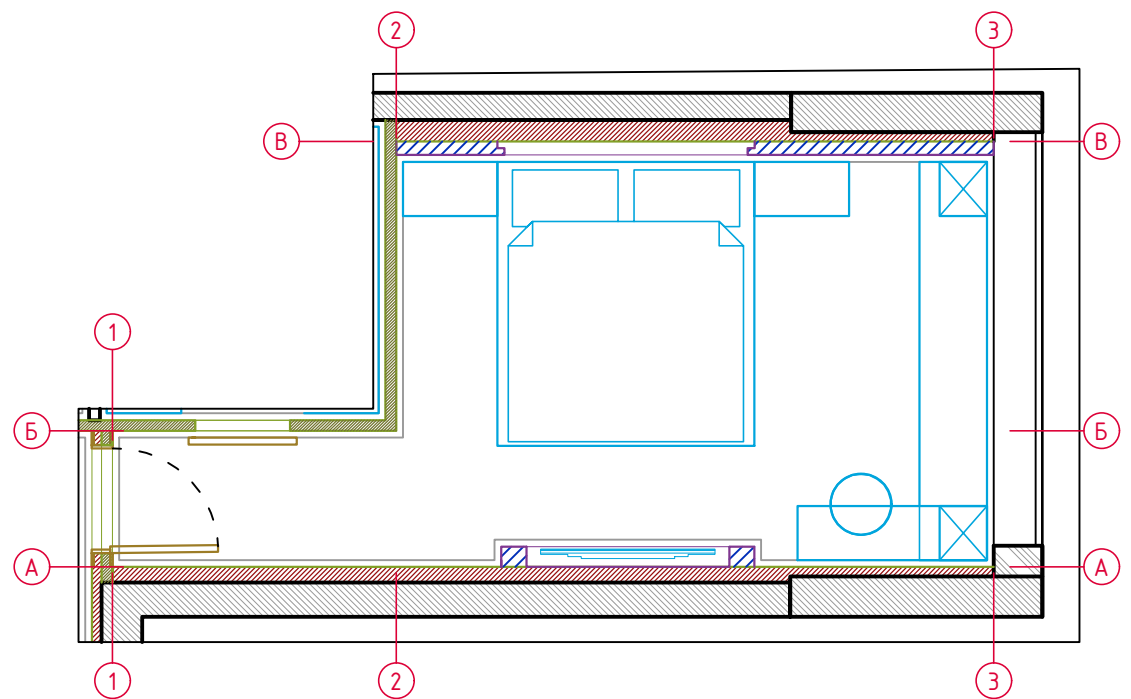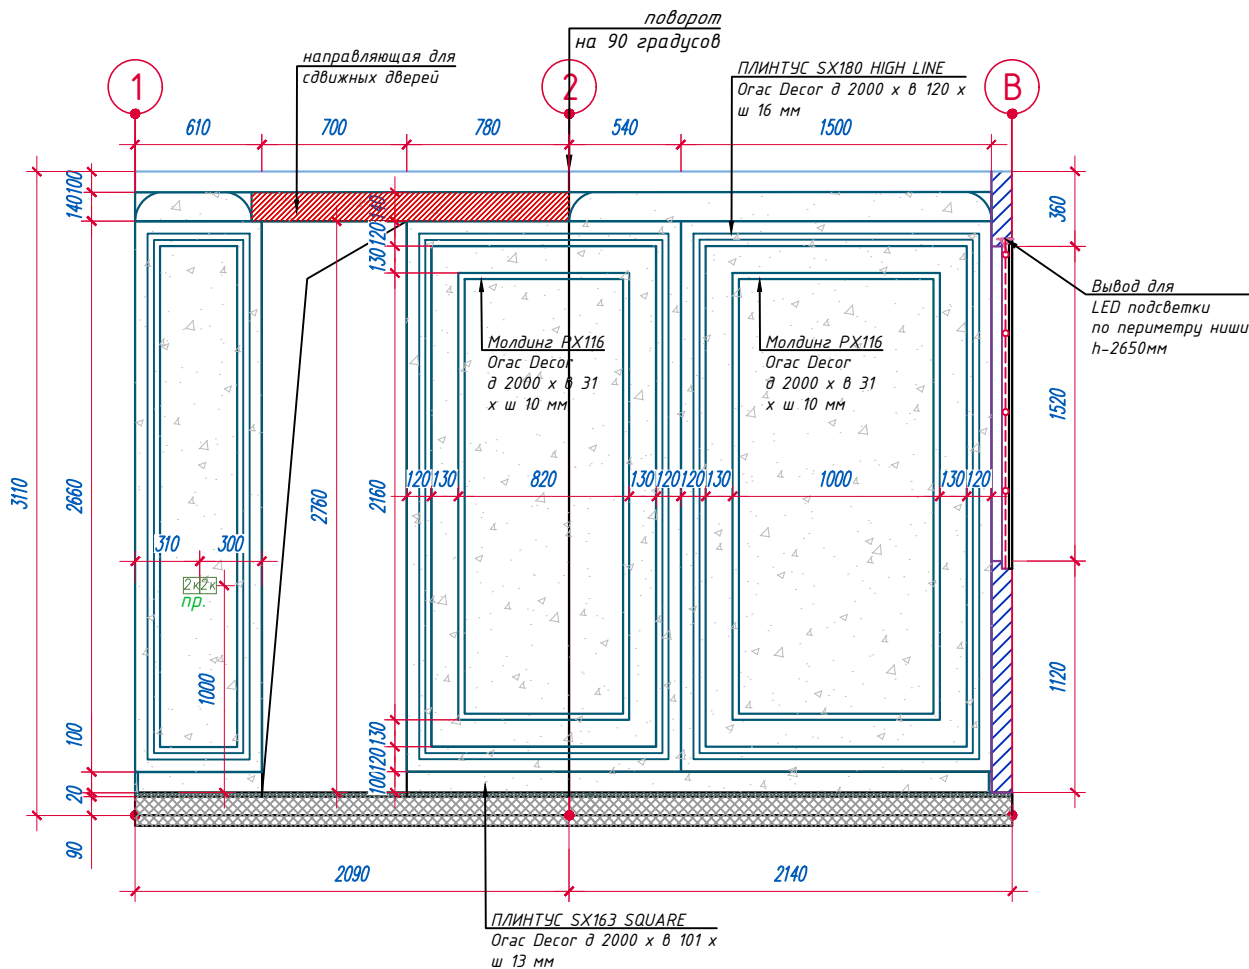

Развертки по спальне
(отделка стен,
расстановка мебели)

УСЛОВНЫЕ ОБОЗНАЧЕНИЯ


- А — ось привязки
- краска
цвет — голубой
- краска
цвет — серый

1. Все размеры указаны от чистого пола до середины блока (центра блока)
2. Размеры стен даны без учета штукатурного слоя отделочных материалов. Поэтому после проведения отделочных материалов рекомендуем сверить с проектом и внести изменения, либо согласовать в порядке авторского надзора с проектировщиком.
3. Проектировщик не несет ответственности за достоверность информации, предоставленной производителями, за сроки поставки, качество выполненных работ, сроки монтажа субподрядными организациями.
4. Смотреть совместно с планом розеток, выключателей, планировочным решением мебели и оборудования.
5. Перед началом каких-либо работ подрядчики должны сверить размеры на объекте.
6. Чистовую высоту стен уточнить после укладки стяжки и потолка.
7. Все высоты даны от чистого пола.
8. Размеры мебели уточняются производителем по месту.
9. Артикул и цвет краски и плитки уточнить по месту (при помощи выкрасов).

Дизайн проект интерьера
квартиры по адресу:
г. Москва ЖК "Headliner" 39/1

Стадия	Лист	Листов
РП	26	
Компания	Коголов Групп	
Дизайнер	Заика Нина	
Дата	11.2022	

Все размеры уточнить на стадии
производственных работ

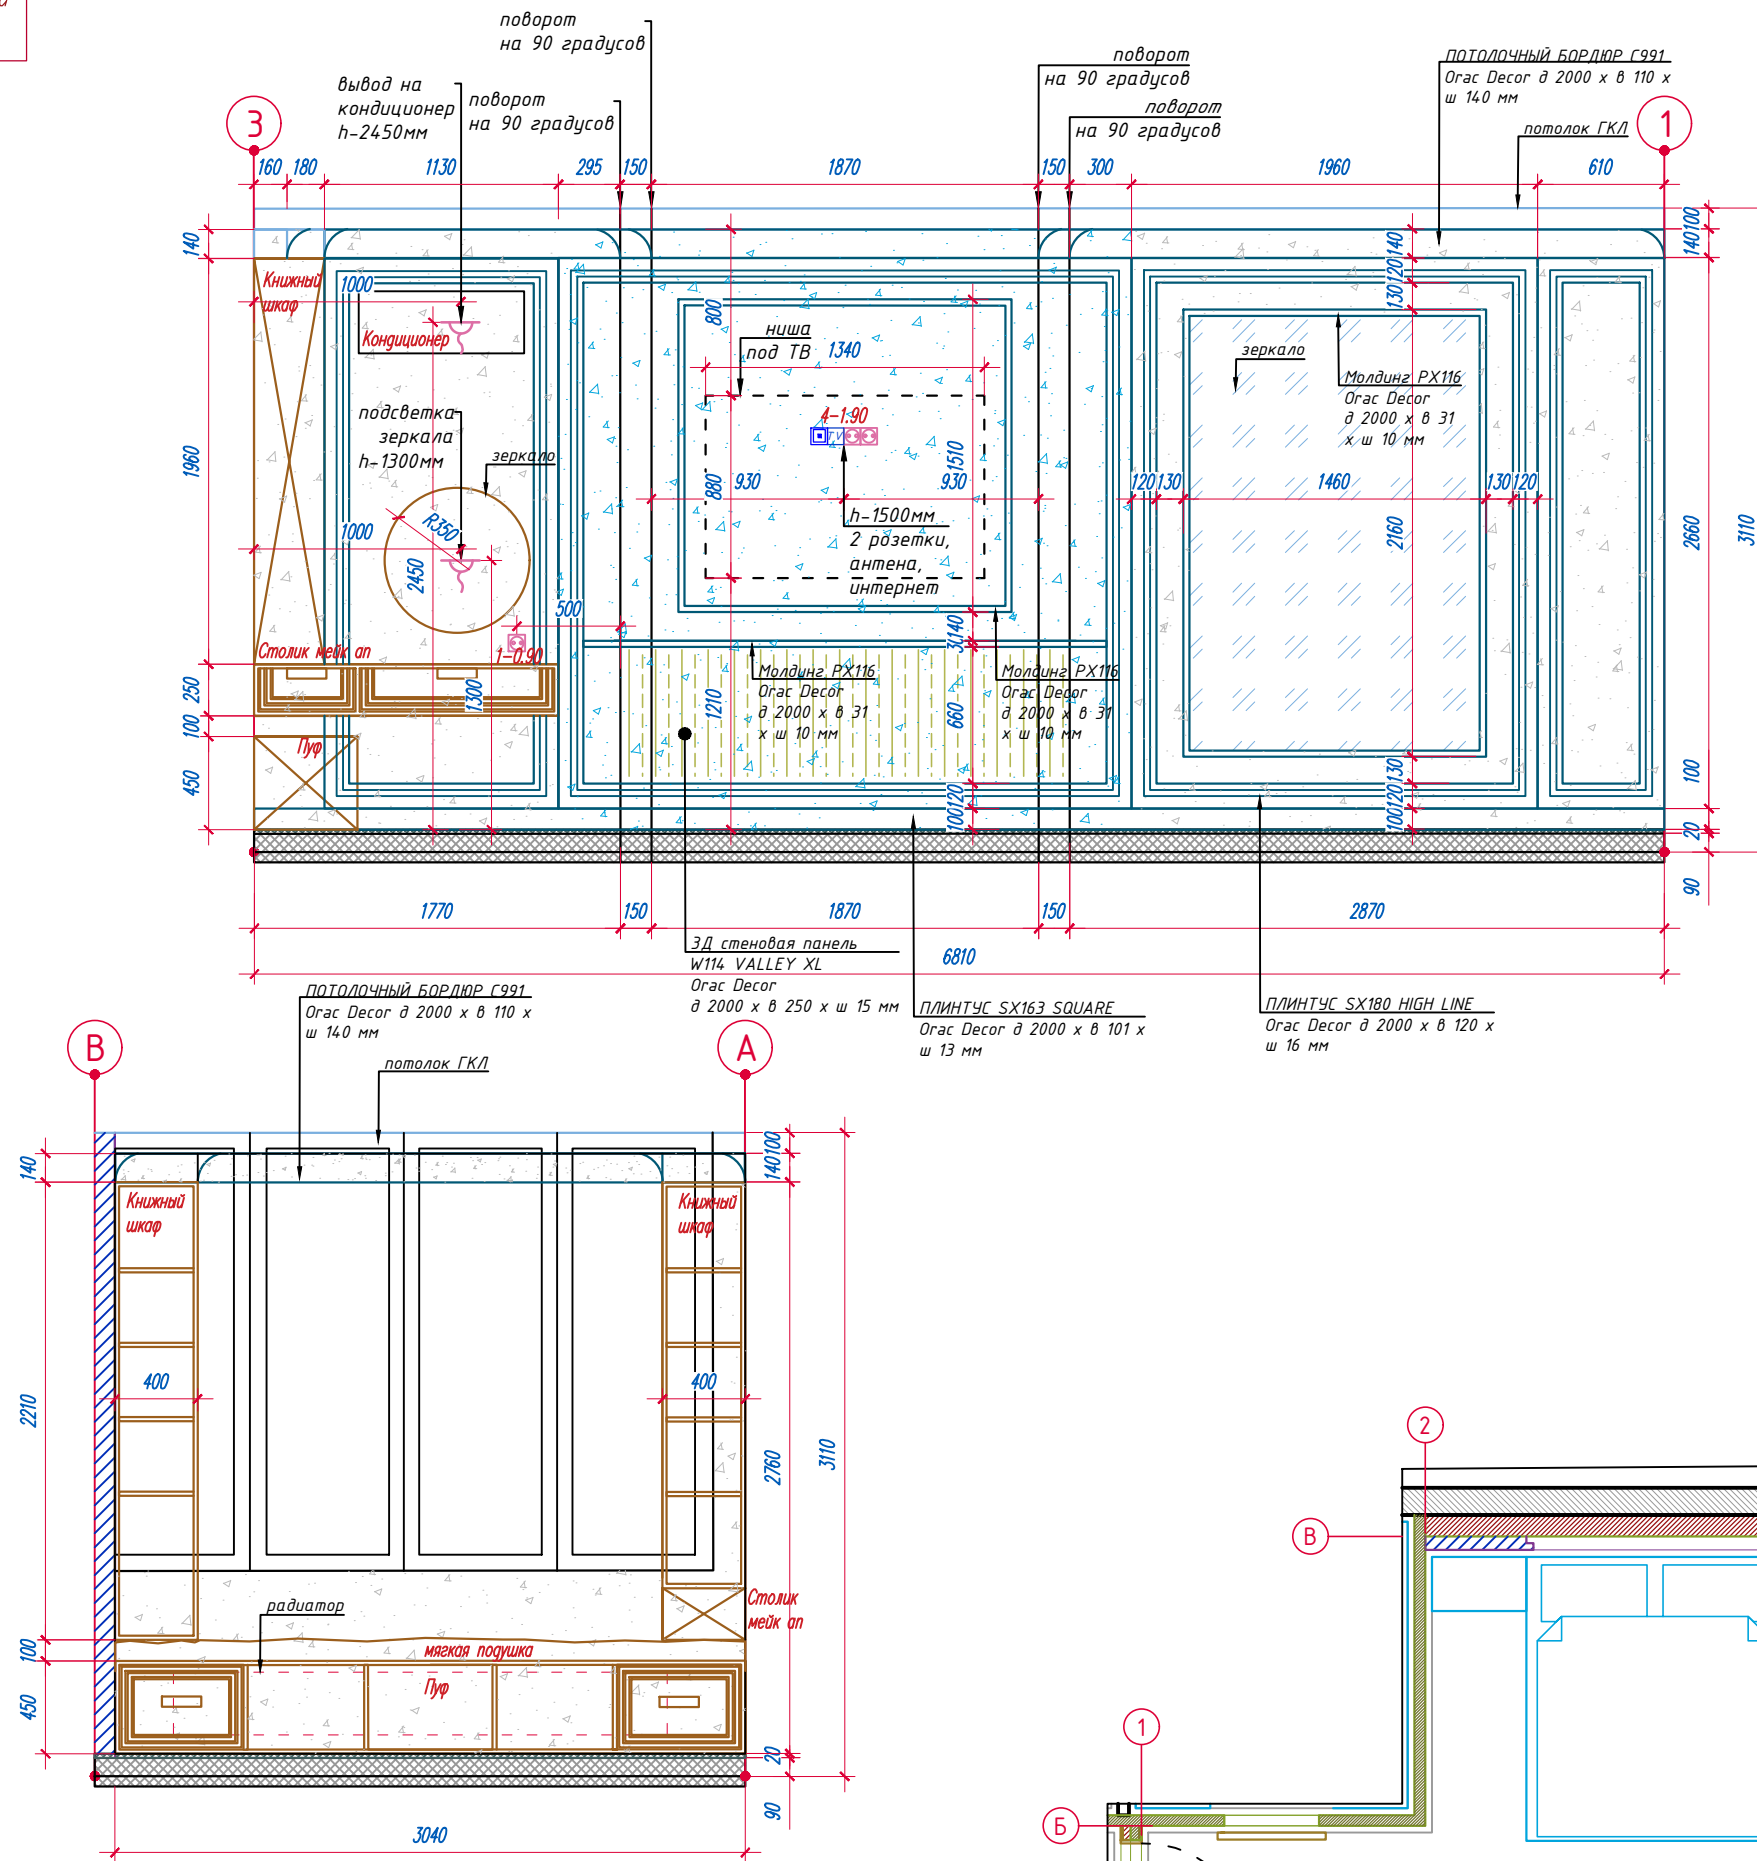

Примечание:
Все размеры и отметки, расход всех материалов, все
площади уточняются по месту. На каждом объекте возможны
увеличения или уменьшения размеров в зависимости от
технических допусков, кривизны, расхождения уровней стен и
потолков.

Развертки по спальне
(отделка стен,
расстановка мебели)

УСЛОВНЫЕ ОБОЗНАЧЕНИЯ




- А — Ось привязки
- краска
цвет — голубой
- краска
цвет — серый

- Все размеры указаны от чистого пола до середины блока (центра блока)
- Размеры стен даны без учета штукатурного слоя отделочных материалов. Поэтому после проведения отделочных материалов рекомендуем сверить с проектом и внести изменения, либо согласовать в порядке авторского надзора с проектировщиком.
- Проектировщик не несет ответственности за достоверность информации, предоставленной производителями, за сроки поставки, качество выполненных работ, сроки монтажа субподрядными организациями.
- Смотреть совместно с планом розеток, выключателей, планировочным решением мебели и оборудования.
- Перед началом каких-либо работ подрядчики должны сверить размеры на объекте.
- Чистовую высоту стен уточнить после укладки стяжки и потолка.
- Все высоты даны от чистого пола.
- Размеры мебели уточняются производителем по месту.
- Артикул и цвет краски и плитки уточнить по месту (при помощи выкрасов).

Дизайн проект интерьера
квартиры по адресу:
г. Москва ЖК "Headliner" 39/1

Стадия	Лист	Листов
РП	27	
Компания	Кодолов Групп	
Дизайнер	Заика Нина	
Дата	11.2022	

Все размеры уточнить на стадии
производственных работ

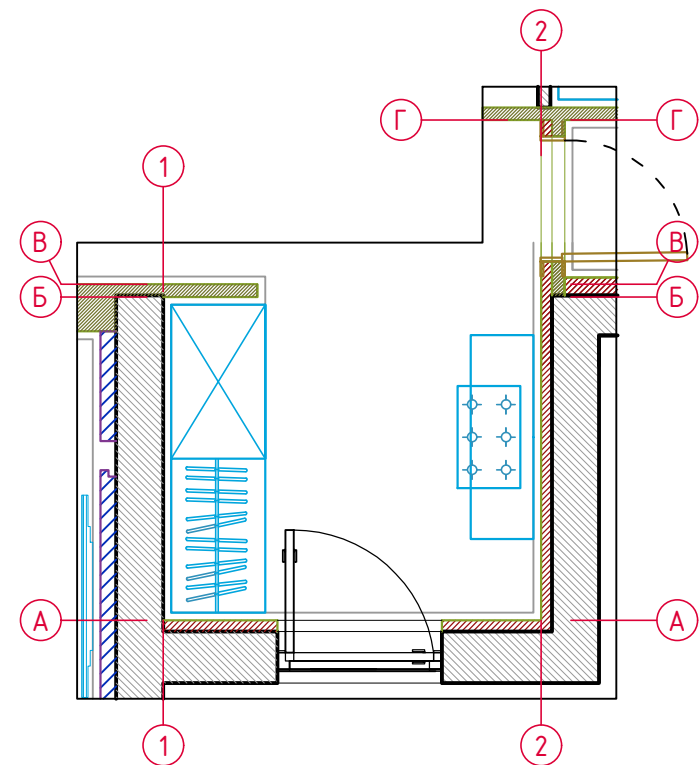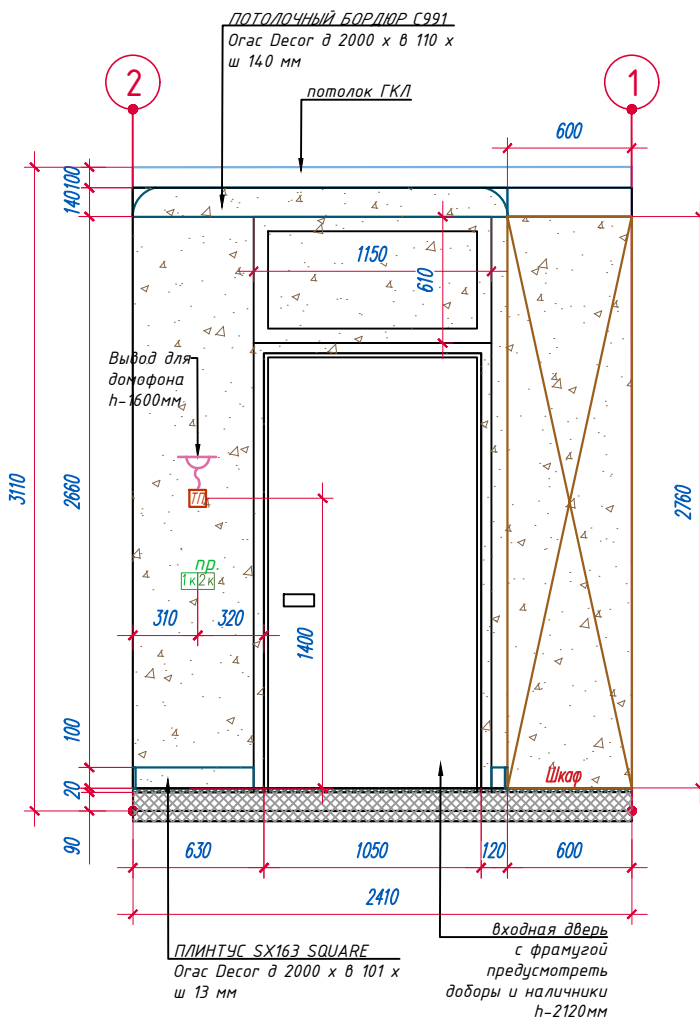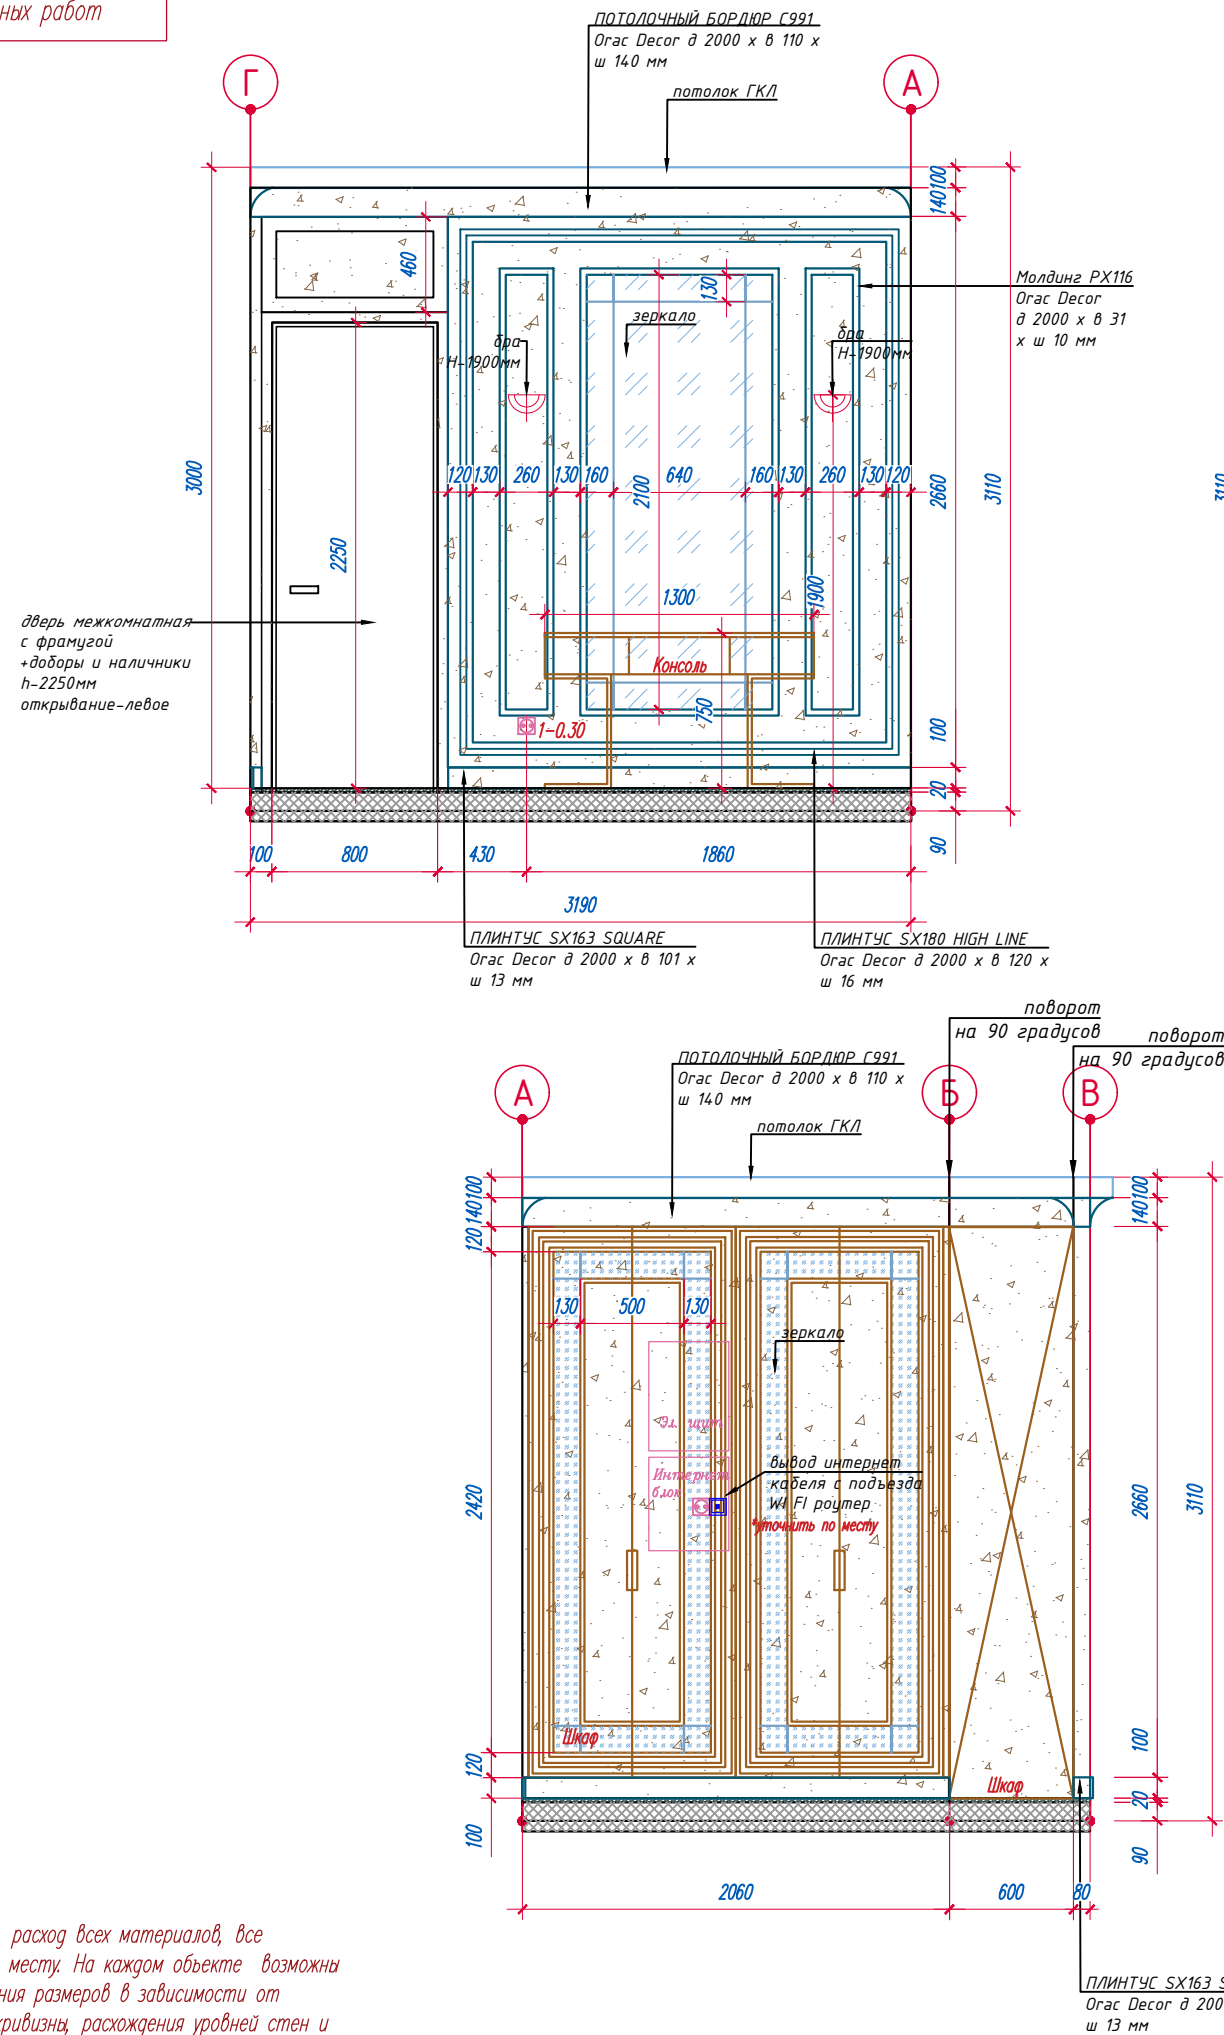

Развертки по прихожей
(отделка стен,
расстановка мебели)

УСЛОВНЫЕ ОБОЗНАЧЕНИЯ

- А — ось привязки
- краска
- цвет — бежевый




1. Все размеры указаны от чистого пола до середины блока (центра блока)
2. Размеры стен даны без учета штукатурного слоя отделочных материалов. Поэтому после проведения отделочных материалов рекомендуем сверить с проектом и внести изменения, либо согласовать в порядке авторского надзора с проектировщиком.
3. Проектировщик не несет ответственности за достоверность информации, предоставленной производителями, за сроки поставки, качество выполненных работ, сроки монтажа субподрядными организациями.
4. Смотреть совместно с планом розеток, выключателей, планировочным решением мебели и оборудования.
5. Перед началом каких-либо работ подрядчики должны сверить размеры на объекте.
6. Чистовую высоту стен уточнить после укладки стяжки и потолка.
7. Все высоты даны от чистого пола.
8. Размеры мебели уточняются производителем по месту.
9. Артикул и цвет краски и плитки уточнить по месту (при помощи выкрасов).

Дизайн проект интерьера
квартиры по адресу:
г. Москва ЖК "Headliner" 39/1

Стадия	Лист	Листов
РП	28	
Компания	Коголов Групп	
Дизайнер	Заика Нина	
Дата	11.2022	

Примечание:
Все размеры и отметки, расход всех материалов, все площади уточняются по месту. На каждом объекте возможны увеличения или уменьшения размеров в зависимости от технических допусков, кривизны, расхождения уровней стен и потолков.

Все размеры уточнить на стадии
производственных работ

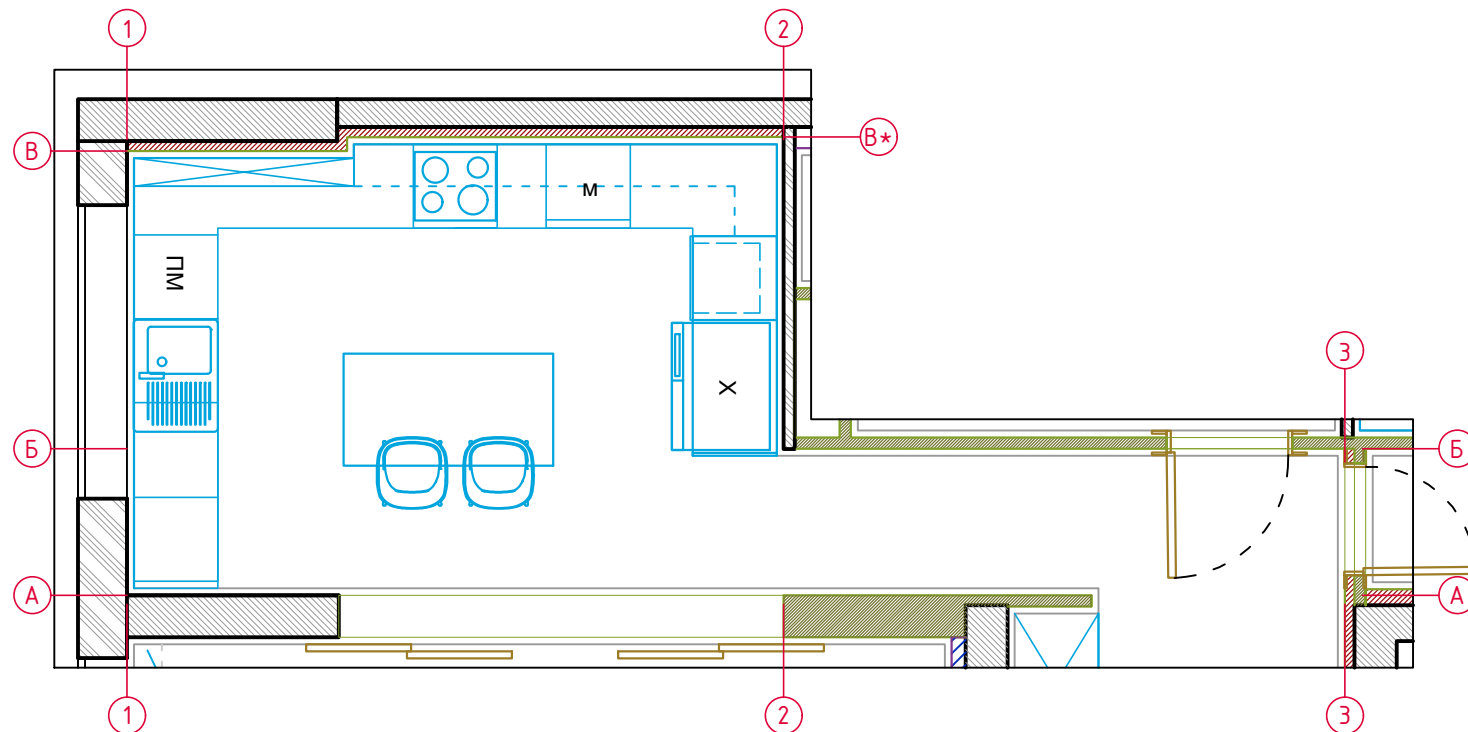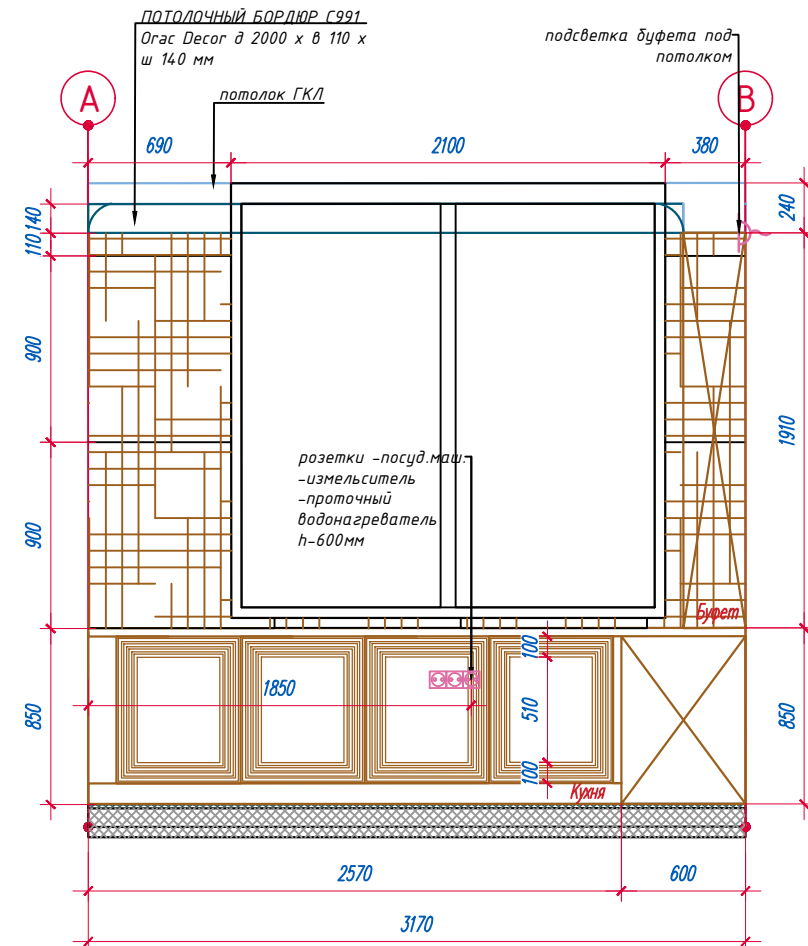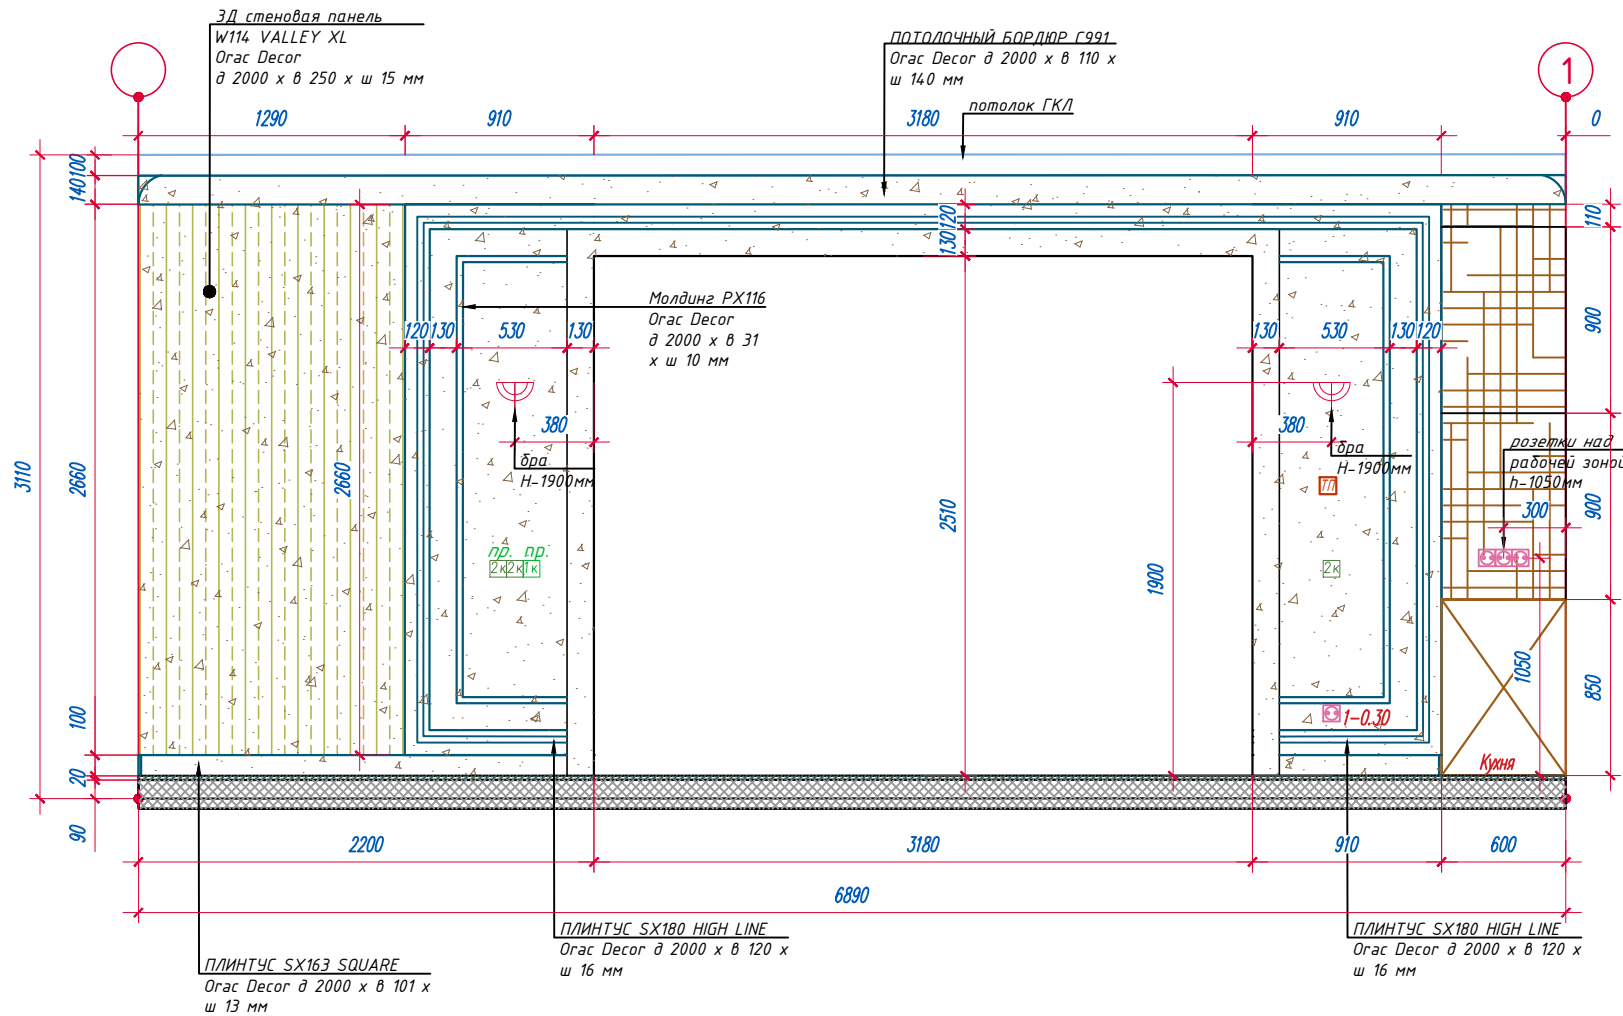

Примечание:
Все размеры и отметки, расход всех материалов, все
площади уточняются по месту. На каждом объекте возможны
увеличения или уменьшения размеров в зависимости от
технических допусков, кривизны, расхождения уровней стен и
потолков.

Развертки по кухне
(отделка стен,
расстановка мебели)

УСЛОВНЫЕ ОБОЗНАЧЕНИЯ





- А — ось привязки
- краска
цвет — бежевый
- зеркало
- 187971Selene Light Pul.
керамогранит Dune 900x900 мм

- Все размеры указаны от чистого пола до середины блока (центра блока)
- Размеры стен даны без учета штукатурного слоя отделочных материалов. Поэтому после проведения отделочных материалов рекомендуем сверить с проектом и внести изменения, либо согласовать в порядке авторского надзора с проектировщиком.
- Проектировщик не несет ответственности за достоверность информации, предоставленной производителем, за сроки поставки, качество выполненных работ, сроки монтажа субподрядными организациями.
- Смотреть совместно с планом розеток, выключателей, планировочным решением мебели и оборудования.
- Перед началом каких-либо работ подрядчики должны сверить размеры на объекте.
- Чистовую высоту стен уточнить после укладки стяжки и потолка.
- Все высоты даны от чистого пола.
- Размеры мебели уточняются производителем по месту.
- Артикул и цвет краски и плитки уточнить по месту (при помощи выкрасов).

Дизайн проект интерьера
квартиры по адресу:
г. Москва ЖК "Headliner" 39/1

Стадия	Лист	Листов
РП	29	
Компания	Коголов Групп	
Дизайнер	Заика Нина	
Дата	11.2022	

Все размеры уточнить на стадии
производственных работ

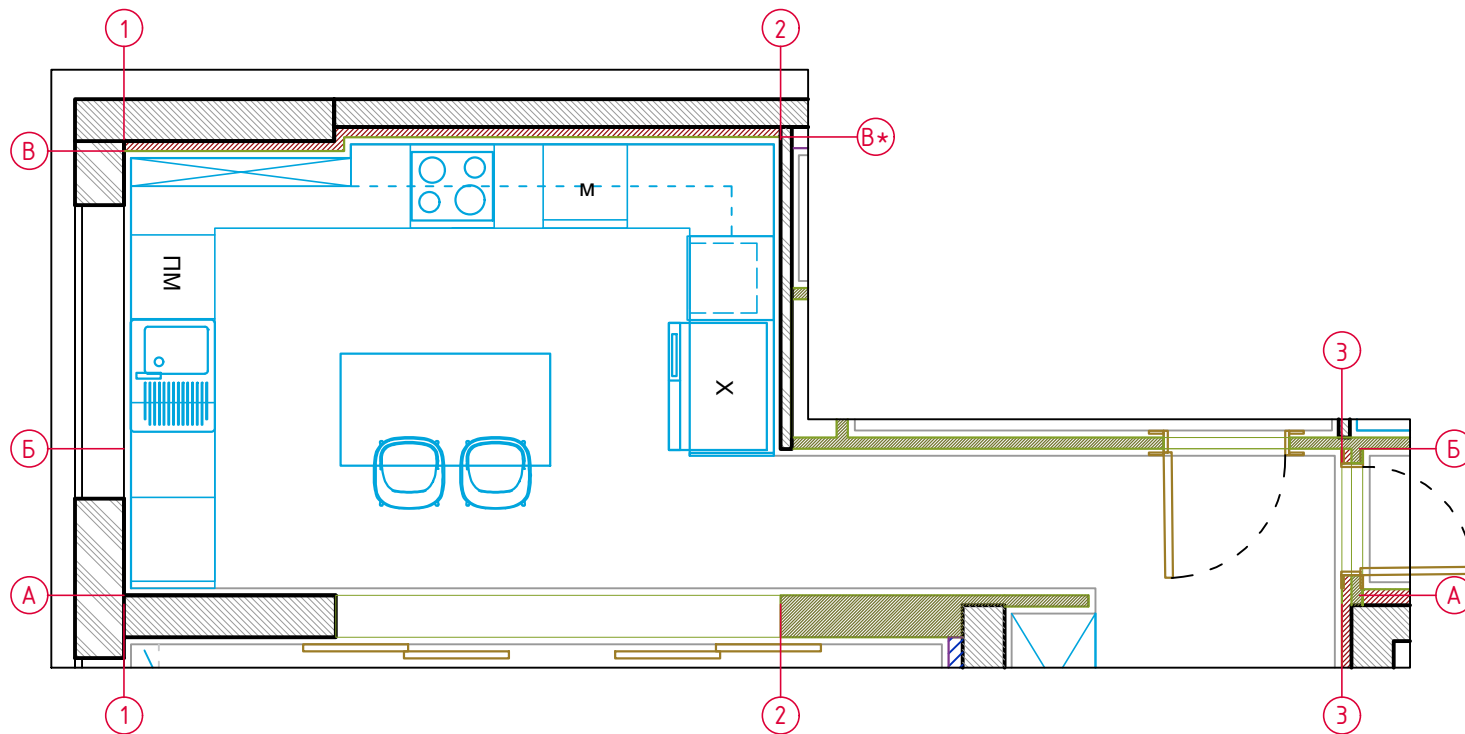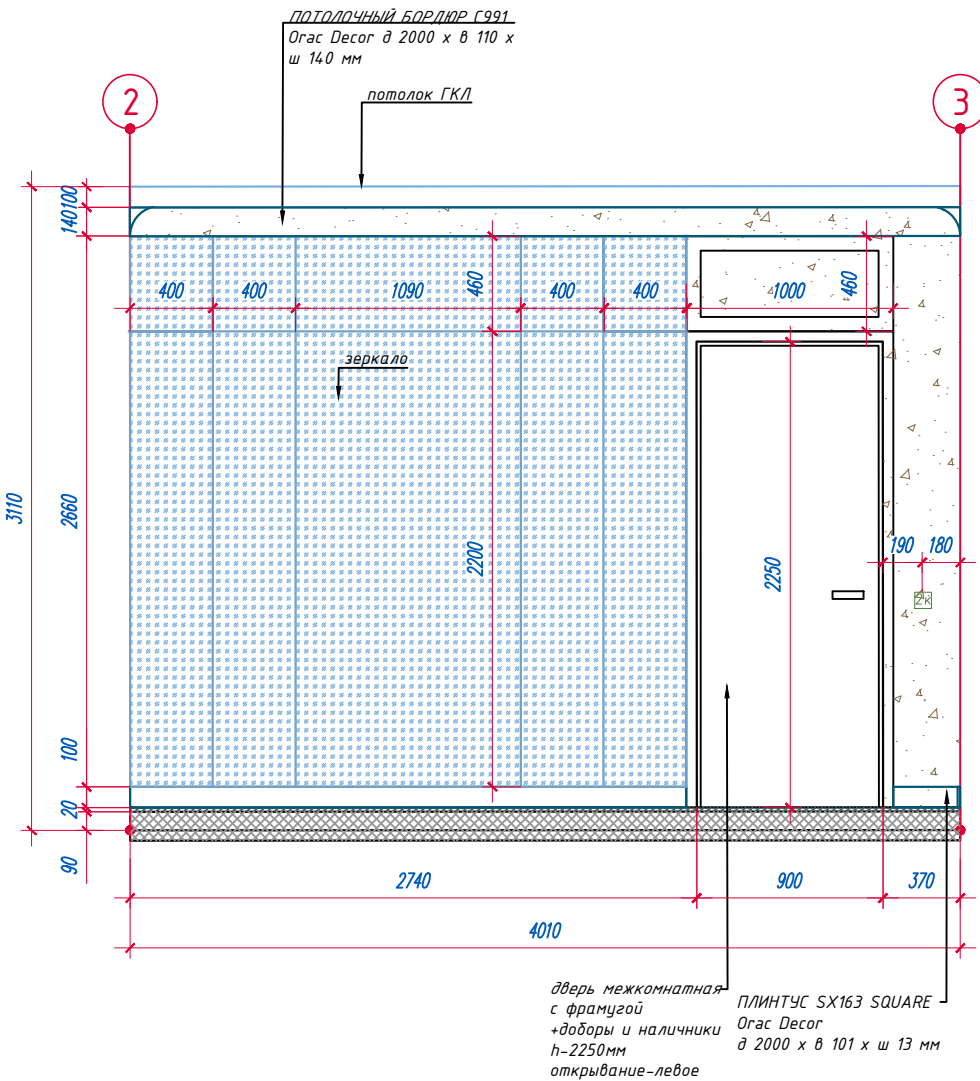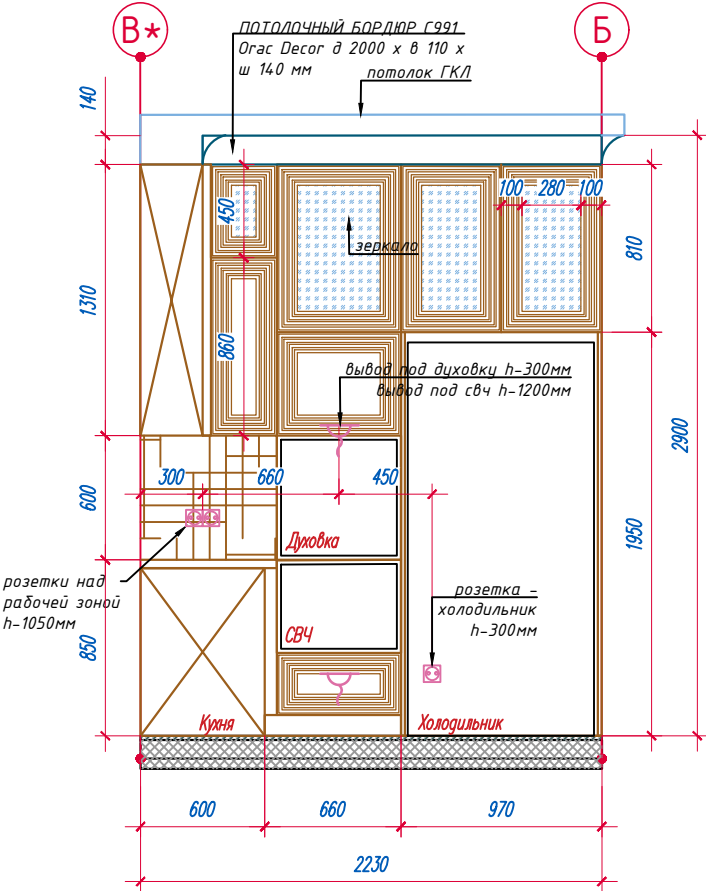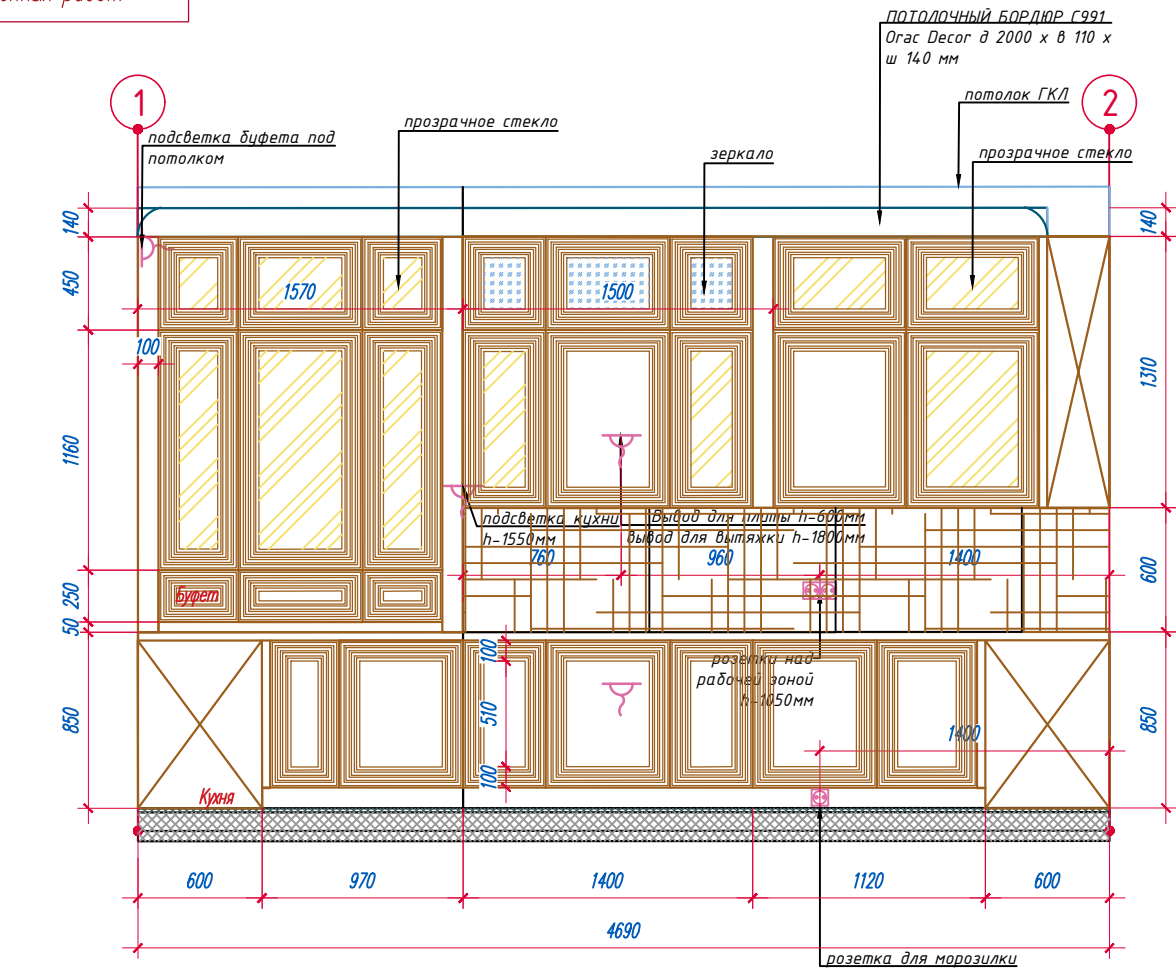

Развертки по кухне
(отделка стен,
расстановка мебели)

УСЛОВНЫЕ ОБОЗНАЧЕНИЯ

- А — Ось привязки
- краска
цвет — бежевый
- зеркало
- 187971Selene Light Pul.
керамогранит Dune 900×900мм




- Все размеры указаны от чистого пола до середины блока (центра блока)
- Размеры стен даны без учета штукатурного слоя отделочных материалов. Поэтому после проведения отделочных материалов рекомендуем сверить с проектом и внести изменения, либо согласовать в порядке авторского надзора с проектировщиком.
- Проектировщик не несет ответственности за достоверность информации, предоставленной производителями, за сроки поставки, качество выполненных работ, сроки монтажа субподрядными организациями.
- Смотреть совместно с планом розеток, выключателей, планировочным решением мебели и оборудования.
- Перед началом каких-либо работ подрядчики должны сверить размеры на объекте.
- Чистовую высоту стен уточнить после укладки стяжки и потолка.
- Все высоты даны от чистого пола.
- Размеры мебели уточняются производителем по месту.
- Артикул и цвет краски и плитки уточнить по месту (при помощи выкрасов).

Дизайн проект интерьера
квартиры по адресу:
г. Москва ЖК "Headliner" 39/1

Стадия	Лист	Листов
РП	30	
Компания	Коголов Групп	
Дизайнер	Заика Нина	
Дата	11.2022	

Примечание:
Все размеры и отметки, расход всех материалов, все площади уточняются по месту. На каждом объекте возможны увеличения или уменьшения размеров в зависимости от технических допусков, кривизны, расхождения уровней стен и потолков.

Все размеры уточнить на стадии
производственных работ

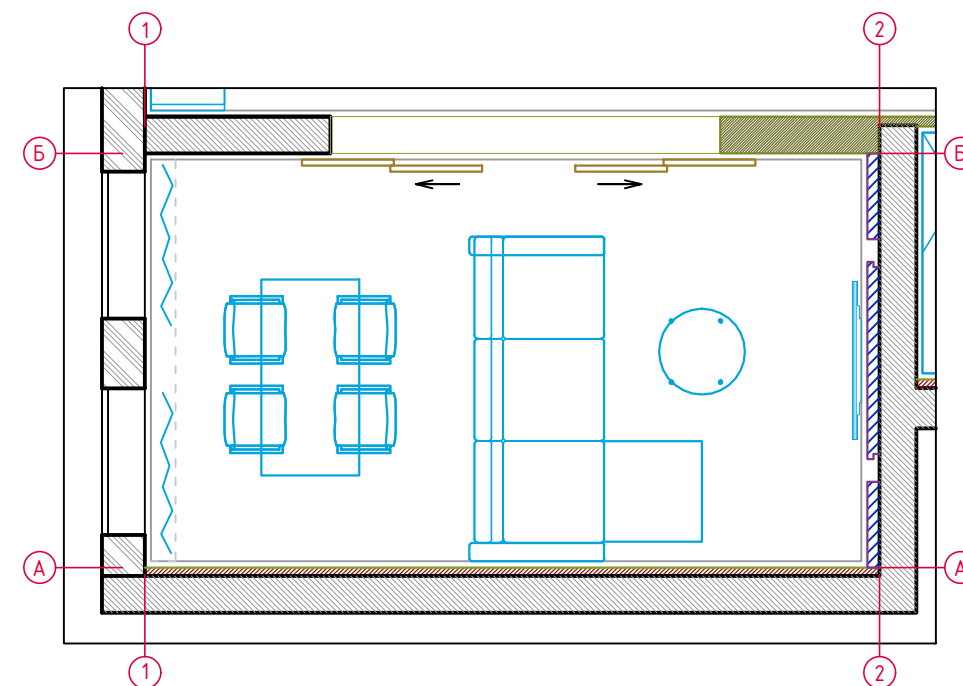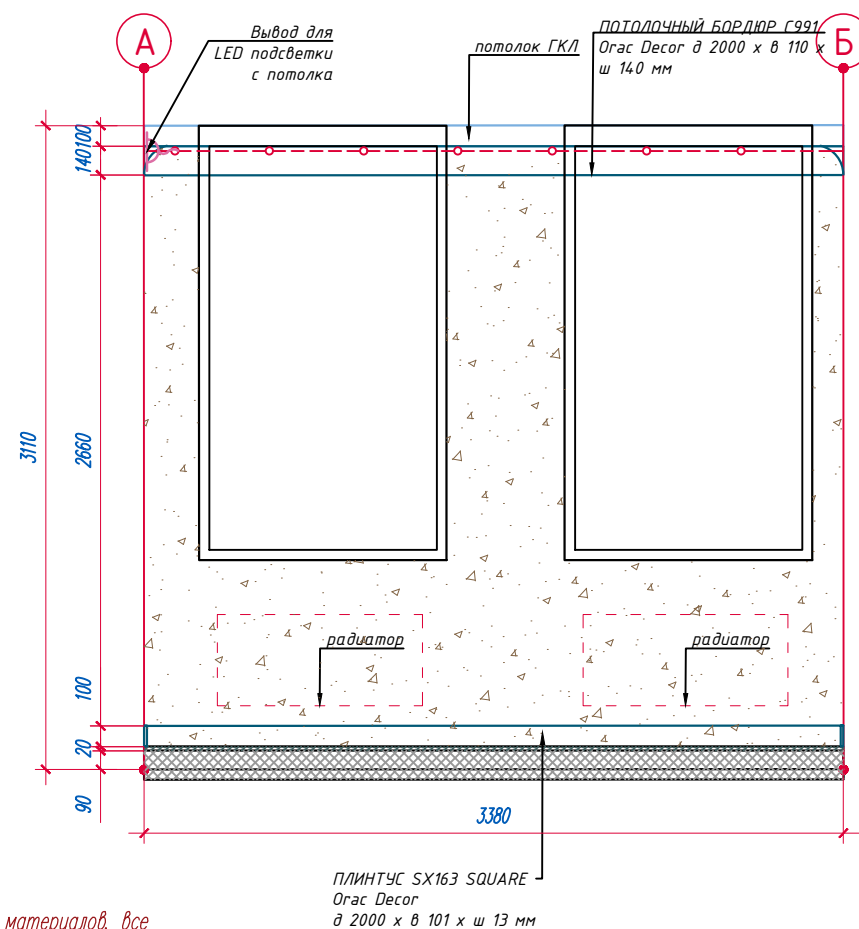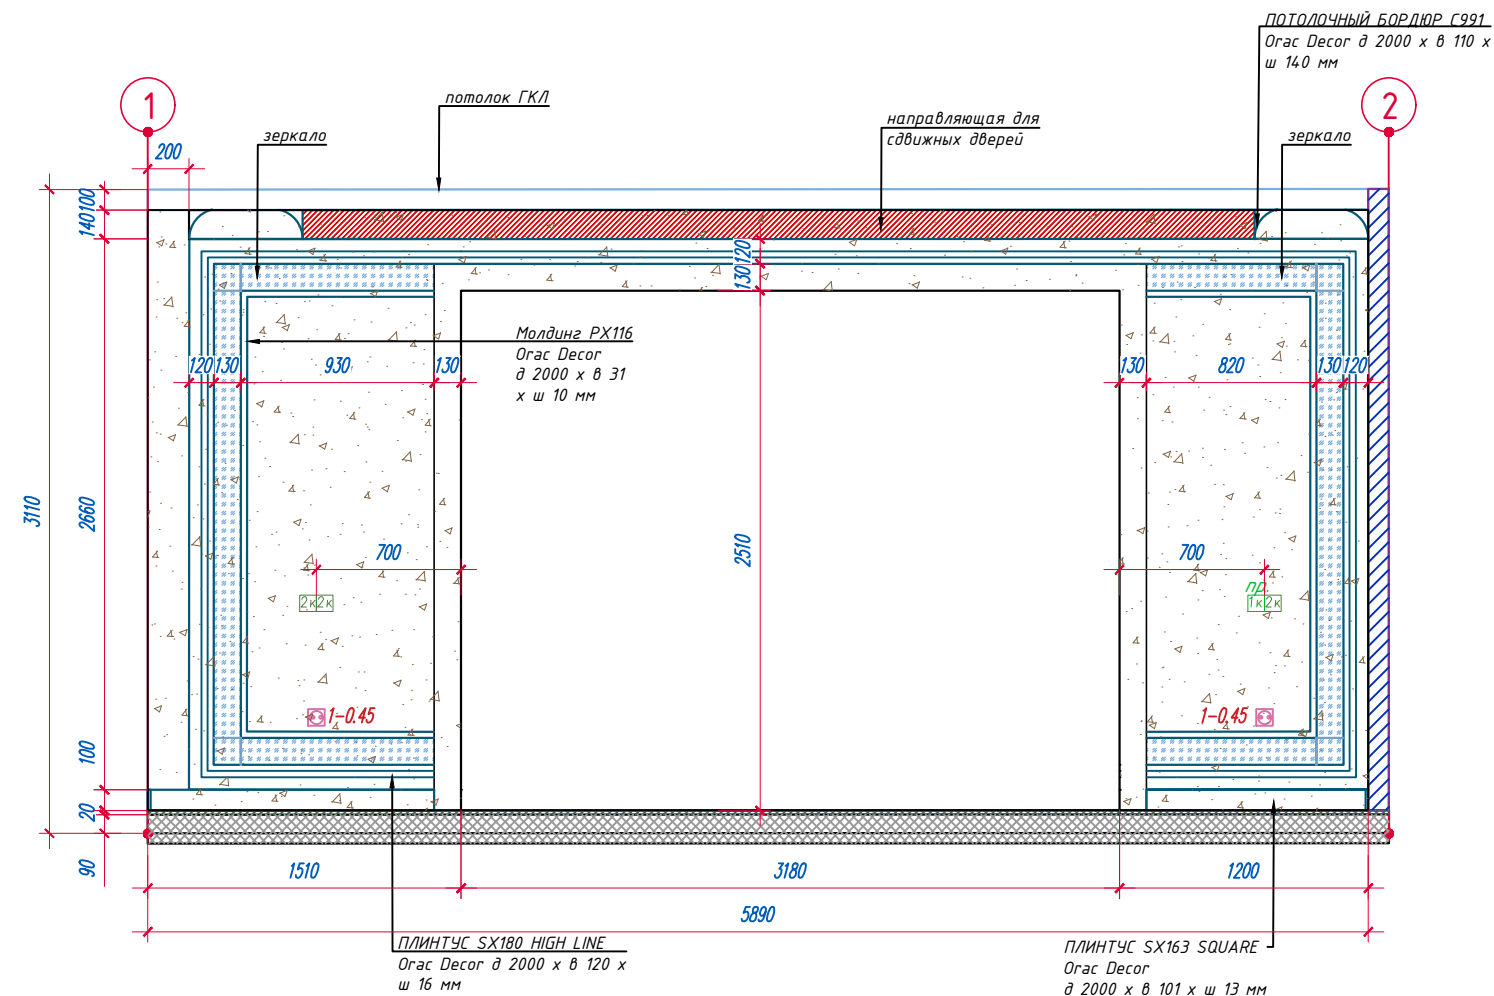

Примечание:
Все размеры и отметки, расход всех материалов, все
площади уточняются по месту. На каждом объекте возможны
увеличения или уменьшения размеров в зависимости от
технических допусков, кривизны, расхождения уровней стен и
потолков.

Развертки по гостиной
(отделка стен,
расстановка мебели)

УСЛОВНЫЕ ОБОЗНАЧЕНИЯ


- А — ось привязки
- краска
цвет — бежевый
- зеркало

- Все размеры указаны от чистого пола до середины блока (центра блока)
- Размеры стен даны без учета штукатурного слоя отделочных материалов. Поэтому после проведения отделочных материалов рекомендуем сверить с проектом и внести изменения, либо согласовать в порядке авторского надзора с проектировщиком.
- Проектировщик не несет ответственности за достоверность информации, предоставленной производителями, за сроки поставки, качество выполненных работ, сроки монтажа субподрядными организациями.
- Смотреть совместно с планом розеток, выключателей, планировочным решением мебели и оборудования.
- Перед началом каких-либо работ подрядчики должны сверить размеры на объекте.
- Чистовую высоту стен уточнить после укладки стяжки и потолка.
- Все высоты даны от чистого пола.
- Размеры мебели уточняются производителем по месту.
- Артикул и цвет краски и плитки уточнить по месту (при помощи выкрасов).

Дизайн проект интерьера
квартиры по адресу:
г. Москва ЖК "Headliner" 39/1

Стадия	Лист	Листов
РП	31	
Компания	Коголов Групп	
Дизайнер	Заика Нина	
Дата	11.2022	

Все размеры уточнить на стадии
производственных работ

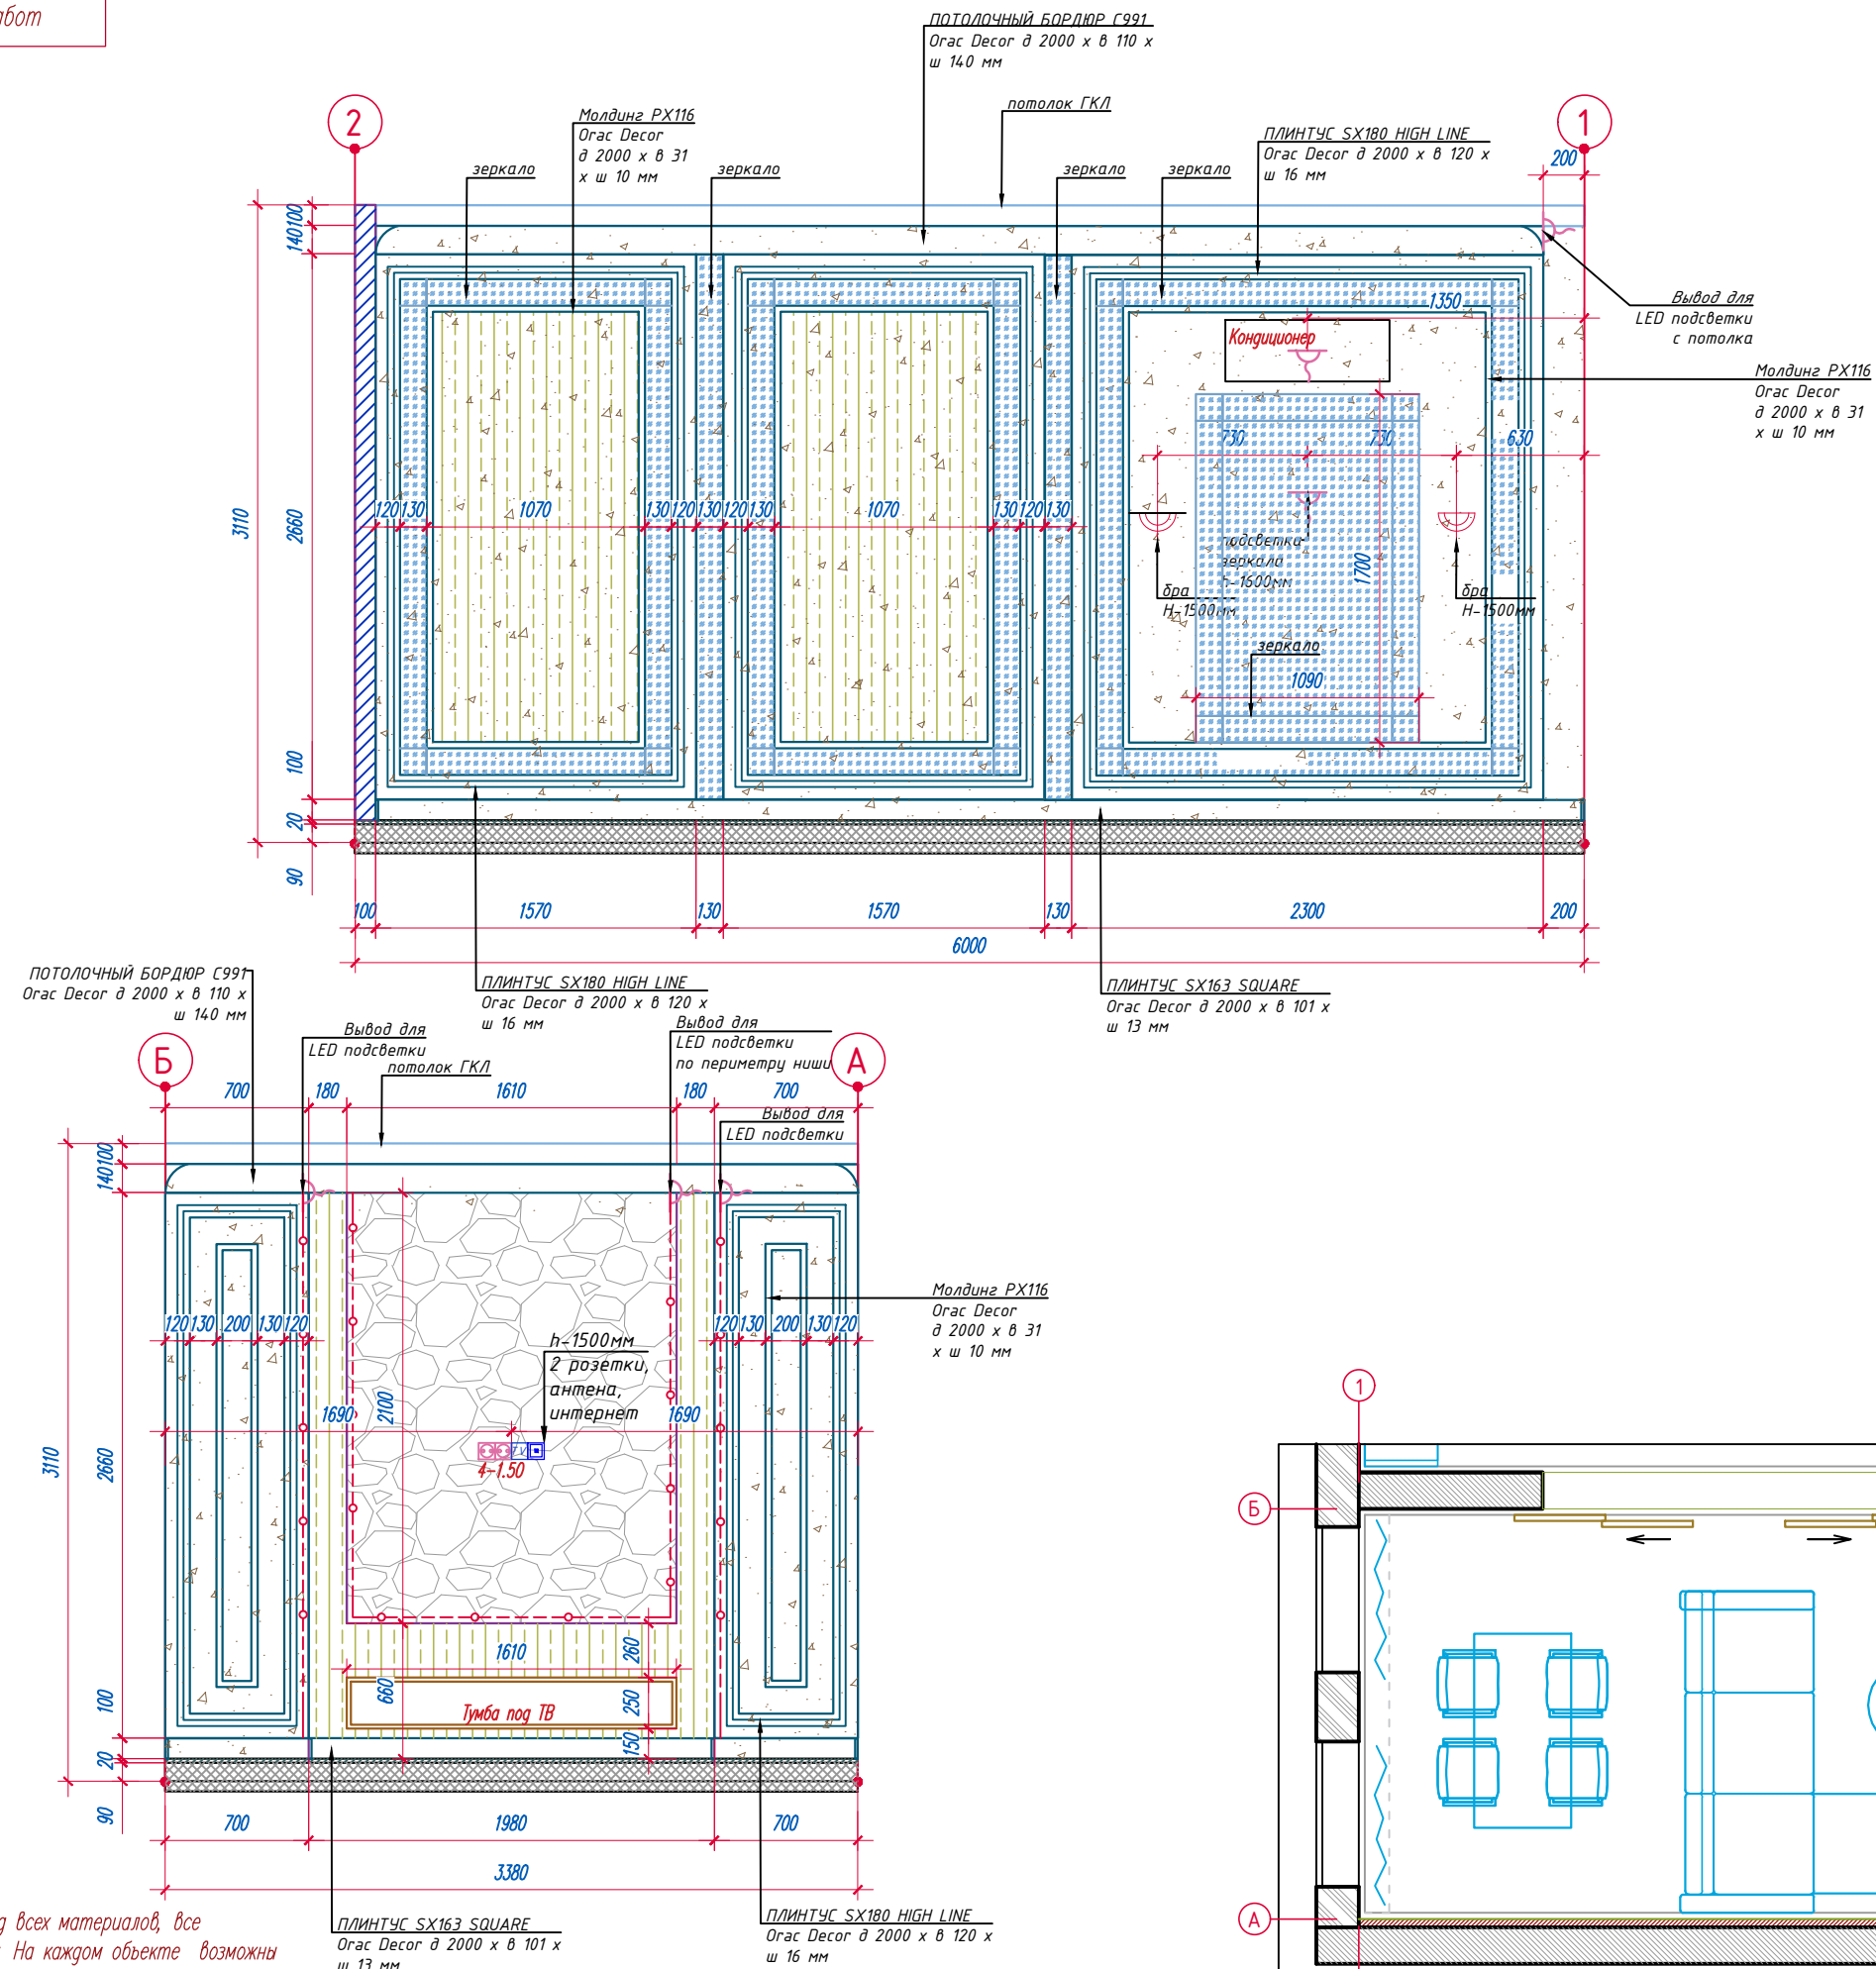

Примечание:
Все размеры и отметки, расход всех материалов, все площади уточняются по месту. На каждом объекте возможны увеличения или уменьшения размеров в зависимости от технических припусков, кривизны, расхождения уровней стен и потолка.

Развертки по гостиной
(отделка стен,
расстановка мебели)

УСЛОВНЫЕ ОБОЗНАЧЕНИЯ

А — Ось привязки

 краска
цвет – бежевый

 *зеркало*









Agata Black Luc. 6 mm
керамогранит Maxfine
1500x3000 мм

1. Все размеры указаны от чистого пола до середины блока (центра блока)
2. Размеры стен даны без учета штукатурного слоя отделочных материалов. Поэтому после проведения отделочных материалов рекомендуем сверить с проектом и внести изменения, либо согласовать в порядке авторского надзора с проектировщиком.
3. Проектировщик не несет ответственности за достоверность информации, предоставленной производителям, за сроки поставки, качество выполненных работ, сроки монтажа субподрядными организациями.
4. Смотреть совместно с планом розеток, выключателей, планировочным решением мебели и оборудования.
5. Перед началом каких-либо работ подрядчики должны сверить размеры на объекте.
6. Чистовую высоту стен уточнить после укладки стяжки и потолка.
7. Все высоты даны от чистого пола.
8. Размеры мебели уточняются производителем по месту.
9. Артикул и цвет краски и плитки уточнить по месту (при помощи выкрасов).

Дизайн проект интерьера
квартиры по адресу:
г. Москва ЖК "Headliner" 39/1


Стадия	Лист	Листов
РП	32	
Компания	Кодолов Групп	
Дизайнер	Заика Нина	
Дата	11.2022	

Все размеры уточнить на стадии
производственных работ

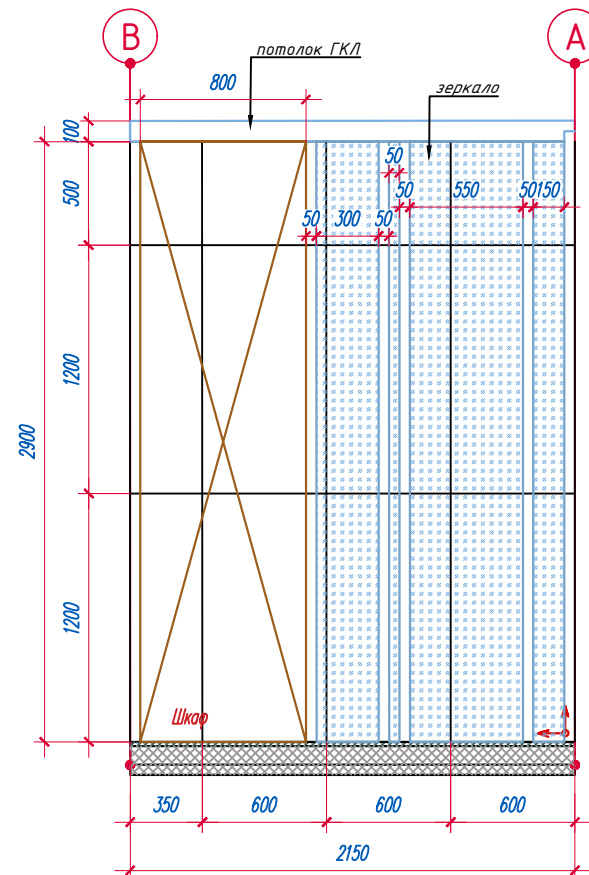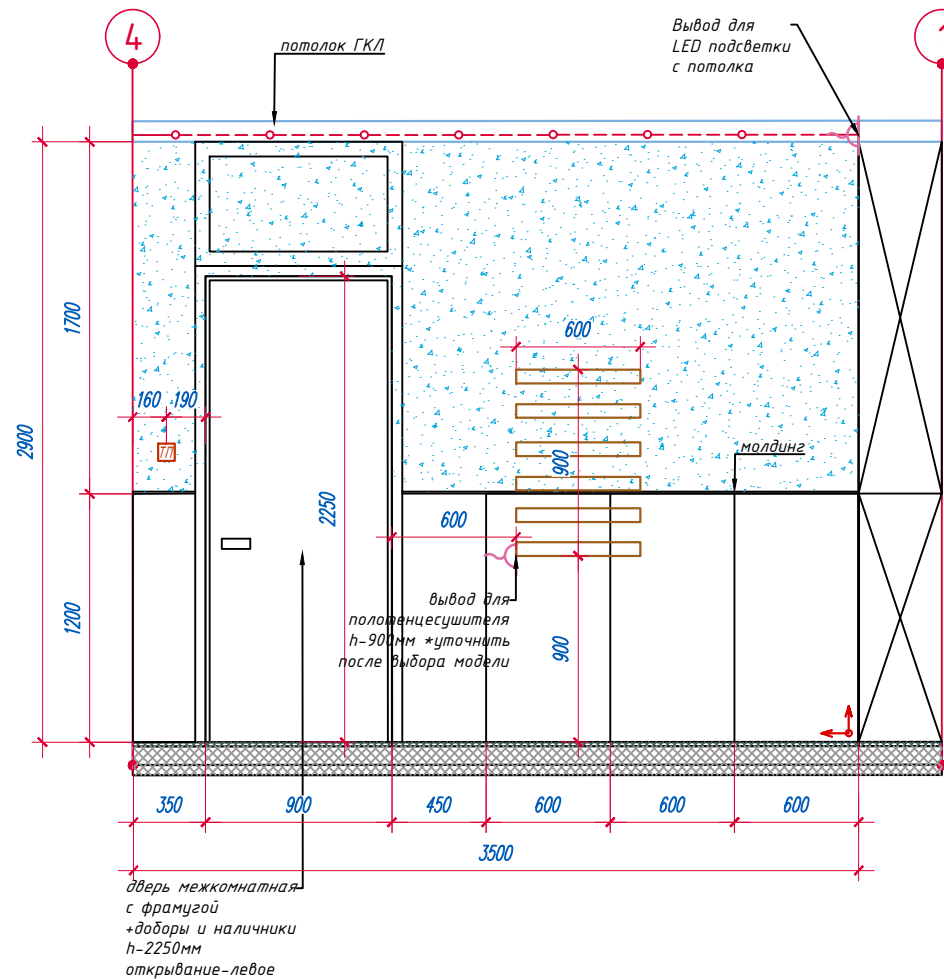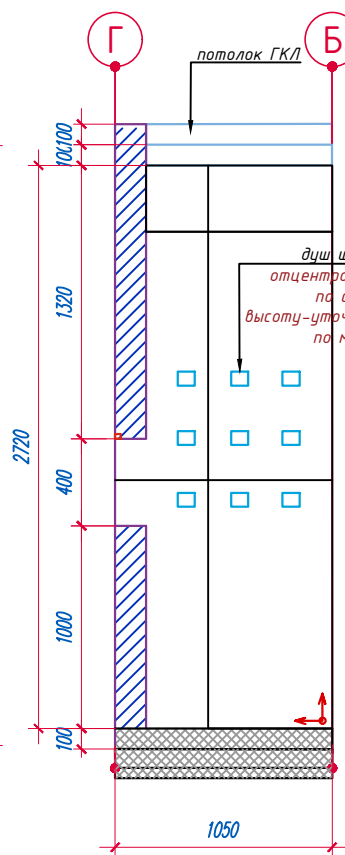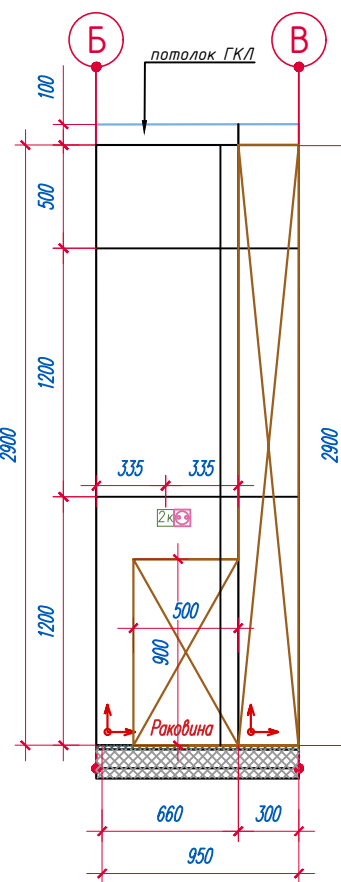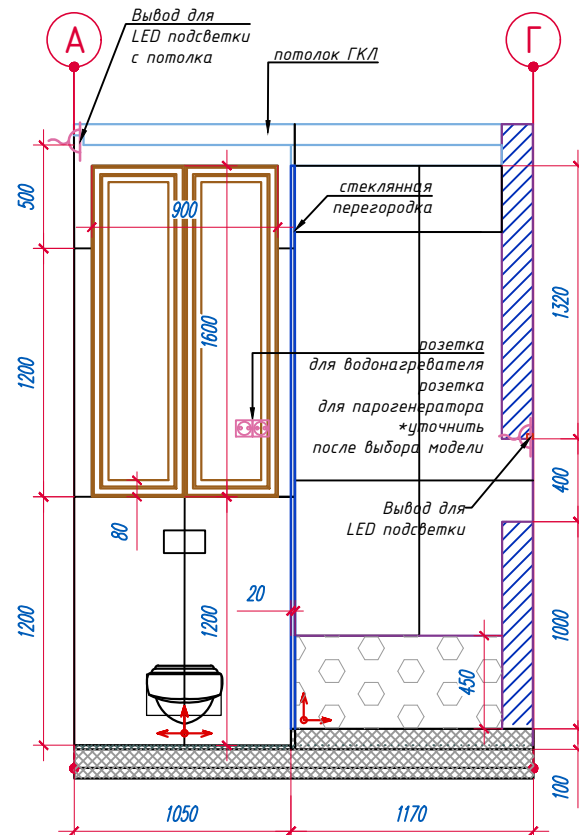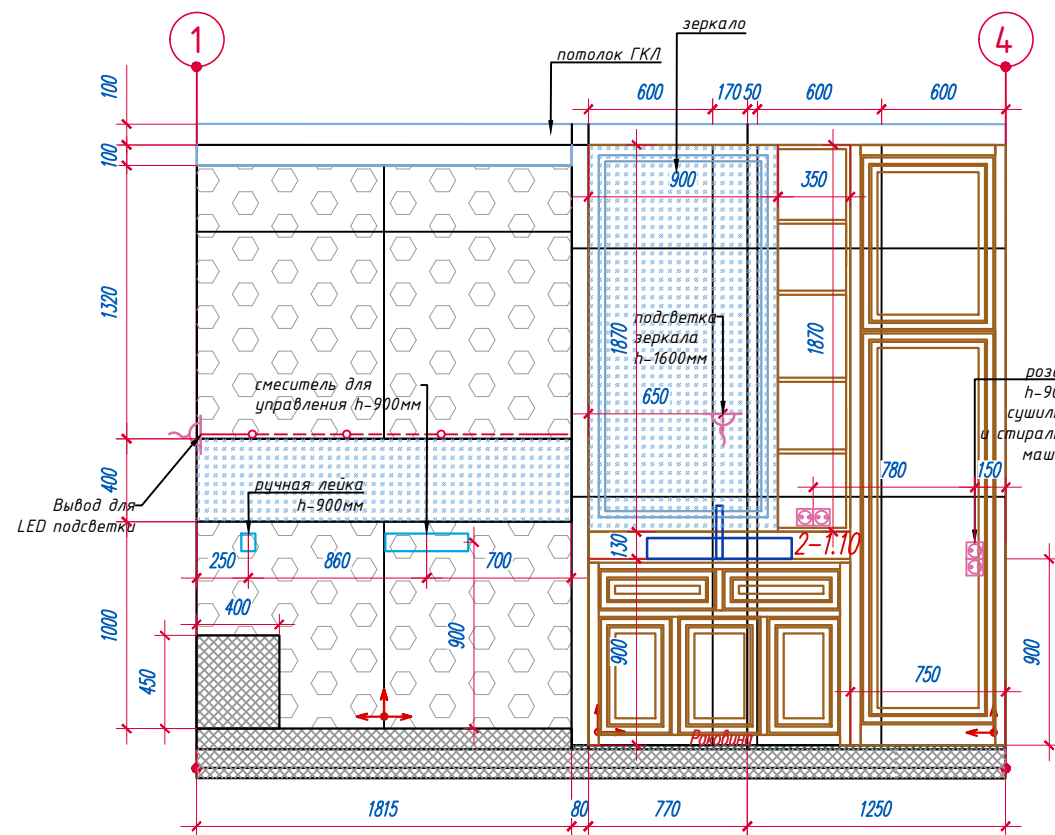

Примечание:
Предусмотреть лючки ревизии в необходимых местах!!

Все размеры и отметки, расход всех материалов, все площади уточняются по месту. На каждом объекте возможны увеличения или уменьшения размеров в зависимости от технических допусков, кривизны, расхождения уровней стен и потолков.

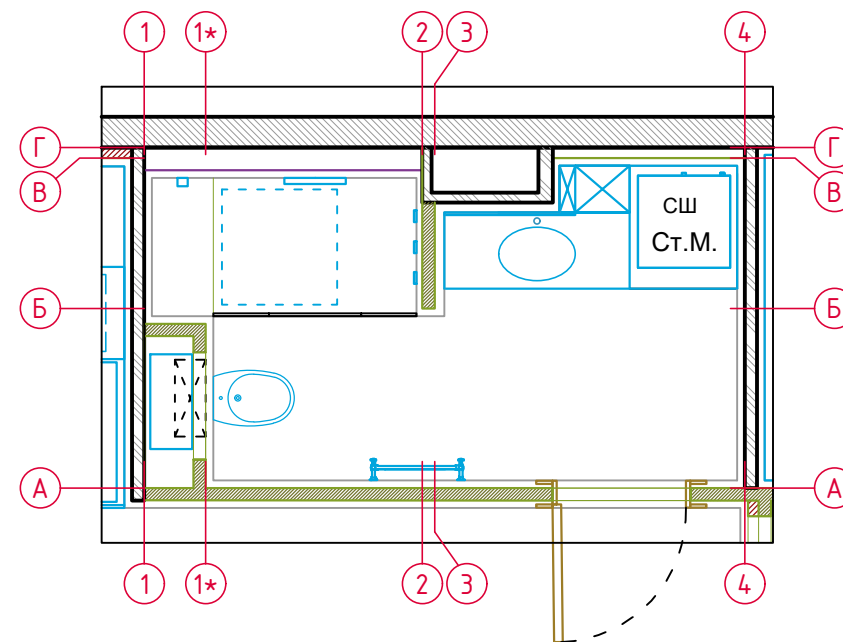

Развертки по душевой
(отделка стен,
расстановка мебели)

УСЛОВНЫЕ ОБОЗНАЧЕНИЯ


- А — ось привязки
- 201221P Selene Light Pol. керамогранит Dune 600x1200mm
- Canyon Purple Natural керамогранит LAND Porcelanico 1000x1000mm
- краска цвет — синяя
- зеркало

Начало раскладки

- Все размеры указаны от чистого пола до середины блока (центра блока)
- Размеры стен даны без учета штукатурного слоя отделочных материалов. Поэтому после проведения отделочных материалов рекомендуем сверить с проектом и внести изменения, либо согласовать в порядке авторского надзора с проектировщиком.
- Проектировщик не несет ответственности за достоверность информации, предоставленной производителями, за сроки поставки, качество выполненных работ, сроки монтажа субподрядными организациями.
- Смотреть совместно с планом розеток, выключателей, планировочным решением мебели и оборудования.
- Перед началом каких-либо работ подрядчики должны сверить размеры на объекте.
- Чистовую высоту стен уточнить после укладки стяжки и потолка
- Все высоты даны от чистого пола
- Размеры мебели уточняются производителем по месту
- Артикул и цвет краски и плитки уточнить по месту (при помощи выкрасов).

Дизайн проект интерьера квартиры по адресу: г. Москва ЖК "Headliner" 39/1		
Стадия	Лист	Листов
РП	33	
Компания	Коголов Групп	
Дизайнер	Заика Нина	
Дата	11.2022	

	Стены			Полы			Потолки			Дополнительные элементы		Ведомость учета материалов														
Наименование помещения	Отделка	Цвет	Кол-во	Отделка	Цвет	Кол-во	Отделка	Цвет	Кол-во	Тип осветительного прибора	Кол-во	УСЛОВНЫЕ ОБОЗНАЧЕНИЯ														
Прихожая Холл Кухня	краска	бежевый	31 кв.м	Инженерная Доска	дуб Мерлетто (brushed) 110511 190x1800мм	4,2 кв. м	ГВЛ крашенный	белый	25 кв. м	Светильник настенный Бра (включение с выключателя) прихожая Светильник настенный Бра (включение с выключателя) кухня Трек встроенный Г-образный прихожая Трек встроенный прямой кухня Свет.потолочный.Подвесной Свет.потолочный.Встроенный	2шт 2шт 2200x3100 мм 1960мм 1шт 4шт	1. Все площади указаны без запаса 2. Перед покупкой, уточнить площади на стройке. 3. Артикулы и цвет краски и плитки уточнить по месту (при помощи выкрасов).														
	Молдинг	PX116 Orac Decor 2000x31x10мм в цвет стены	22,5 п. м.																							
	ПЛИНТУС настенный	SX180 HIGH LINE Orac Decor 2000x120x16мм в цвет стены	22 п. м.																							
	ДЕКОРАТИВНЫЕ ПАНЕЛИ ДЛЯ СТЕН	W114 VALLEY XL 2000x250x15мм в цвет стены	1290x2660мм																							
	Керамогранит	188205 Selene Carrussino Pul. Dune 900x900мм	10шт																							
	зеркало	Смотри развертки	ст.30																							
Гостиная	краска	бежевый	36 кв.м	Инженерная Доска	дуб Мерлетто (brushed) 110511 190x1800мм	21 кв. м	ГВЛ крашенный	белый	20 кв. м	Свет.потолочный.Встроенный Свет.потолочный.Подвесной Встроенный световой профиль(потолоч.) форма- Квадрат Светильник настенный Бра (включение с выключателя) LED лента(1 трансформатор) LED лента(1 трансформатор)	8шт 1шт 1610x1330 мм 2шт 3300мм 5800мм	Дизайн проект интерьера квартиры по адресу: г. Москва ЖК "Headliner" 39/1														
	Керамогранит	Agata Black Luc. 6 mm Maxfine 1500x3000	1шт																							
	Молдинг	PX116 Orac Decor 2000x31x10мм в цвет стены	36,5 п. м.																							
	ПЛИНТУС настенный	SX180 HIGH LINE Orac Decor 2000x120x16мм в цвет стены	42,5 п. м.																							
	ДЕКОРАТИВНЫЕ ПАНЕЛИ ДЛЯ СТЕН	W114 VALLEY XL 2000x250x15мм в цвет стены	1070x2100мм -2 шт																							
		цвет белый	Смотри развертки ст.,32																							
	зеркало	Смотри развертки	ст.31,32																							
															Стадия	Лист	Листов									
																34										
															Компания	Коголов Групп										
												Дизайнер	Заика Нина													
												Дата	11.2022													

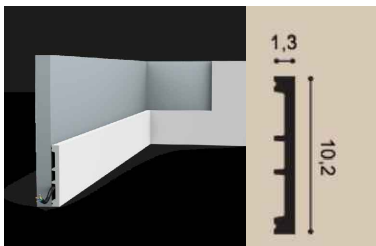	Стены			Полы			Потолки			Дополнительные элементы		Ведомость учета материалов		
Наименование помещения	Отделка	Цвет	Кол-во	Отделка	Цвет	Кол-во	Отделка	Цвет	Кол-во	Тип осветительного прибора	Кол-во	УСЛОВНЫЕ ОБОЗНАЧЕНИЯ		
Спальня Гардероб	краска	голубой	31 кв.м	Инженерная Доска	дуб Мерлетто (brushed) 110511 190x1800мм	21 кв.м	ГВЛ крашенный	белый	20 кв.м	Свет.потолочный.Встроенный гардероб	3шт	1. Все площади указаны без запаса 2. Перед покупкой, уточнить площади на стройке. 3. Артикулы и цвет краски и плитки уточнить по месту (при помощи выкрасов). ПЛИНТУС SX163 SQUARE Orac Decor g 2000 x в 101 x ш 13 мм – 54 п.м 		
	краска	серый	31 кв.м				ПОТОЛОЧНЫЙ БОРДЮР	C991 Orac Decor 2000x110x140мм в цвет стены	27 п.м.	Свет.потолочный.Встроенный в коридоре	3шт			
	Молдинг	PX116 Orac Decor 2000x31x10мм в цвет стены	41 п.м.					Молдинг	PX116 Orac Decor 2000x31x10мм белый	8,8 п.м.	Свет.потолочный.Встроенный У окна		3шт	
	ПЛИНТУС настенный	SX180 HIGH LINE Orac Decor 2000x120x16мм в цвет стены	87 п.м.							Свет.потолочный.Подвесной Над прикров.тумбами	3шт			
	ДЕКОРАТИВНЫЕ ПАНЕЛИ ДЛЯ СТЕН	W114 VALLEY XL 2000x250x15мм в цвет стены	1800x 1550мм 2350x 660мм							Свет.потолочный.Подвесной LED лента(1 трансформатор)	1шт 7000мм			
	зеркало в гардеробе зеркало в коридоре	зеркало зеркало	1460x 2160мм 770x 2420мм											
Душевая	краска	синяя	5 кв.м	Керамогранит	201221P Selene Light Pol. Dune 600x1200мм	10 шт	ГВЛ крашенный	белый	5,3 кв.м	Свет.потолочный.Встроенный	3шт	Дизайн проект интерьера квартиры по адресу: г. Москва ЖК "Headliner" 39/1 Стадия Лист Листов 35 Компания Коголов Групп Дизайнер Заика Нина Дата 11.2022		
	профиль г-образный	золотой	2700мм								Свет.потолочный.Накладной		1шт	
	Керамогранит	201221P Selene Light Pol. Dune 600x1200мм	42 шт	Керамогранит	Canyon Purple Natural LAND Porcelanico 1000x1000мм	3 шт	Керамогранит	Canyon Purple Natural LAND Porcelanico 1000x1000мм	2 шт	Встроенная трековая система	1200мм			
	Керамогранит	Canyon Purple Natural LAND Porcelanico 1000x1000мм	7 шт	Пробковый разделитель	в цвет инженерной доски	900мм				LED лента(1 трансформатор)	2660мм –2шт			
	зеркало	зеркало	400*1800 мм							LED лента(1 трансформатор)	1800мм			